
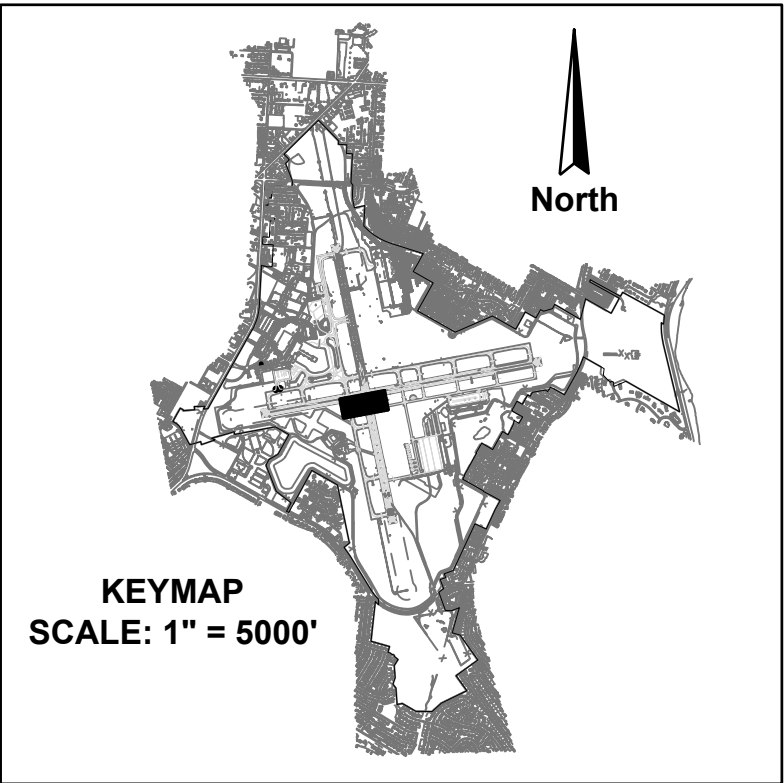


N:\359 CITY OF PENSACOLA-AIRPORT\2024-0359.01-PNS RUNWAY 8-26\000 CAD\24035901_E201-211.DWG 4/11/2025 11:20 AM

NOTES:

1. SEE SHEET E201 FOR GENERAL LAYOUT NOTES.

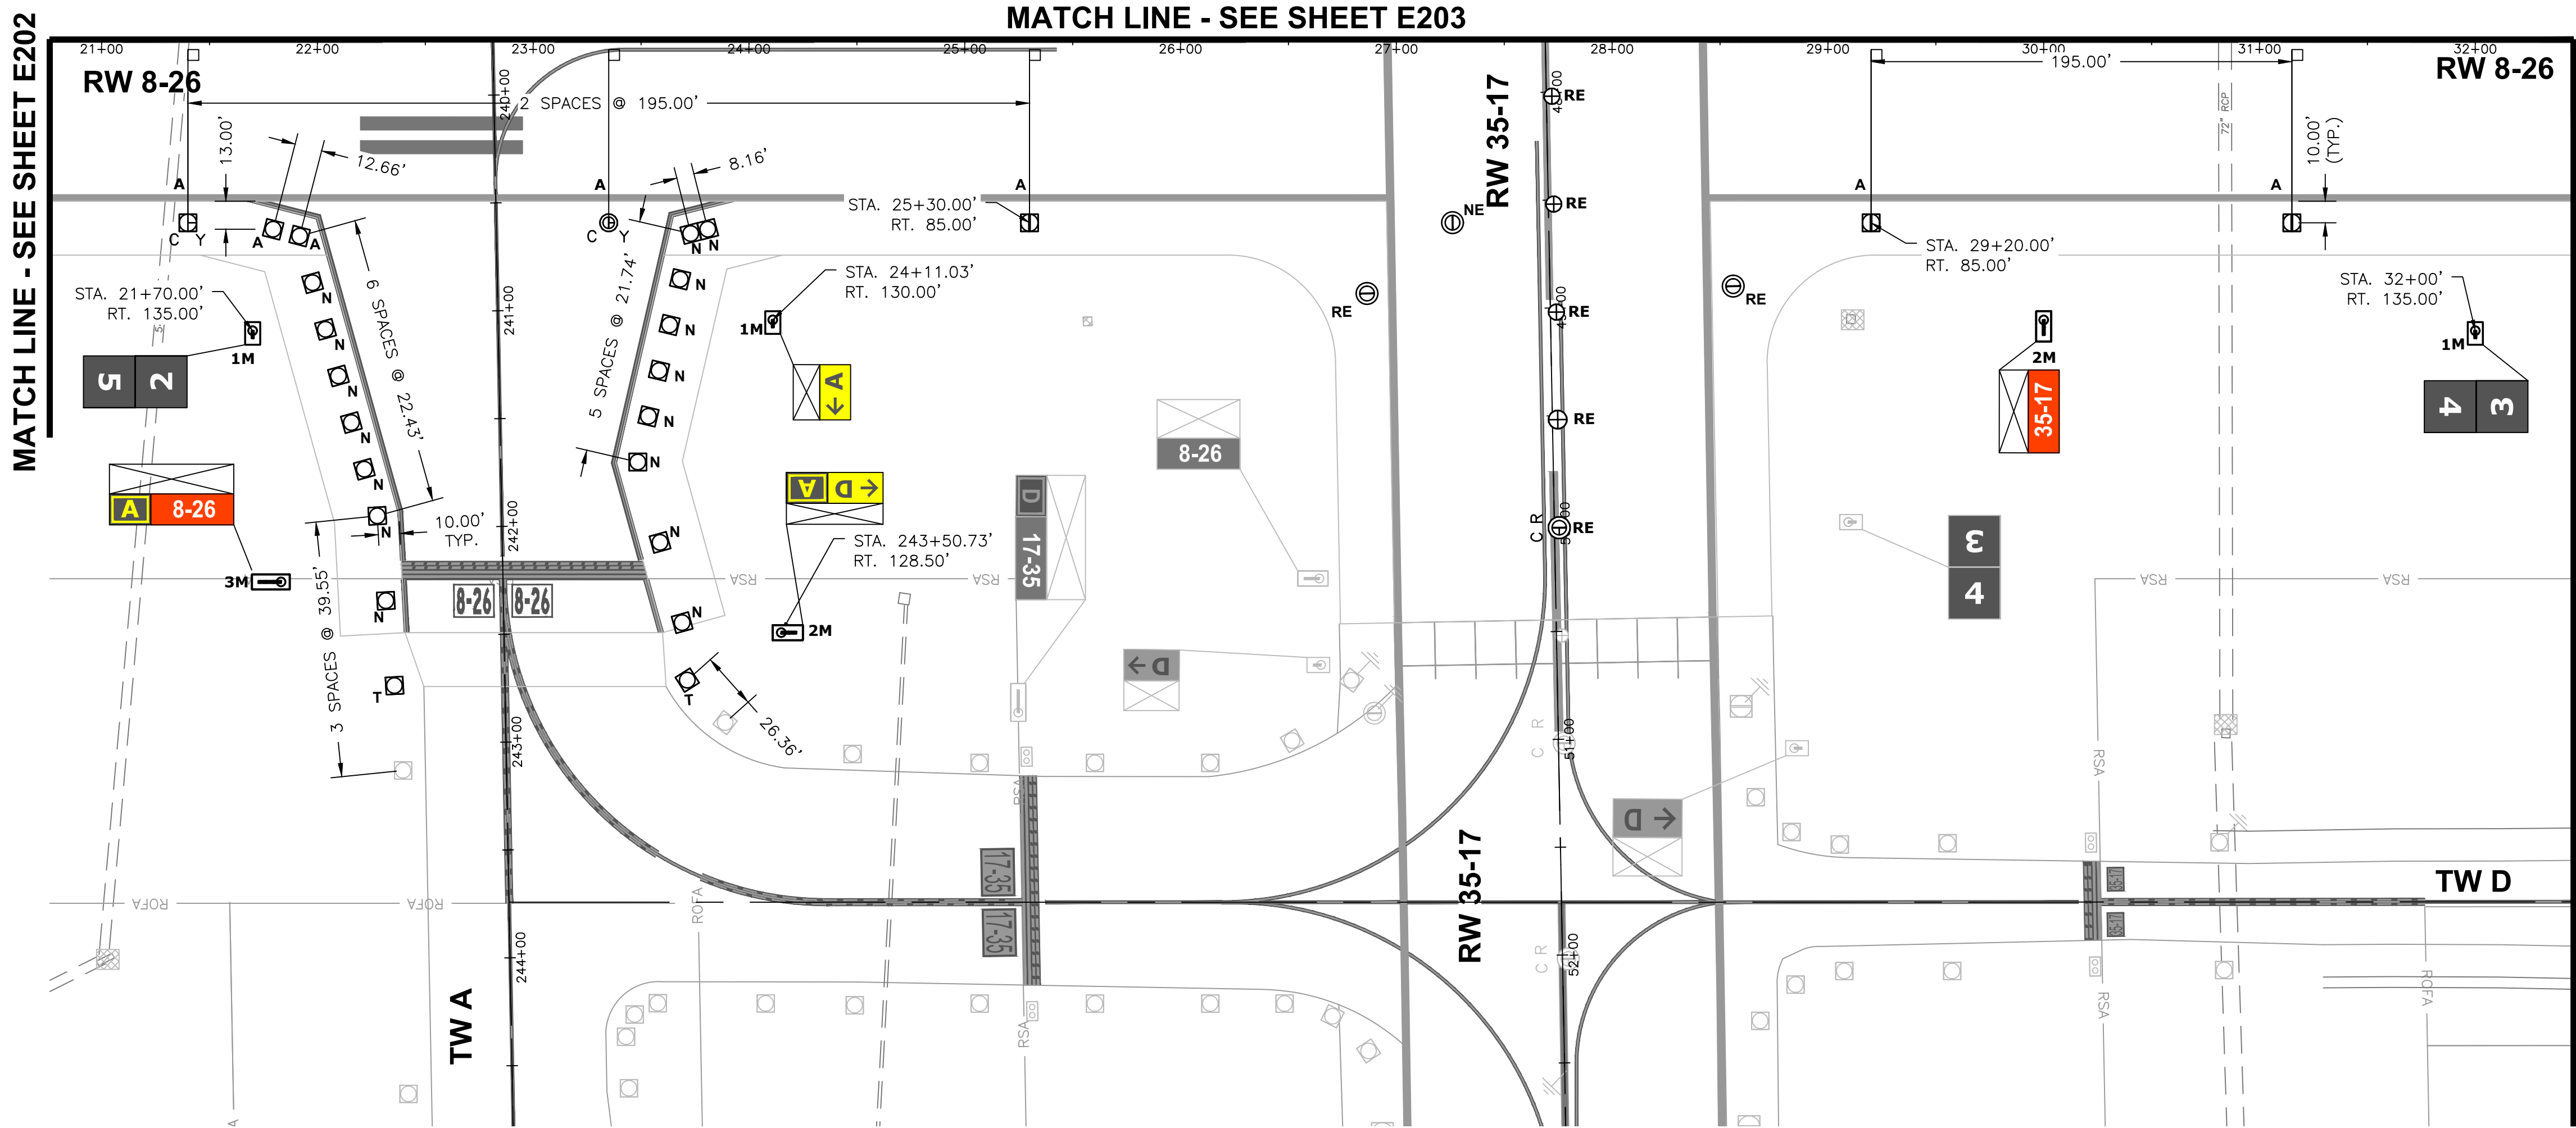

RUNWAY 8-26
REHABILITATION

AIRFIELD LIGHTING
LAYOUT PLAN
(SHEET 4 OF 11)

NO.	DATE	REVISION	BY
1	4/25	ADDENDUM 3	SAH
2			
3			
4			
5			
6			
7			
8			
9			
10			

DESIGNED BY: SAH
DRAWN BY: KJF
CHECKED BY: MAG
APPROVED BY: VCL
PROJECT NO: 24.0359.01
DATE: MARCH 28, 2025

SHEET NUMBER
E204

TRANSFORMING TODAY'S IDEAS
INTO TOMORROW'S REALITY

AVCON, INC.
ENGINEERS & PLANNERS
3298 SUMMIT BLVD., SUITE 26
PENSACOLA, FL 32503
OFFICE: (850) 688-3526
CORPORATE CERTIFICATE OF
AUTHORIZATION NUMBER: 5057
WWW.AVCONINC.COM

THIS DOCUMENT CONTAINS PRIVILEGED AND PROPRIETARY INFORMATION. ALL OF WHICH IS EXPRESSLY PROVIDED BY AVCON, INC., FOR USE BY THE INTENDED RECIPIENT, AND FOR A SPECIFIC PURPOSE. WITHOUT THE EXPRESS WRITTEN CONSENT OF AVCON, INC., ANY DISTRIBUTION, REPRODUCTION, OR OTHER USE OF THIS DOCUMENT, IN WHOLE OR IN PART, IS STRICTLY PROHIBITED.