




N:\359 CITY OF PENSACOLA-AIRPORT\2024.0359.01-PNS RUNWAY 8-26\000 CAD\24035901\_E201-211.DWG 4/11/2025 11:21 AM

MATCH LINE - SEE SHEET E206

MATCH LINE - SEE SHEET E205

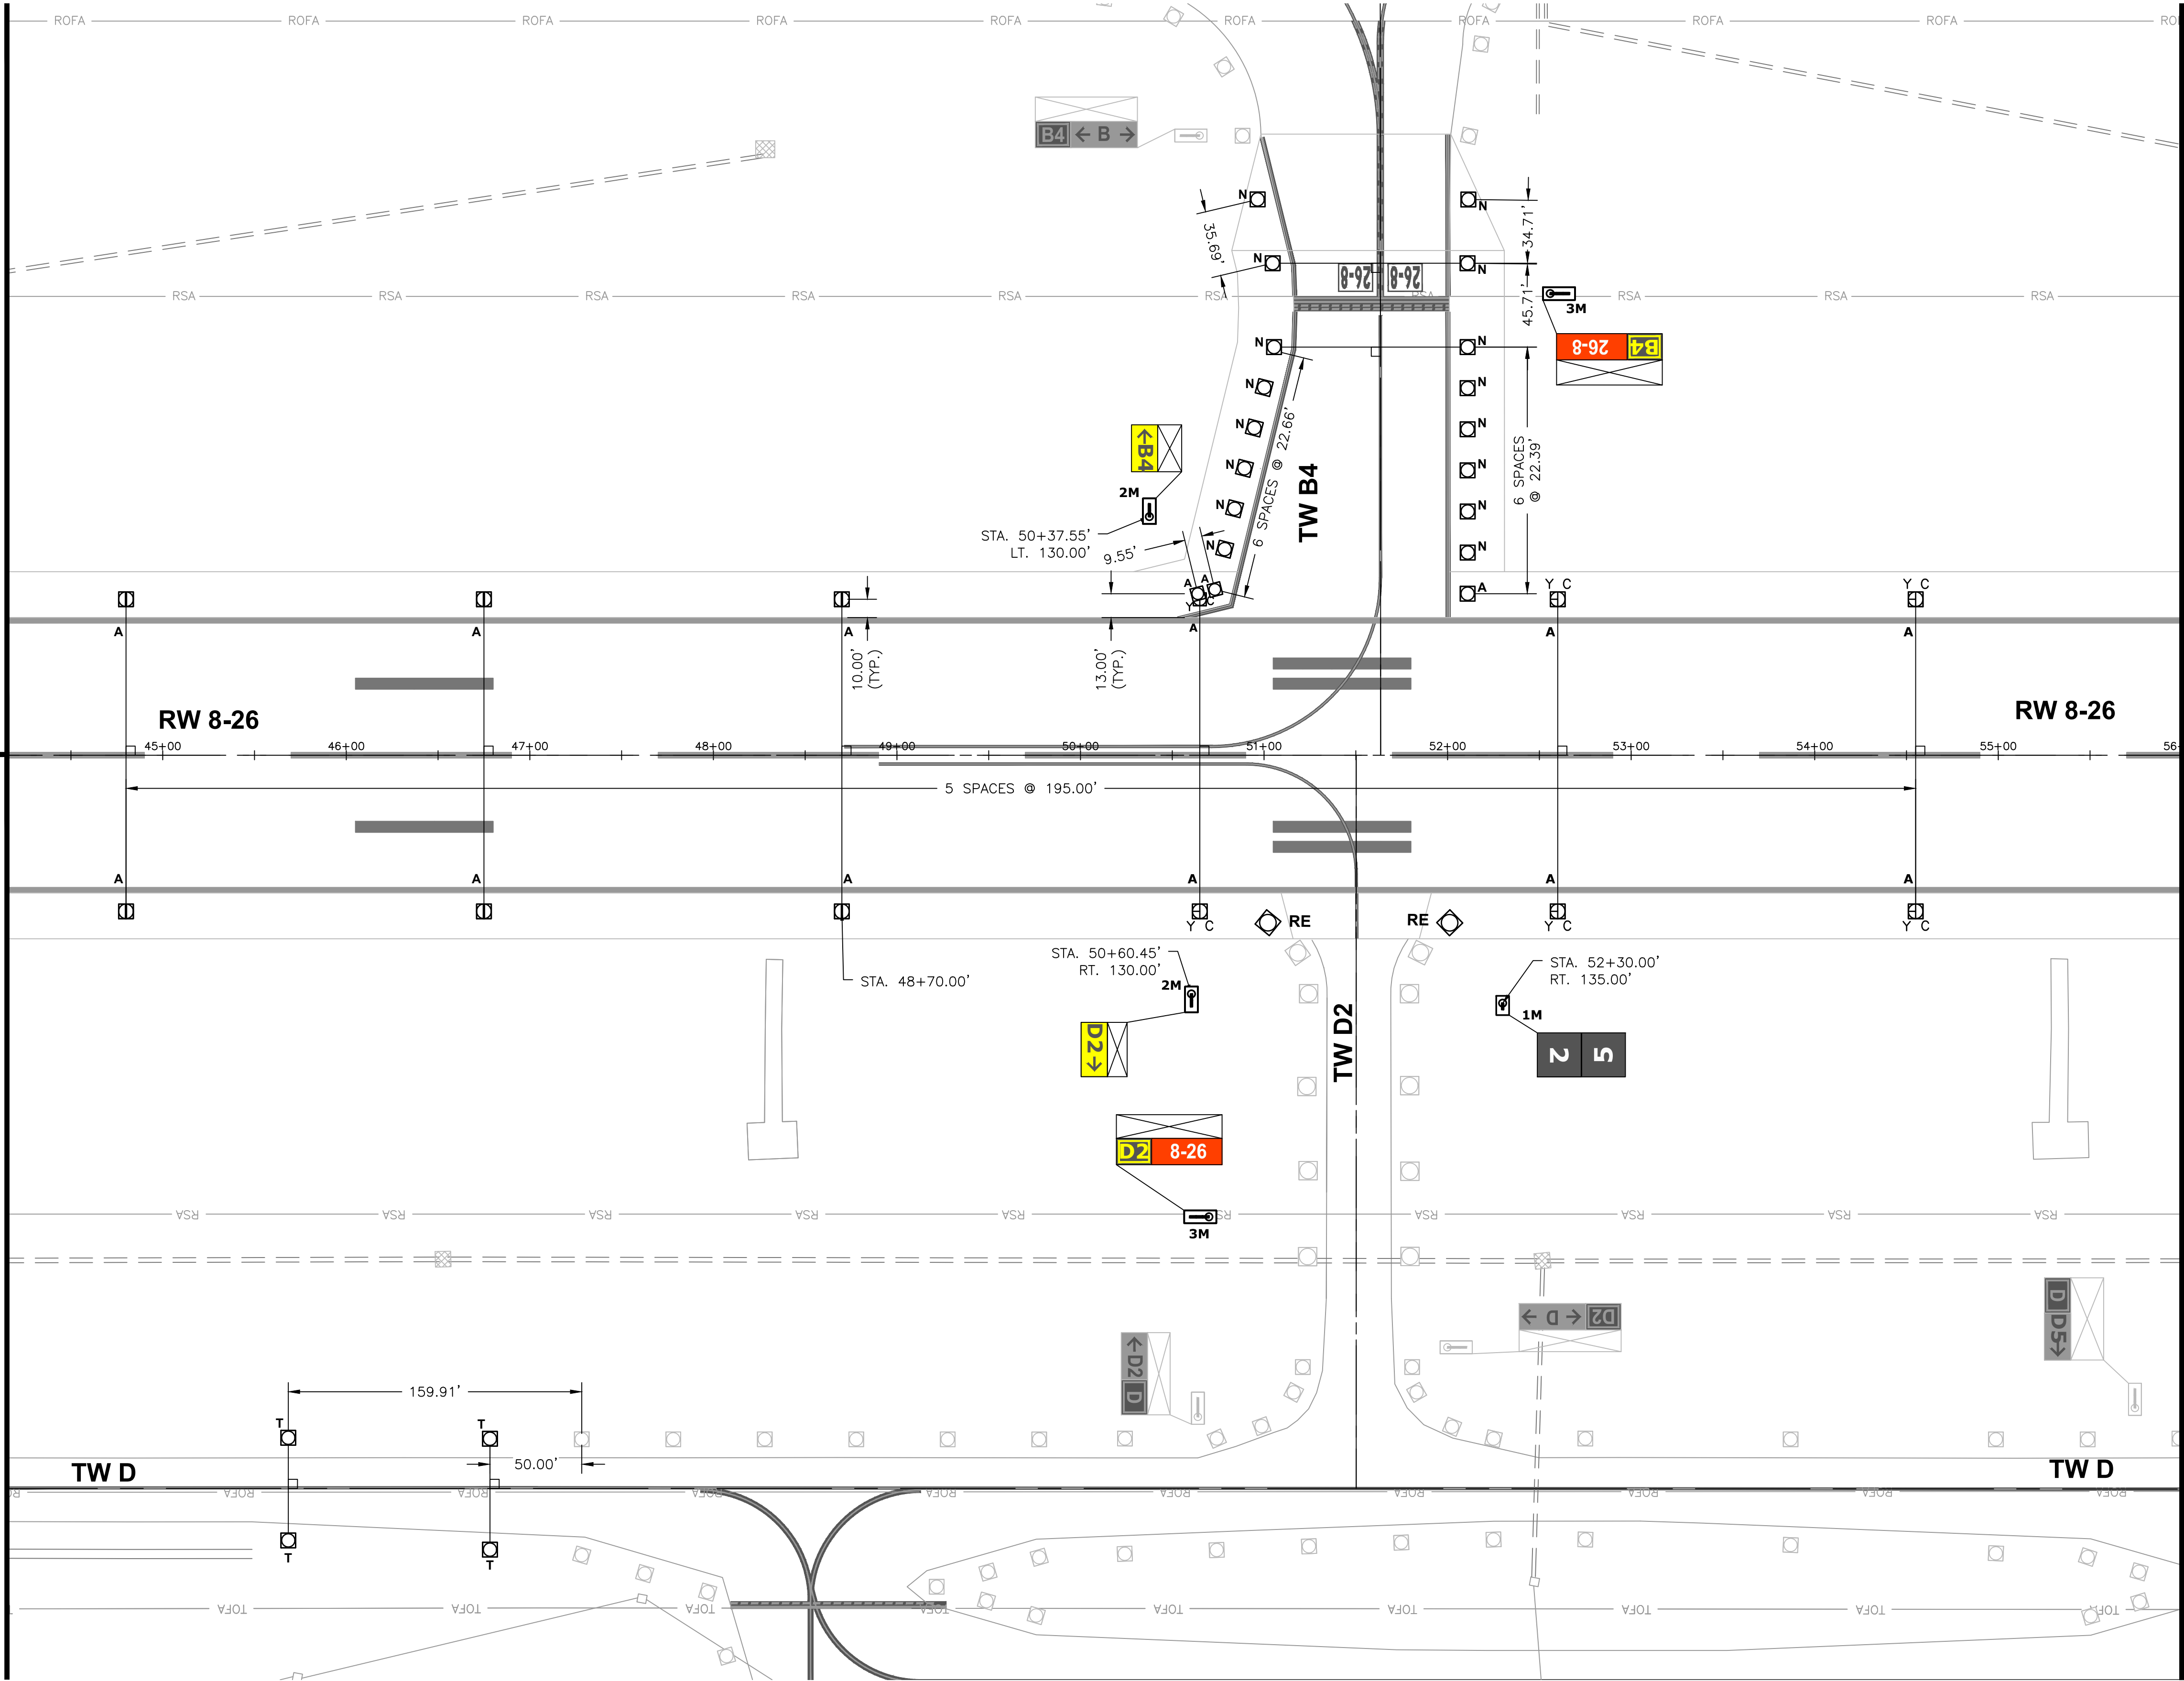

- NOTES:**
- SEE SHEET E201 FOR GENERAL LAYOUT NOTES.

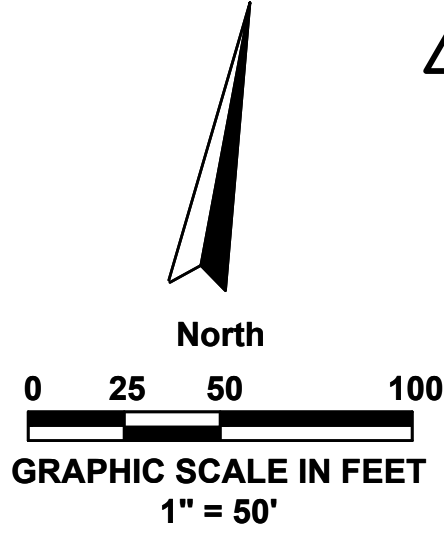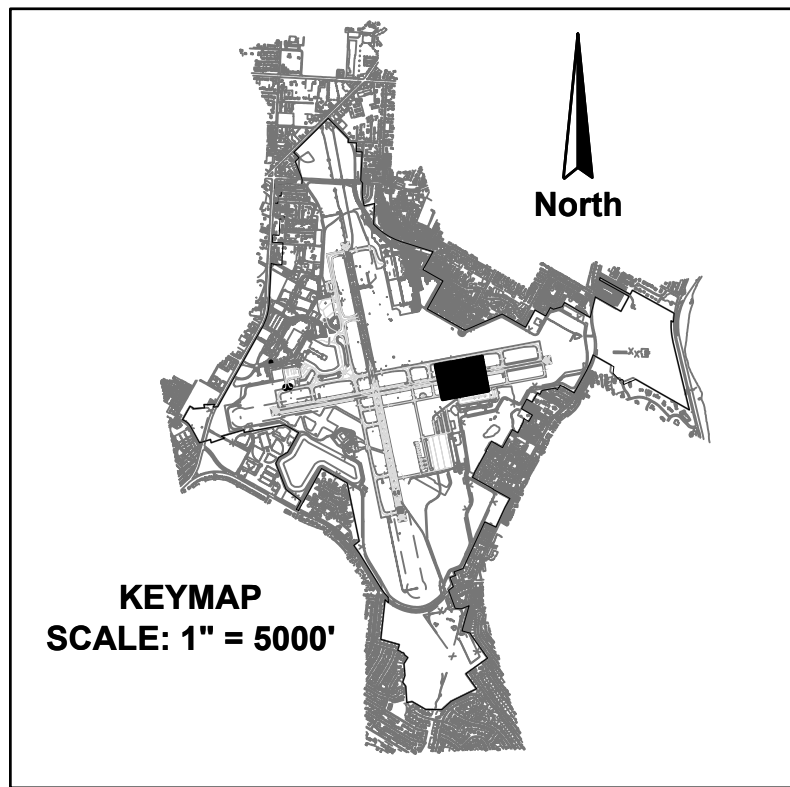

MATCH LINE - SEE SHEET E208

**RUNWAY 8-26  
REHABILITATION**

PREPARED FOR  
PENSACOLA INTERNATIONAL AIRPORT

**AIRFIELD LIGHTING  
LAYOUT PLAN  
(SHEET 7 OF 11)**

ISSUED FOR BID DRAWINGS

| NO. | DATE | REVISION   | BY  |
|-----|------|------------|-----|
| 1   | 4/25 | ADDENDUM 3 | SAH |
| 2   |      |            |     |
| 3   |      |            |     |
| 4   |      |            |     |
| 5   |      |            |     |
| 6   |      |            |     |
| 7   |      |            |     |
| 8   |      |            |     |
| 9   |      |            |     |
| 10  |      |            |     |

**AVCON, INC.**  
ENGINEERS & PLANNERS  
3298 SUMMIT BLVD., SUITE 26  
PENSACOLA, FL 32503  
OFFICE: (850) 688-3326  
CORPORATE CERTIFICATE OF  
AUTHORIZATION NUMBER: 5057  
WWW.AVCONINC.COM

TRANSFORMING TODAY'S IDEAS  
INTO TOMORROW'S REALITY

DESIGNED BY: SAH  
DRAWN BY: KJF  
CHECKED BY: MAG  
APPROVED BY: VCL  
PROJECT NO: 24.0359.01  
DATE: MARCH 28, 2025

**SHEET NUMBER  
E207**