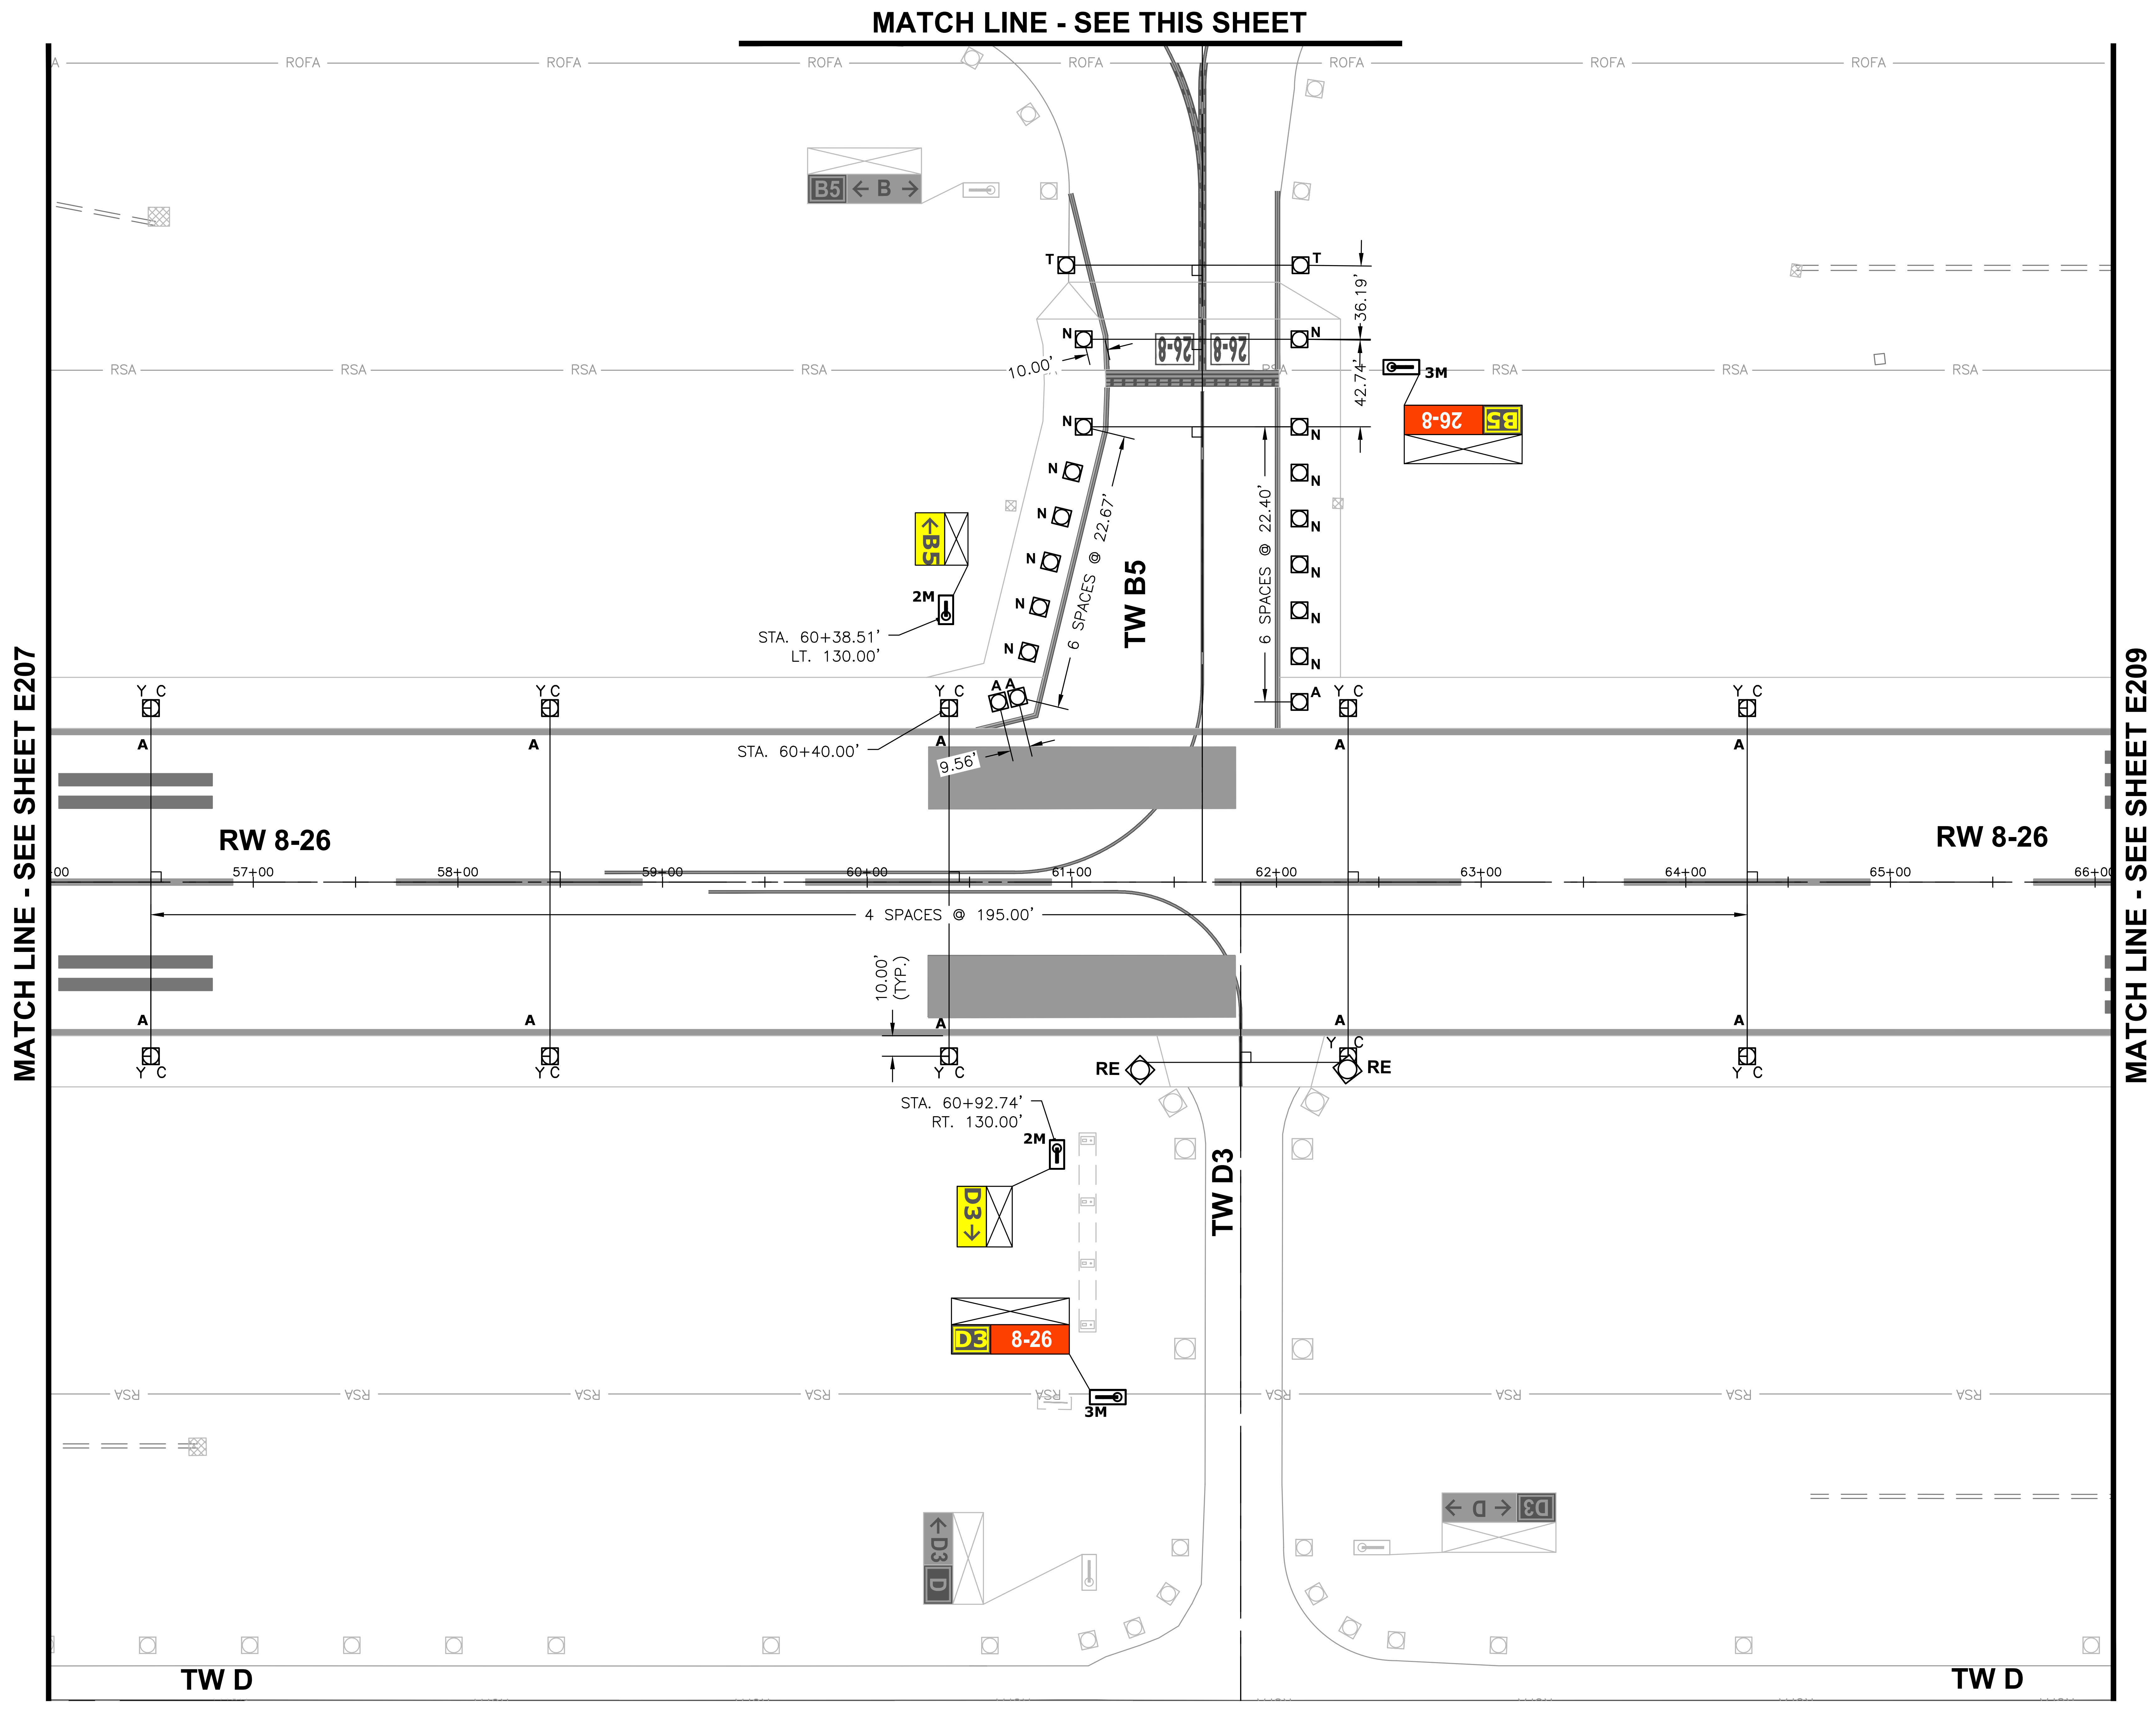

NOTES:

1. SEE SHEET E201 FOR GENERAL LAYOUT NOTES.

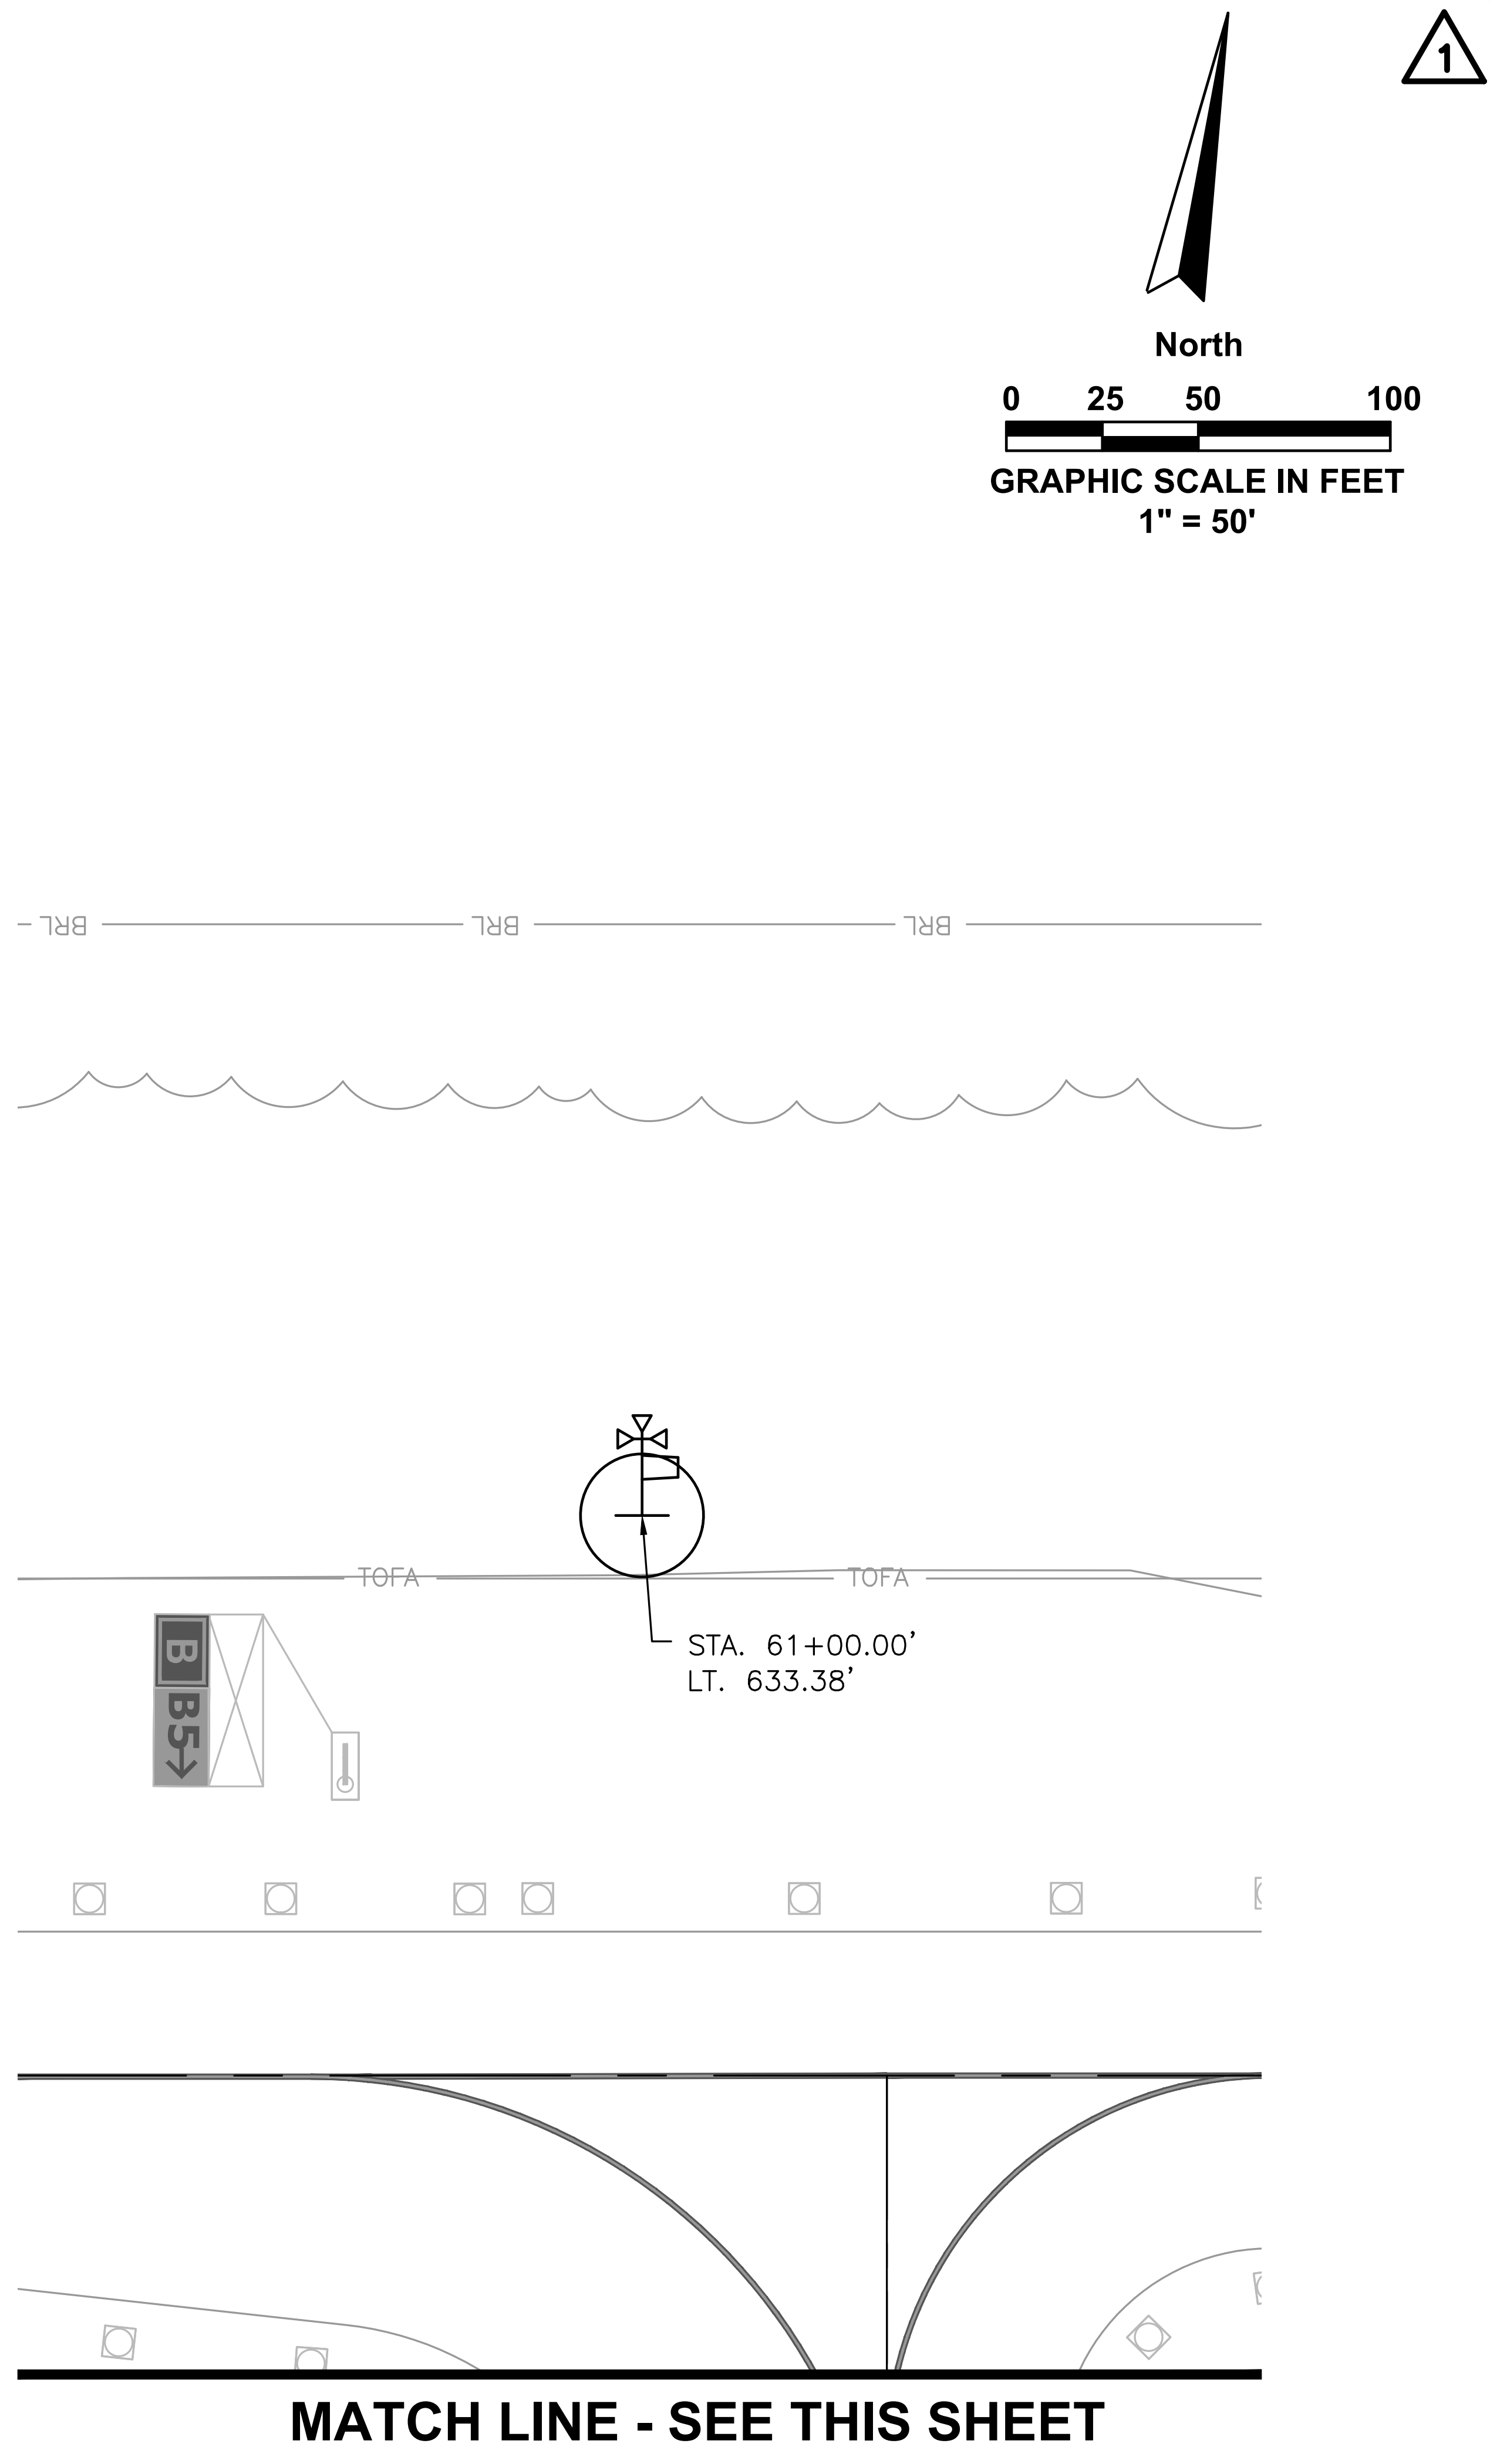

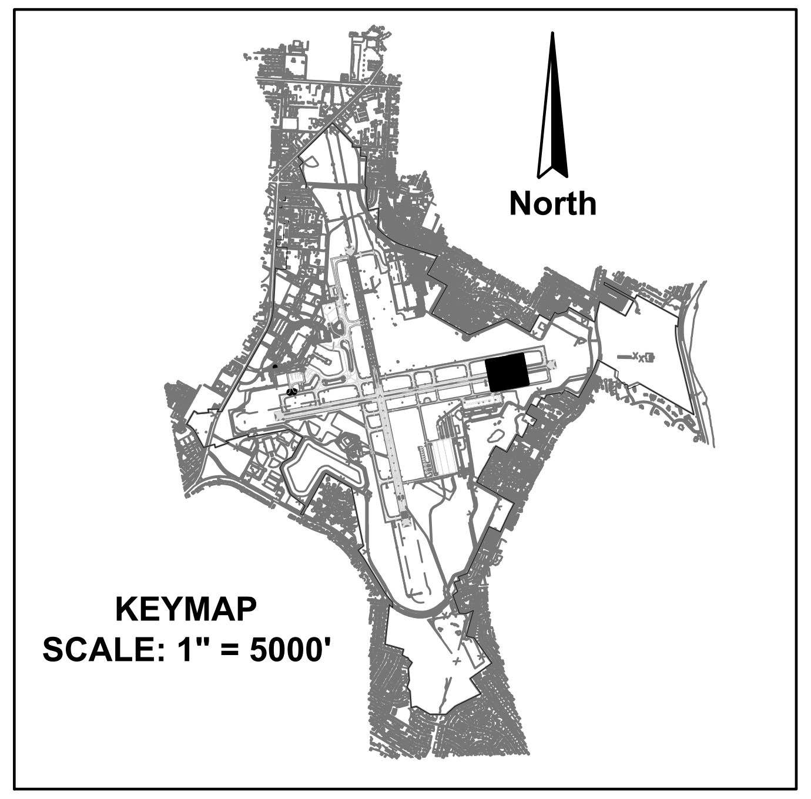

KEYMAP
SCALE: 1" = 5000'

AVCON, INC.
ENGINEERS & PLANNERS
3298 SUMMIT BLVD., SUITE 26
PENSACOLA, FL 32503
OFFICE: (850) 698-3526
CORPORATE CERTIFICATE OF
AUTHORIZATION NUMBER: 5057
www.avconinc.com

N:\NICEVILLE-CAD\002_LOGOS\JPEG\Avcon LOGO pms.jpg

*TRANSFORMING TODAY'S IDEAS
INTO TOMORROW'S REALITY*

NO.	DATE	REVISION	BY
1	4/25	ADDENDUM 3	SAH

AIRFIELD LIGHTING LAYOUT PLAN (SHEET 8 OF 11)

ISSUED FOR BID DRAWINGS

RUNWAY 8-26 REHABILITATION

PREPARED FOR
PENSACOLA INTERNATIONAL AIRPORT

DESIGNED BY: SAH
DRAWN BY: KJF
CHECKED BY: MAG
APPROVED BY: VCL
PROJECT NO: 24.0359.01
DATE: MARCH 28, 2025

SHEET NUMBER
E208

THIS DOCUMENT CONTAINS PRIVILEGED AND PROPRIETARY INFORMATION, ALL OF WHICH IS EXPRESSLY PROVIDED BY AVCON, INC., FOR USE BY THE INTENDED RECIPIENT, AND FOR A SPECIFIC PURPOSE. WITHOUT THE EXPRESS WRITTEN CONSENT OF AVCON, INC. ANY DISTRIBUTION, REPRODUCTION, OR OTHER USE OF THIS DOCUMENT, IN WHOLE OR IN PART, IS STRICTLY PROHIBITED

N:\359 CITY OF PENSACOLA-AIRPORT\2024.0359.01-PNS RUNWAY 8-26\000 CAD\24035901_E201-211.DWG 4/11/2025 11:21 AM