




N:\359 CITY OF PENSACOLA-AIRPORT\2024.0359.01-PNS RUNWAY 8-26\000 CAD\24035901\_E201-211.DWG 4/11/2025 11:21 AM

MATCH LINE - SEE SHEET E208

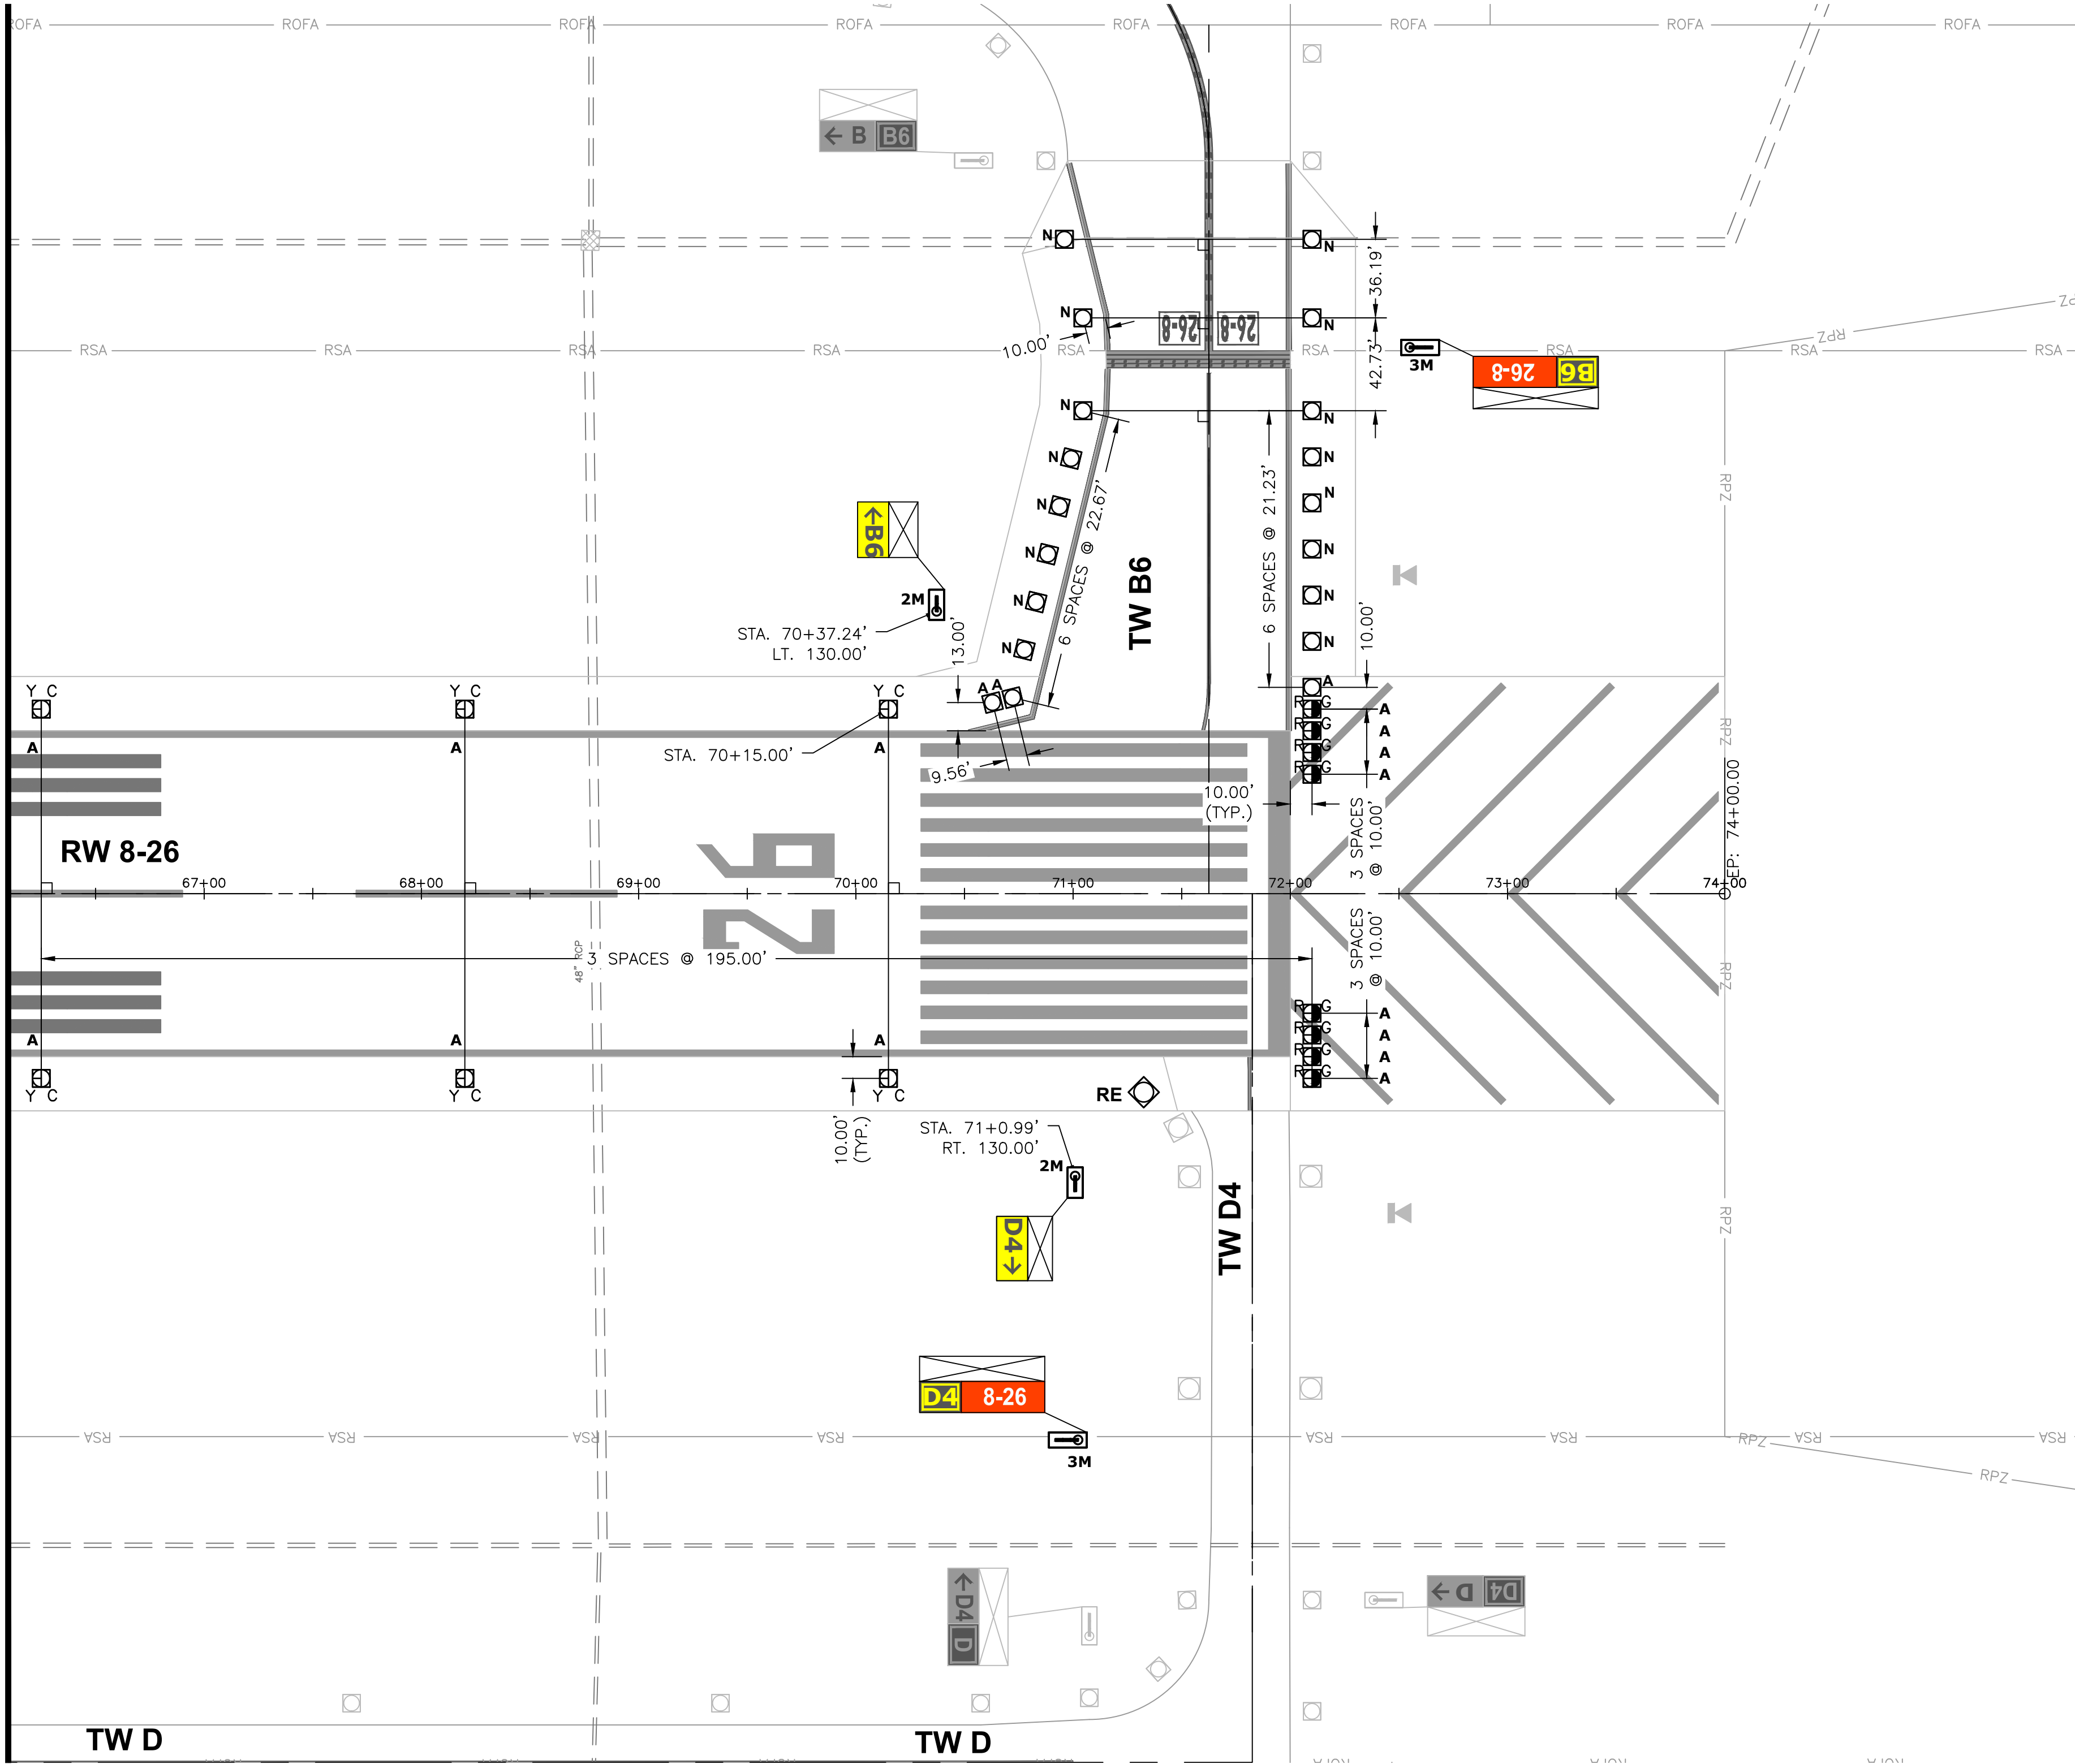

NOTES:

1. SEE SHEET E201 FOR GENERAL LAYOUT NOTES.

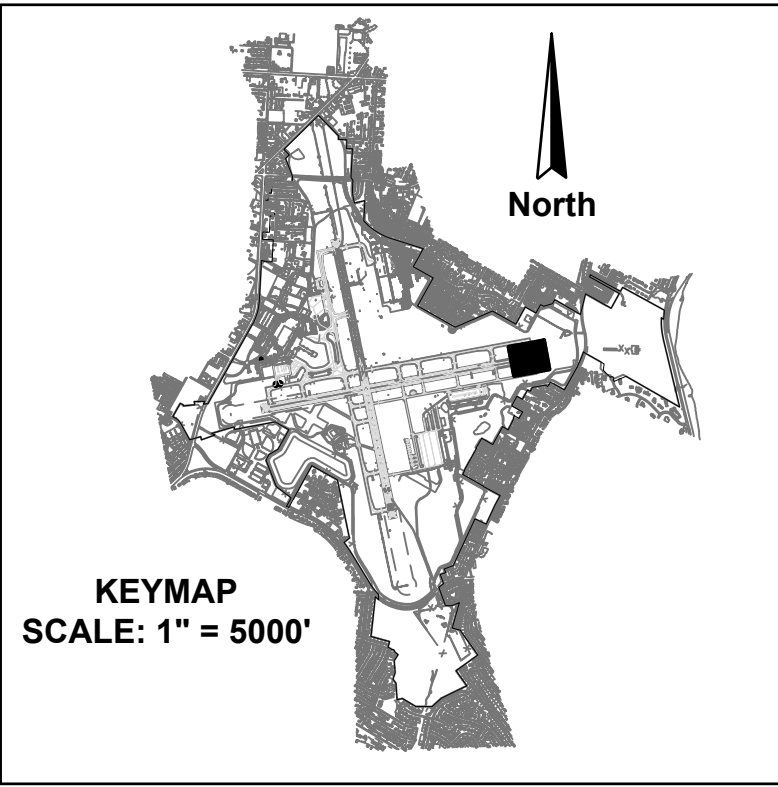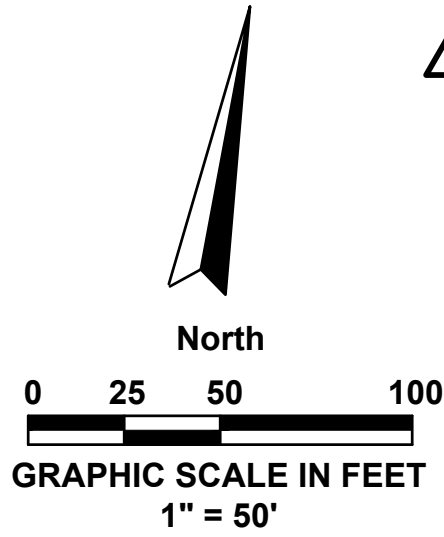

RUNWAY 8-26  
REHABILITATION  
PREPARED FOR  
PENSACOLA INTERNATIONAL AIRPORT

DESIGNED BY: SAH  
DRAWN BY: KJF  
CHECKED BY: MAG  
APPROVED BY: VCL  
PROJECT NO: 24.0359.01  
DATE: MARCH 28, 2025

SHEET NUMBER  
E209

AIRFIELD LIGHTING  
LAYOUT PLAN  
(SHEET 9 OF 11)  
ISSUED FOR BID DRAWINGS

| NO. | DATE | REVISION   | BY  |
|-----|------|------------|-----|
| 1   | 4/25 | ADDENDUM 3 | SAH |
|     |      |            |     |
|     |      |            |     |
R:\NICKLE-CAD\02\_LOGS\AVCON\LOGS.pptx  
TRANSFORMING TODAY'S IDEAS  
INTO TOMORROW'S REALITY

AVCON, INC.  
ENGINEERS & PLANNERS  
3298 SUMMIT BLVD., SUITE 26  
PENSACOLA, FL 32503  
OFFICE: (850) 688-3326  
CORPORATE CERTIFICATE OF  
AUTHORIZATION NUMBER: 5057  
WWW.AVCONINC.COM

THIS DOCUMENT CONTAINS PRIVILEGED AND PROPRIETARY INFORMATION, ALL OF WHICH IS EXPRESSLY PROVIDED BY AVCON, INC., FOR USE BY THE INTENDED RECIPIENT, AND FOR A SPECIFIC PURPOSE. WITHOUT THE EXPRESS WRITTEN CONSENT OF AVCON, INC. ANY DISTRIBUTION, REPRODUCTION, OR OTHER USE OF THIS DOCUMENT, IN WHOLE OR IN PART, IS STRICTLY PROHIBITED.