
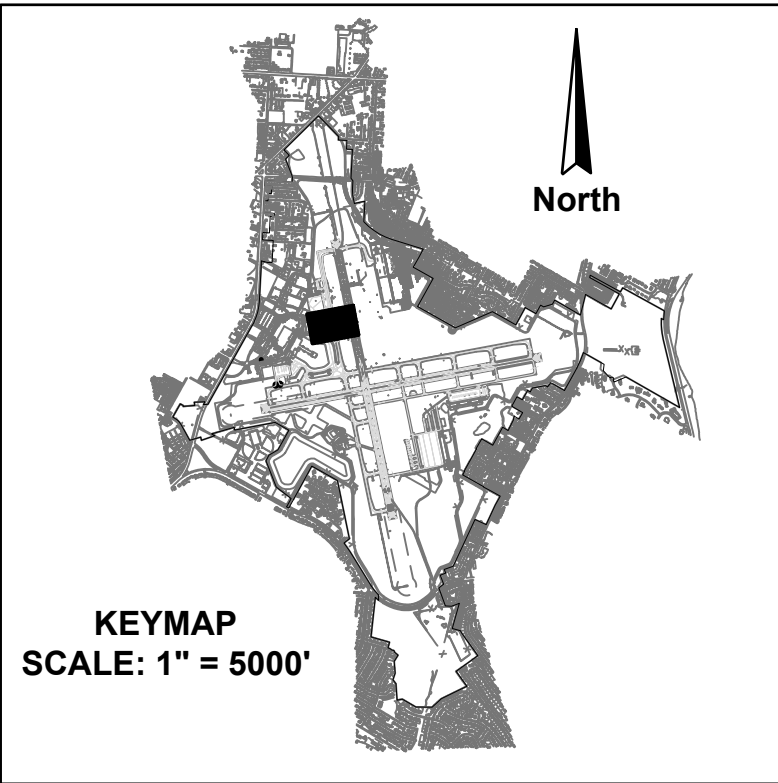
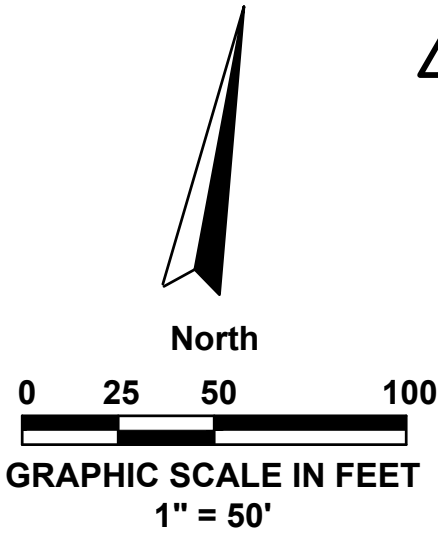


N:\359 CITY OF PENSACOLA-AIRPORT\2024-0359.01-PNS RUNWAY 8-26\000 CAD\24035901_E201-211.DWG 4/11/2025 11:22 AM

NOTES:
1. SEE SHEET E201 FOR GENERAL LAYOUT NOTES.

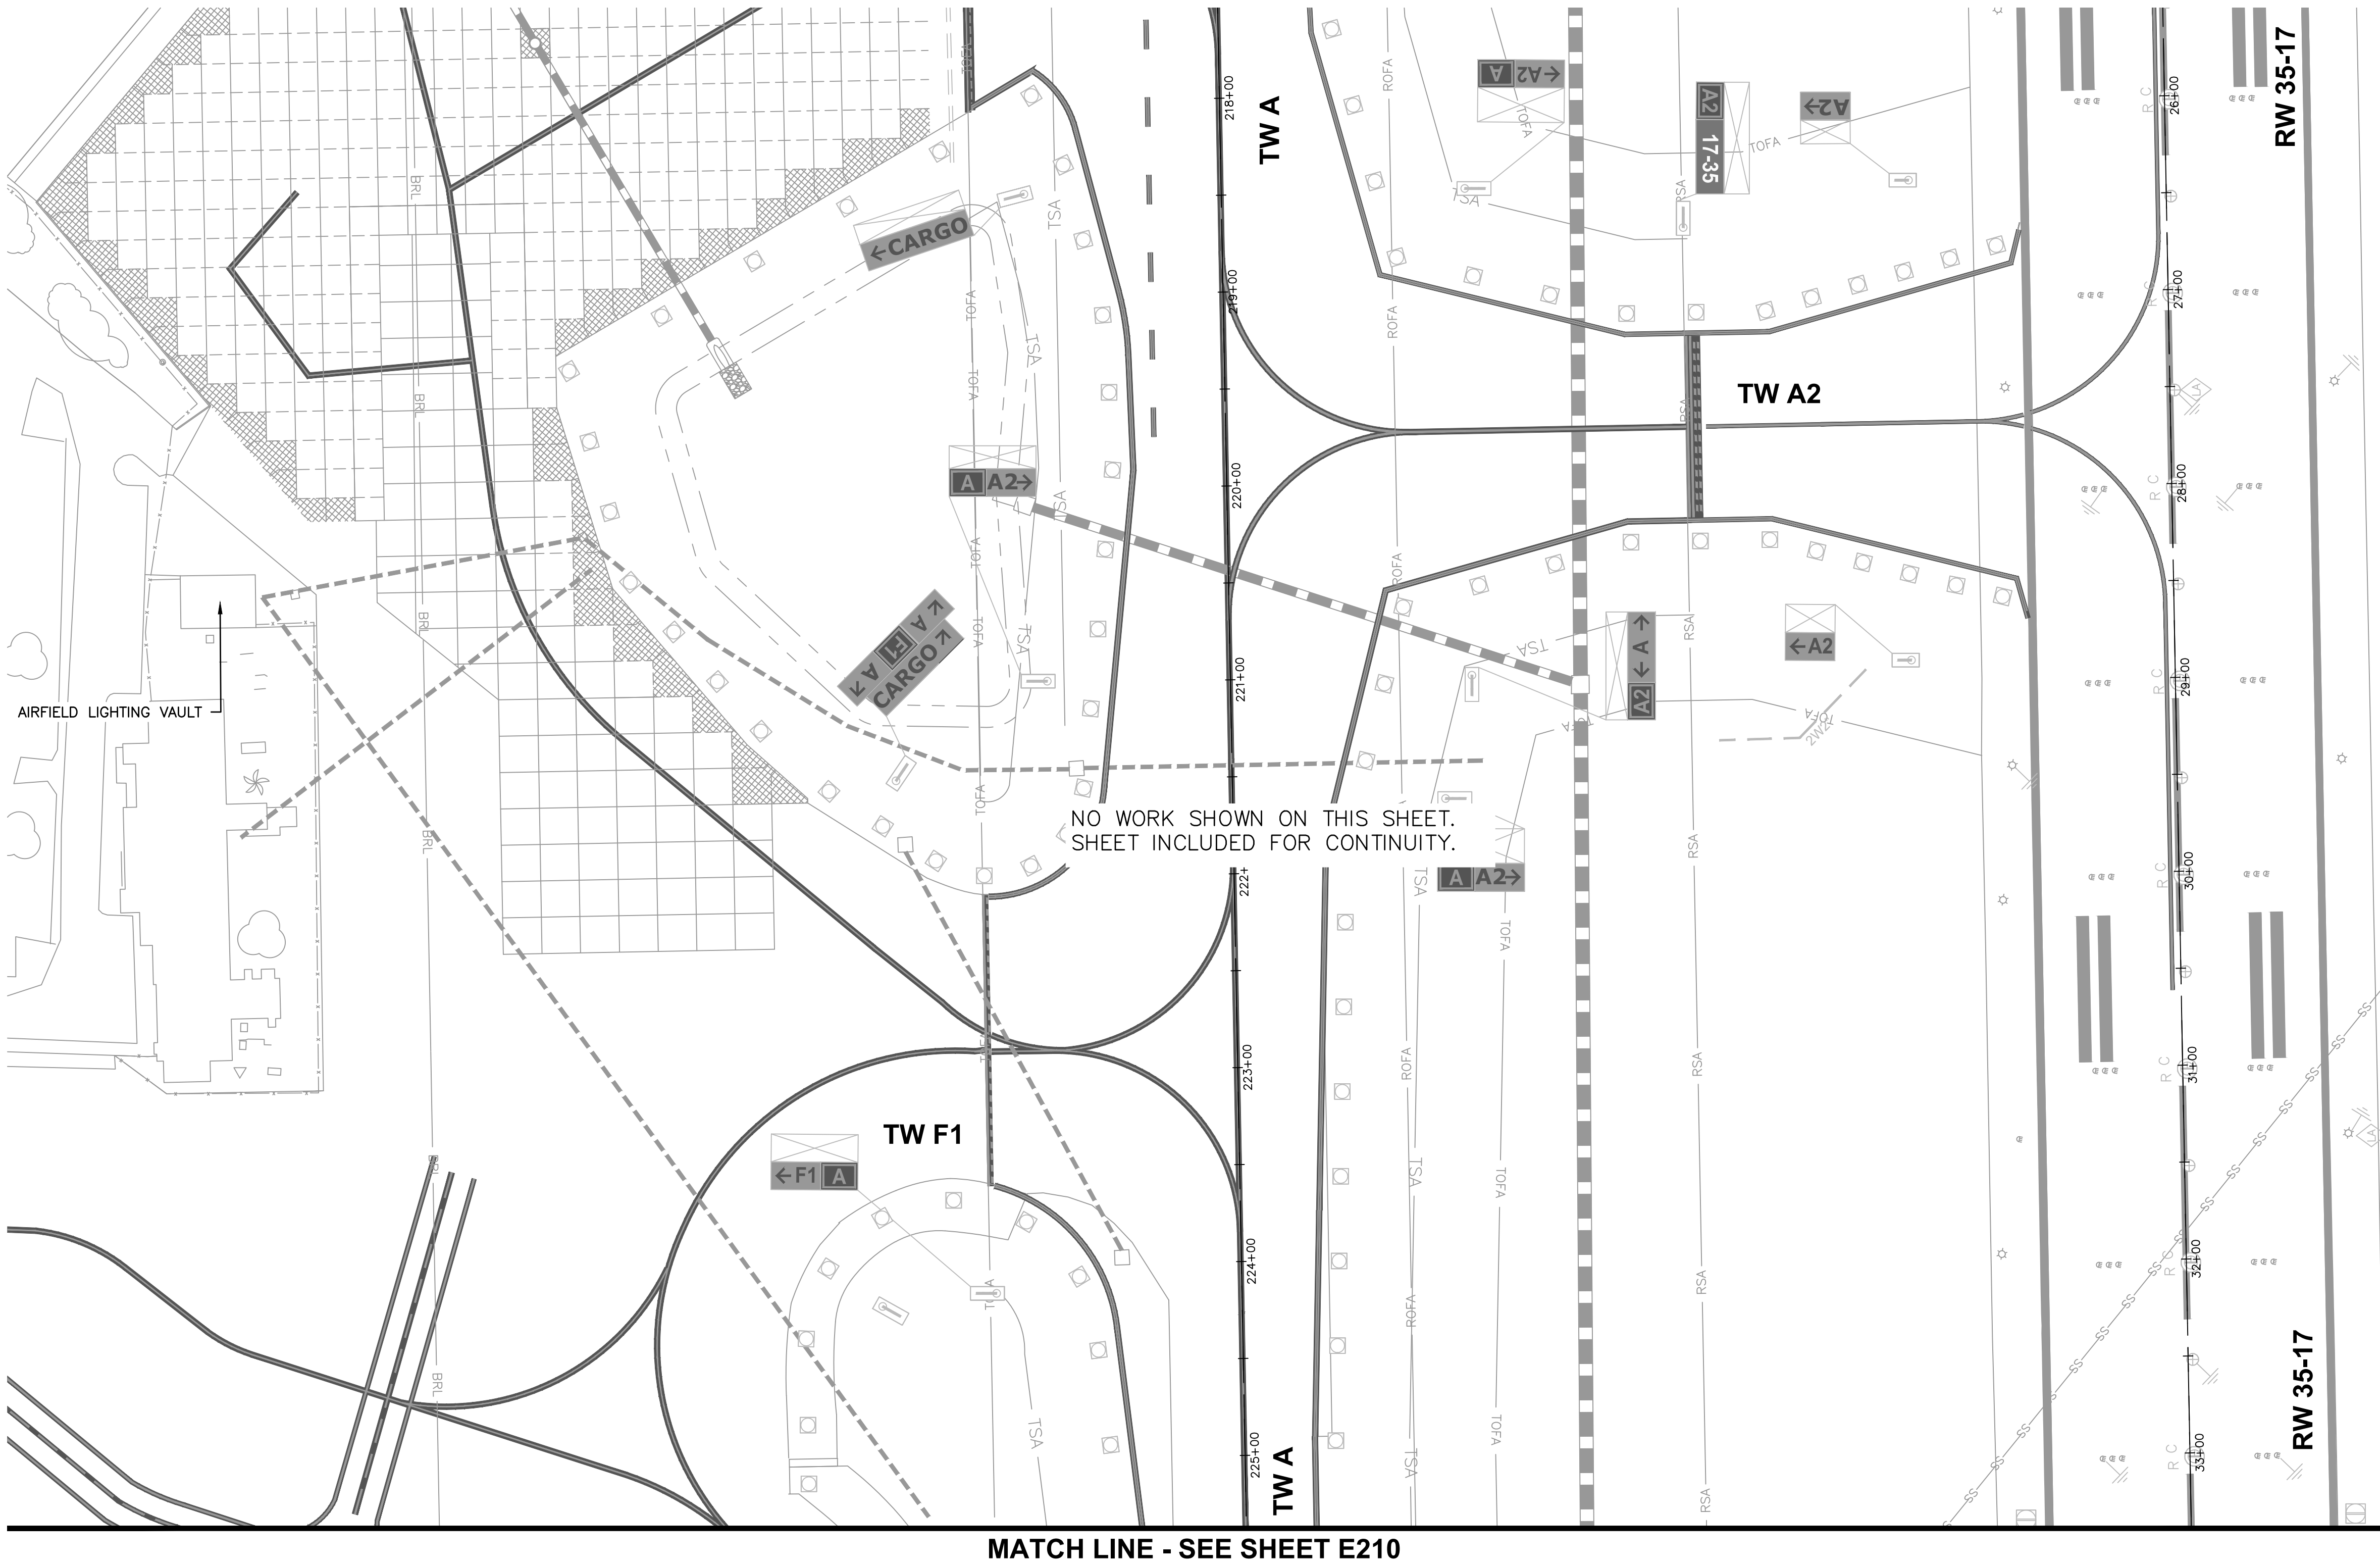

AVCON, INC.

ENGINEERS & PLANNERS

3298 SUMMIT BLVD., SUITE 26

PENSACOLA, FL 32503

OFFICE: (850) 688-3326

CORPORATE CERTIFICATE OF AUTHORIZATION NUMBER: 5057

WWW.AVCONINC.COM

TRANSFORMING TODAY'S IDEAS INTO TOMORROW'S REALITY

SAH

4/25

ADDENDUM 3

NO.

DATE

REVISION

BY

RUNWAY 8-26 REHABILITATION

PREPARED FOR PENSACOLA INTERNATIONAL AIRPORT

DESIGNED BY: SAH

DRAWN BY: KJF

CHECKED BY: MAG

APPROVED BY: VCL

PROJECT NO: 24.0359.01

DATE: MARCH 28, 2025

AIRFIELD LIGHTING LAYOUT PLAN (SHEET 11 OF 11)

ISSUED FOR BID DRAWINGS

E211

SHEET NUMBER