


N:\359 CITY OF PENSACOLA-AIRPORT\2024.0359.01-PNS RUNWAY 8-26\000 CAD\24035901_E301-E311.DWG 4/11/2025 10:22 AM



MATCH LINE - SEE SHEET E302

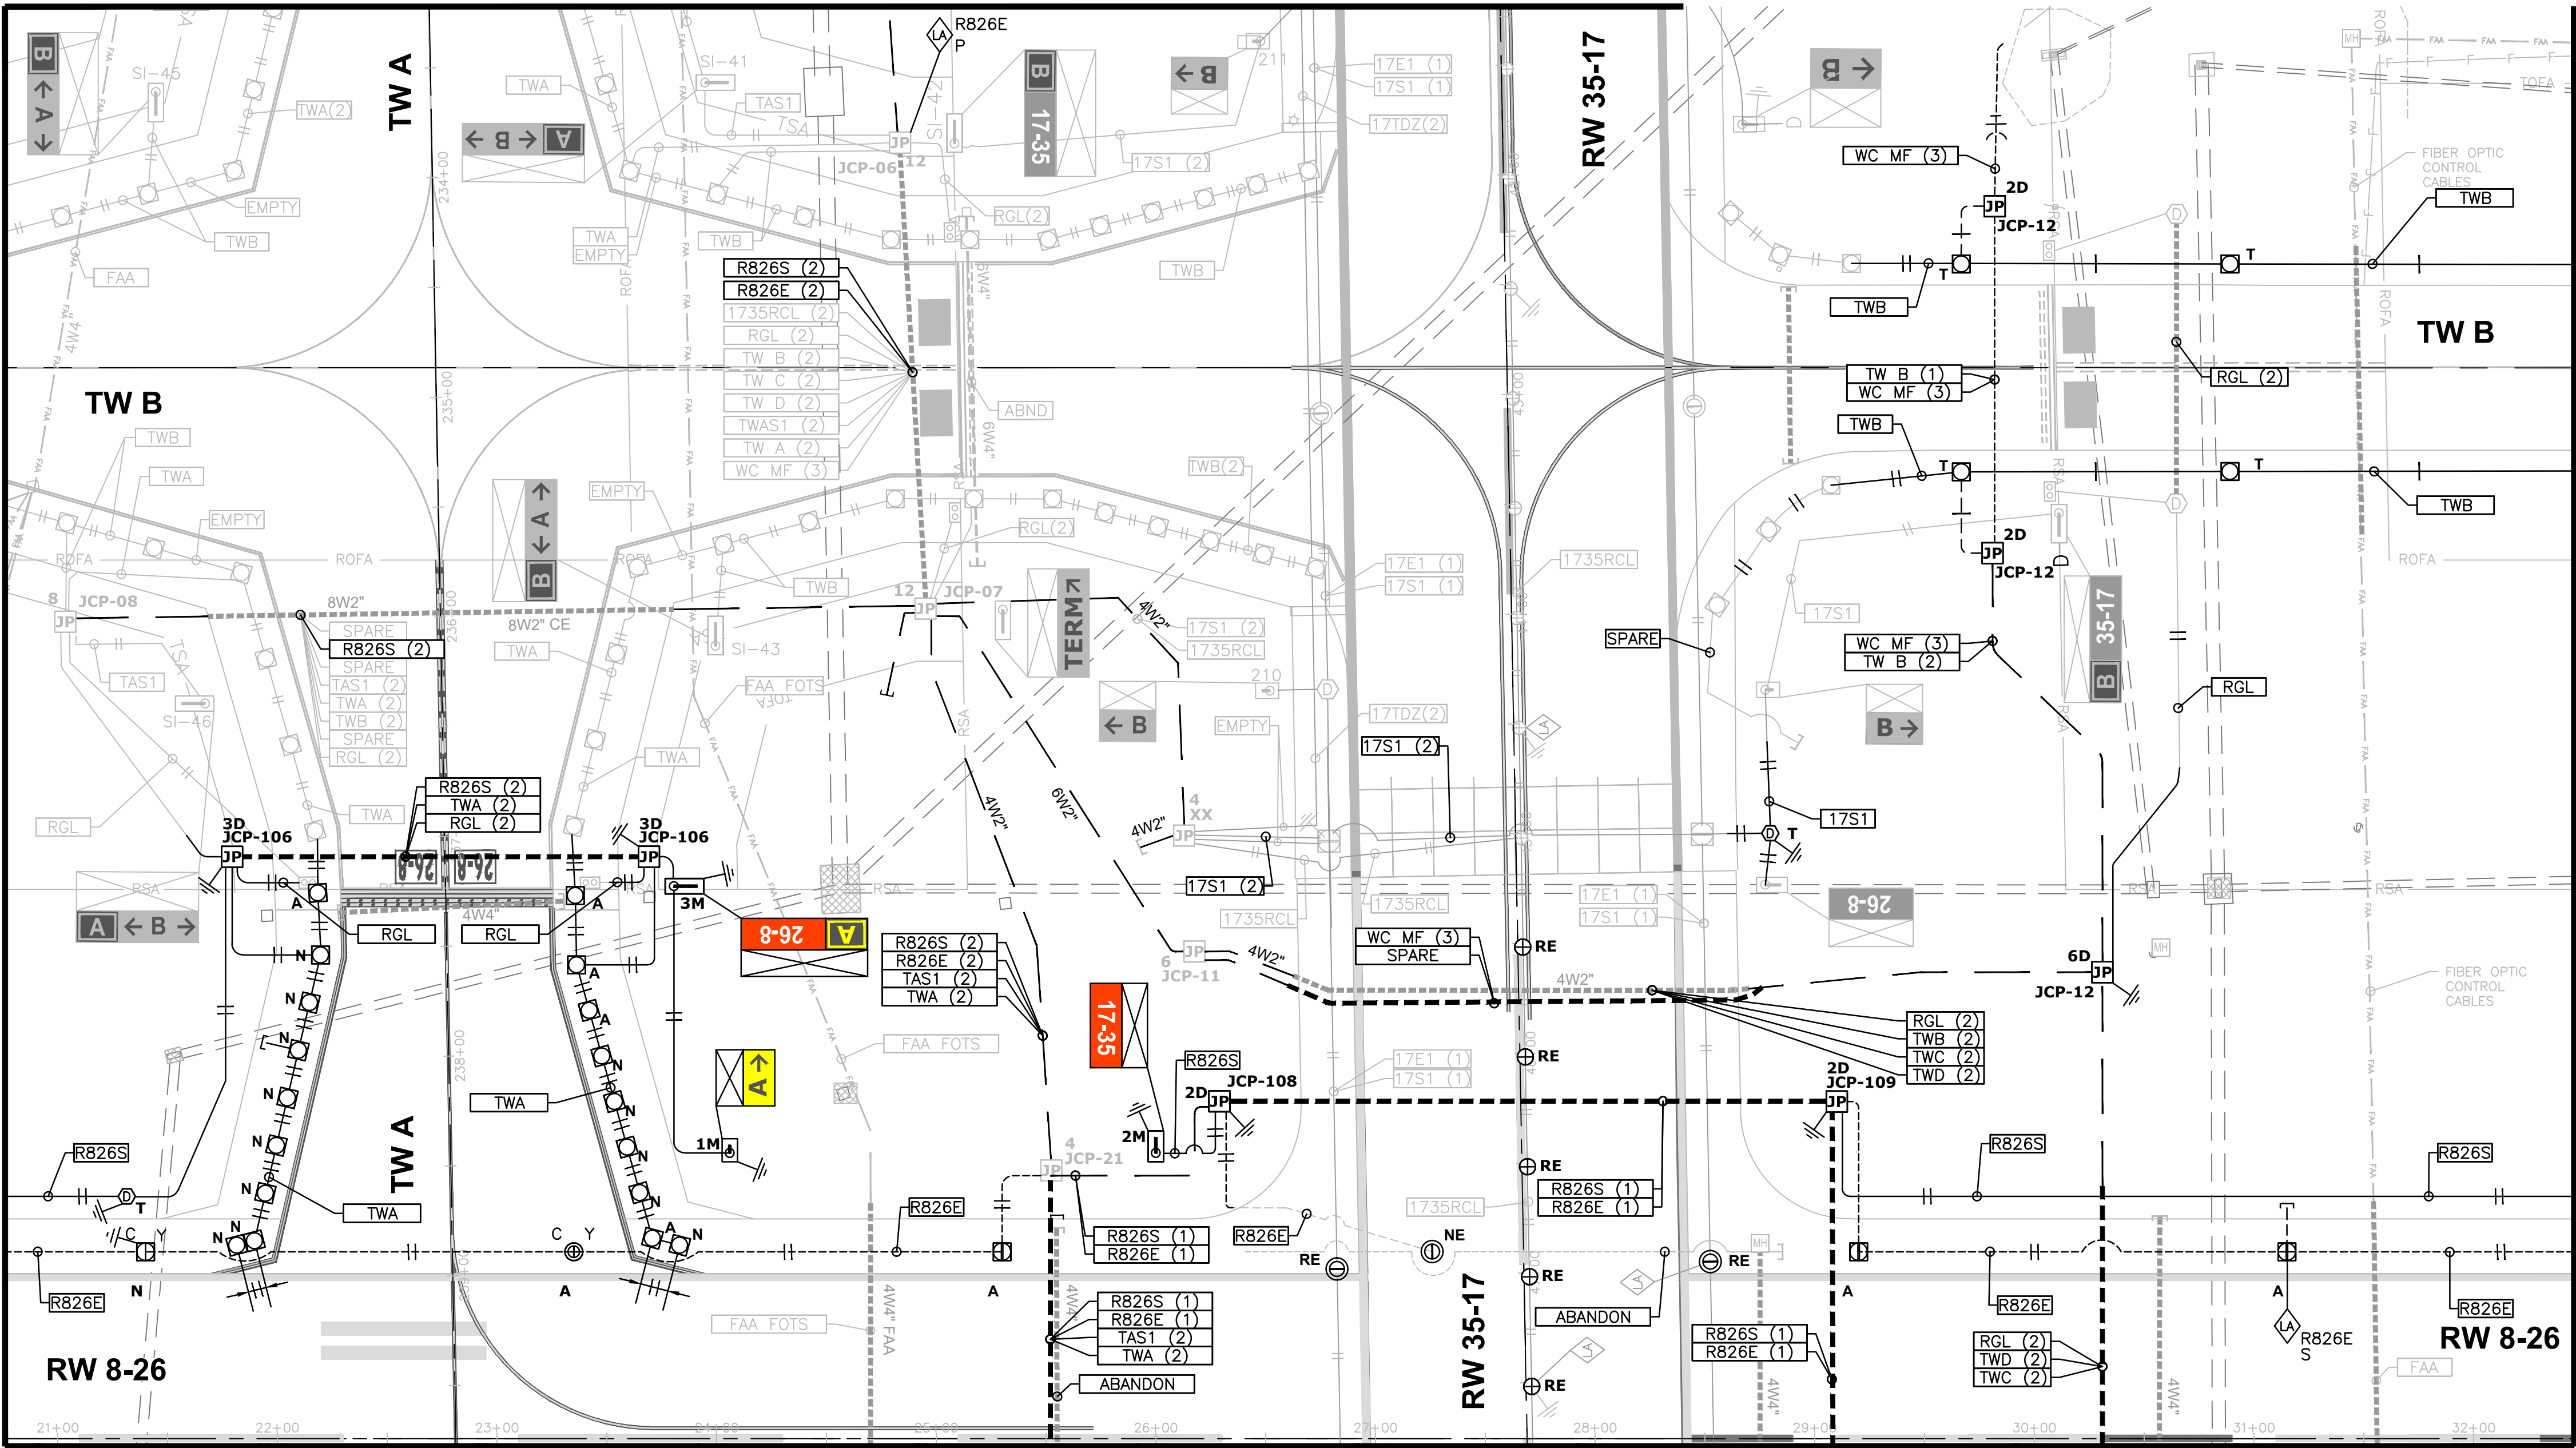

MATCH LINE - SEE SHEET E304

NOTES:

1. SEE SHEET E301 FOR GENERAL CIRCUITING NOTES.

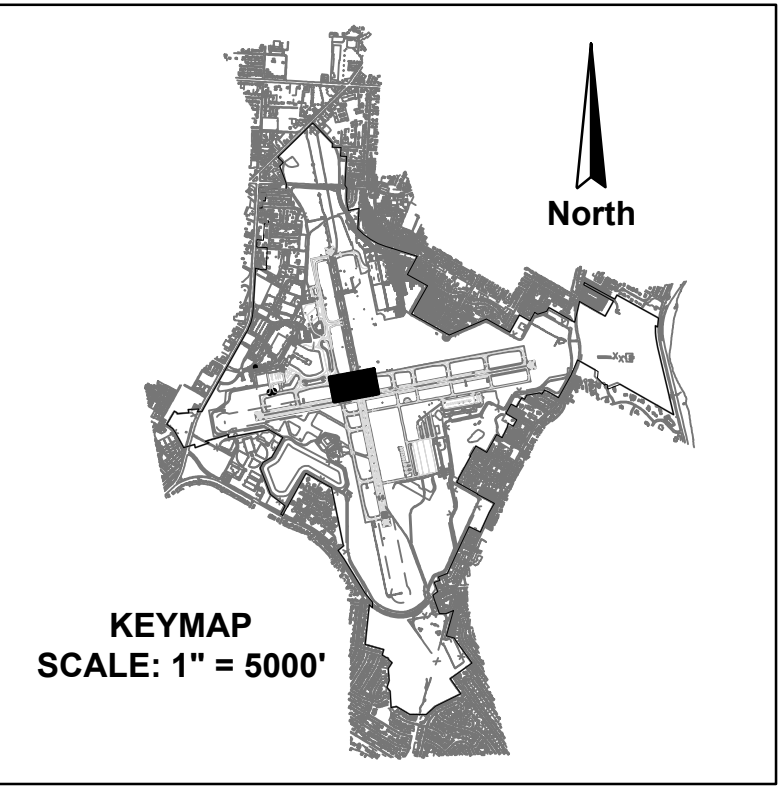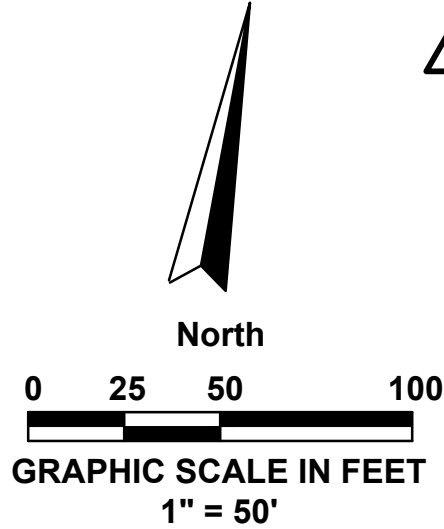

AIRFIELD
LIGHTING
CIRCUITING PLAN
(SHEET 3 OF 11)

RUNWAY 8-26
REHABILITATION
PREPARED FOR
PENSACOLA INTERNATIONAL AIRPORT

DESIGNED BY: SAH
DRAWN BY: KJF
CHECKED BY: MAG
APPROVED BY: VCL
PROJECT NO: 24.0359.01
DATE: MARCH 28, 2025

SHEET NUMBER
E303

AVCON, INC.
ENGINEERS & PLANNERS
3298 SUMMIT BLVD., SUITE 26
PENSACOLA, FL 32503
OFFICE: (850) 688-5526
CORPORATE CERTIFICATE OF
AUTHORIZATION NUMBER: 5057
WWW.AVCONINC.COM

TRANSFORMING TODAY'S IDEAS
INTO TOMORROW'S REALITY

SAH

NO.	DATE	REVISION	BY
1	4/25	ADDENDUM 3	SAH

THIS DOCUMENT CONTAINS PRIVILEGED AND PROPRIETARY INFORMATION, ALL OF WHICH IS EXPRESSLY PROVIDED BY AVCON, INC., FOR USE BY THE INTENDED RECIPIENT, AND FOR A SPECIFIC PURPOSE. WITHOUT THE EXPRESS WRITTEN CONSENT OF AVCON, INC., ANY DISTRIBUTION, REPRODUCTION, OR OTHER USE OF THIS DOCUMENT, IN WHOLE OR IN PART, IS STRICTLY PROHIBITED.