
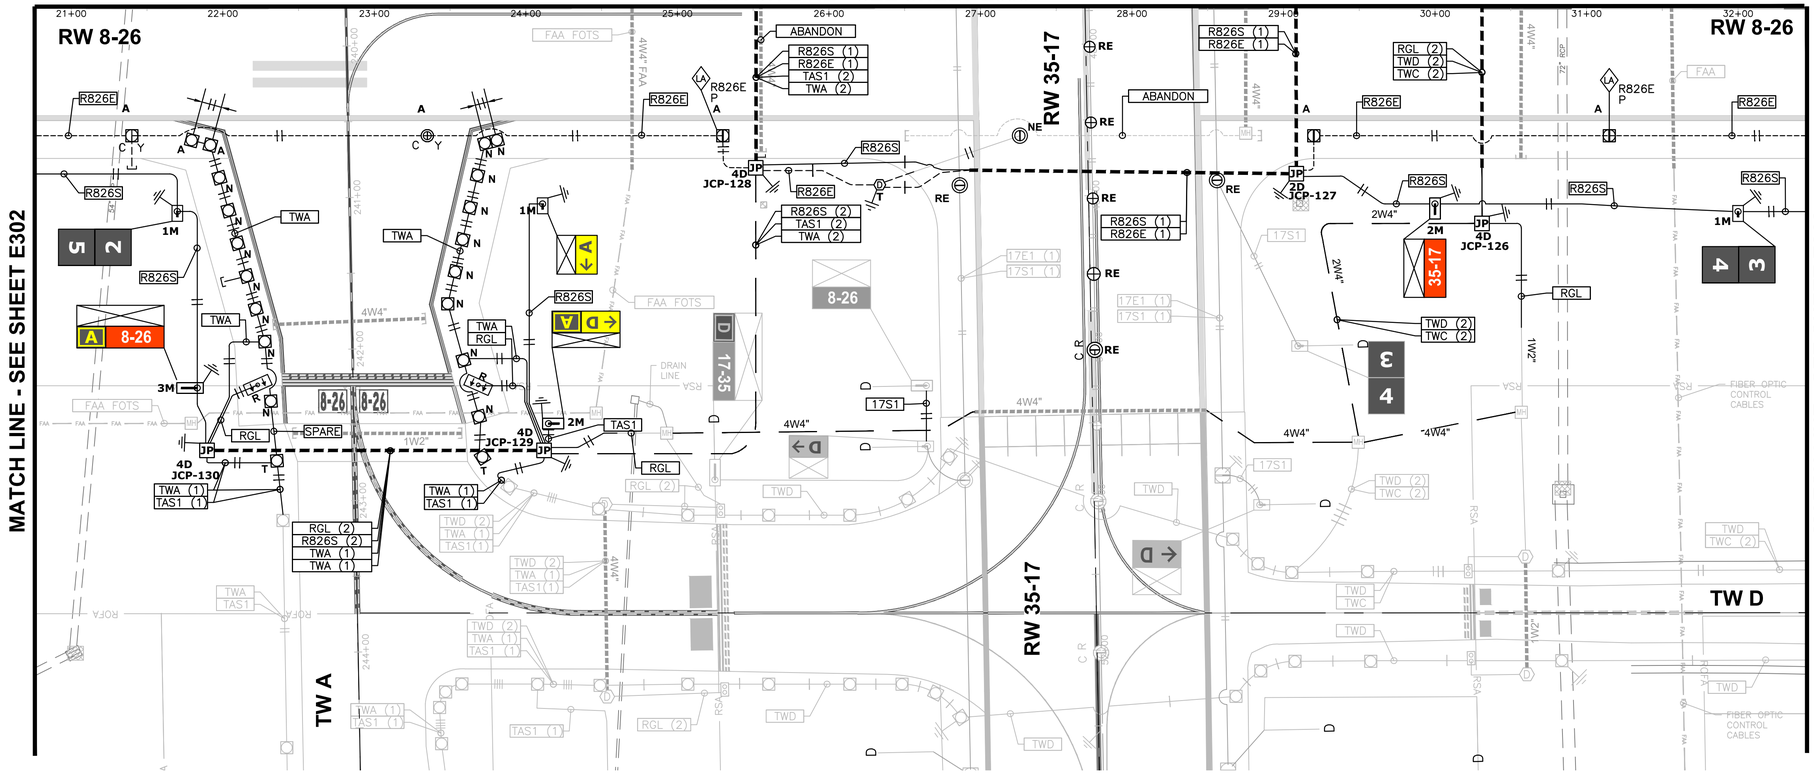


NOTES:

1. SEE SHEET E301 FOR GENERAL CIRCUITING NOTES.

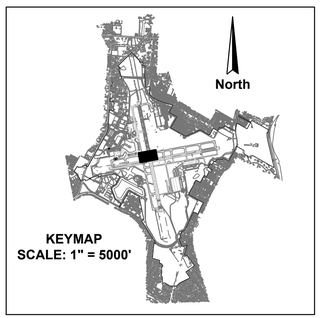

AVCON, INC.
ENGINEERS & PLANNERS
3298 SUMMIT BLVD., SUITE 26
PENSACOLA, FL 32503
OFFICE: (850) 698-3526
CORPORATE CERTIFICATE OF AUTHORIZATION NUMBER: 5057
www.avconinc.com

TRANSFORMING TODAY'S IDEAS INTO TOMORROW'S REALITY

NO.	DATE	REVISION	BY
A	4/25	ADDENDUM 3	SAH

AIRFIELD LIGHTING CIRCUITING PLAN (SHEET 4 OF 11)

ISSUED FOR BID DRAWINGS

RUNWAY 8-26 REHABILITATION

PREPARED FOR
PENSACOLA INTERNATIONAL AIRPORT

DESIGNED BY:	SAH
DRAWN BY:	KJF
CHECKED BY:	MAG
APPROVED BY:	VCL
PROJECT NO:	24.0359.01
DATE:	MARCH 28, 2025

SHEET NUMBER
E304

THIS DOCUMENT CONTAINS PRIVILEGED AND PROPRIETARY INFORMATION, ALL OF WHICH IS EXPRESSLY PROVIDED BY AVCON, INC., FOR USE BY THE INTENDED RECIPIENT, AND FOR A SPECIFIC PURPOSE. WITHOUT THE EXPRESS WRITTEN CONSENT OF AVCON, INC. ANY DISTRIBUTION, REPRODUCTION, OR OTHER USE OF THIS DOCUMENT, IN WHOLE OR IN PART, IS STRICTLY PROHIBITED

N:\359 CITY OF PENSACOLA-AIRPORT\2024.0359.01-PNS RUNWAY 8-26\000 CAD\24035901_E301-E311.DWG 4/11/2025 10:23 AM