




N:\359 CITY OF PENSACOLA-AIRPORT\2024.0359.01-PNS RUNWAY 8-26\000 CAD\24035901_E301-E311.DWG 4/11/2025 10:24 AM

MATCH LINE - SEE SHEET E306

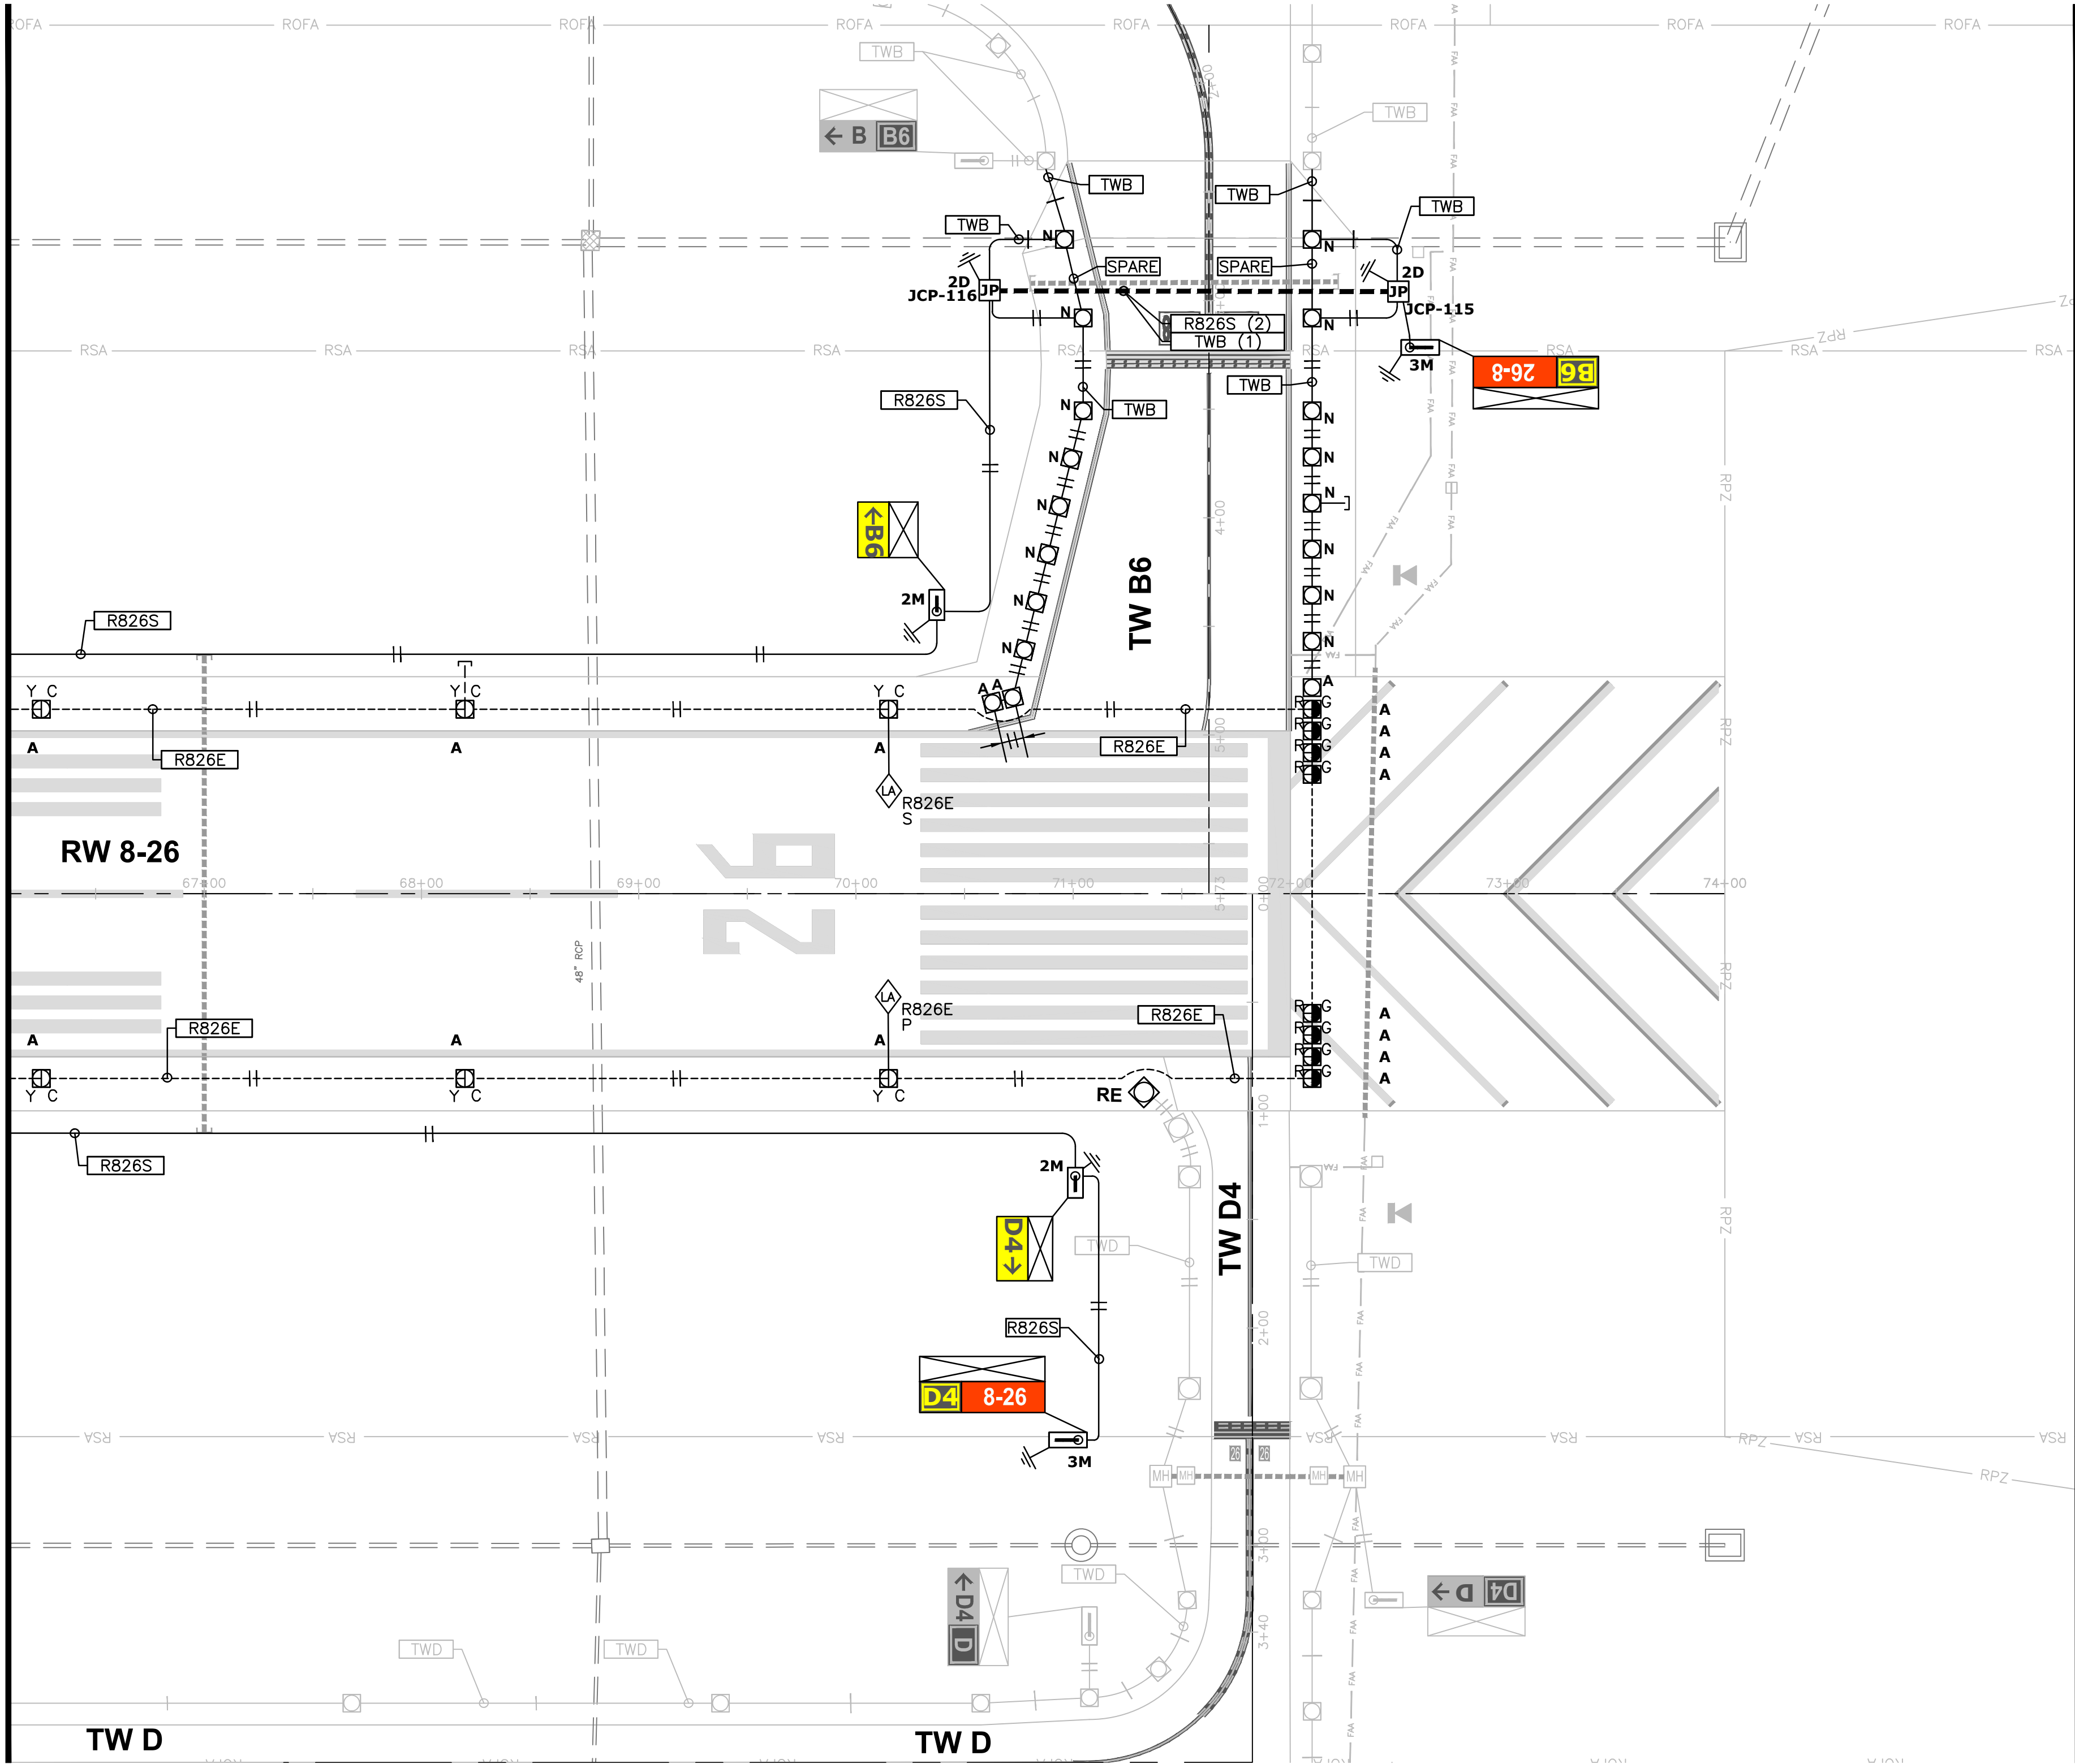

NOTES:

- SEE SHEET E301 FOR GENERAL CIRCUITING NOTES.

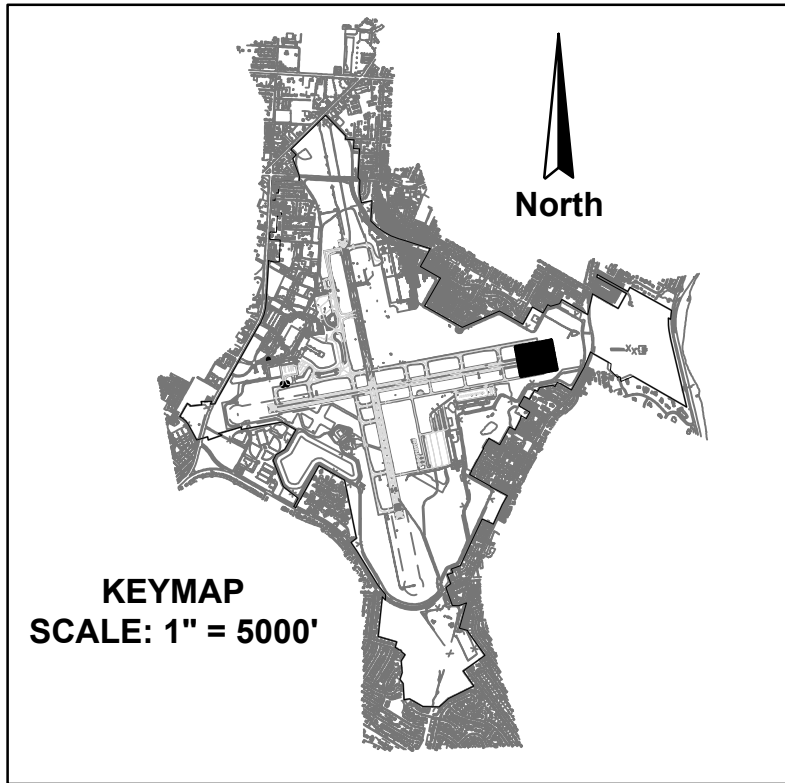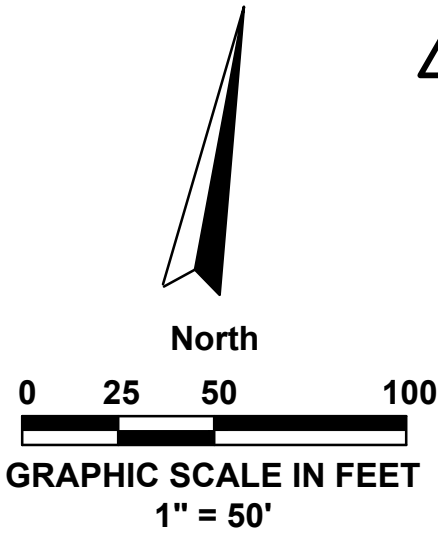

AIRFIELD
LIGHTING
CIRCUITING PLAN
(SHEET 9 OF 11)
ISSUED FOR BID DRAWINGS

RUNWAY 8-26
REHABILITATION
PREPARED FOR
PENSACOLA INTERNATIONAL AIRPORT

DESIGNED BY: SAH
DRAWN BY: KJF
CHECKED BY: MAG
APPROVED BY: VCL
PROJECT NO: 24.0359.01
DATE: MARCH 28, 2025

SHEET NUMBER
E309

TRANSFORMING TODAY'S IDEAS
INTO TOMORROW'S REALITY

SAH

NO.	DATE	REVISION	BY
1	4/25	ADDENDUM 3	SAH

4/25

3

SAH

AVCON, INC.
ENGINEERS & PLANNERS
3298 SUMMIT BLVD., SUITE 26
PENSACOLA, FL 32503
OFFICE: (850) 688-5526
CORPORATE CERTIFICATE OF
AUTHORIZATION NUMBER: 5057
WWW.AVCONINC.COM