


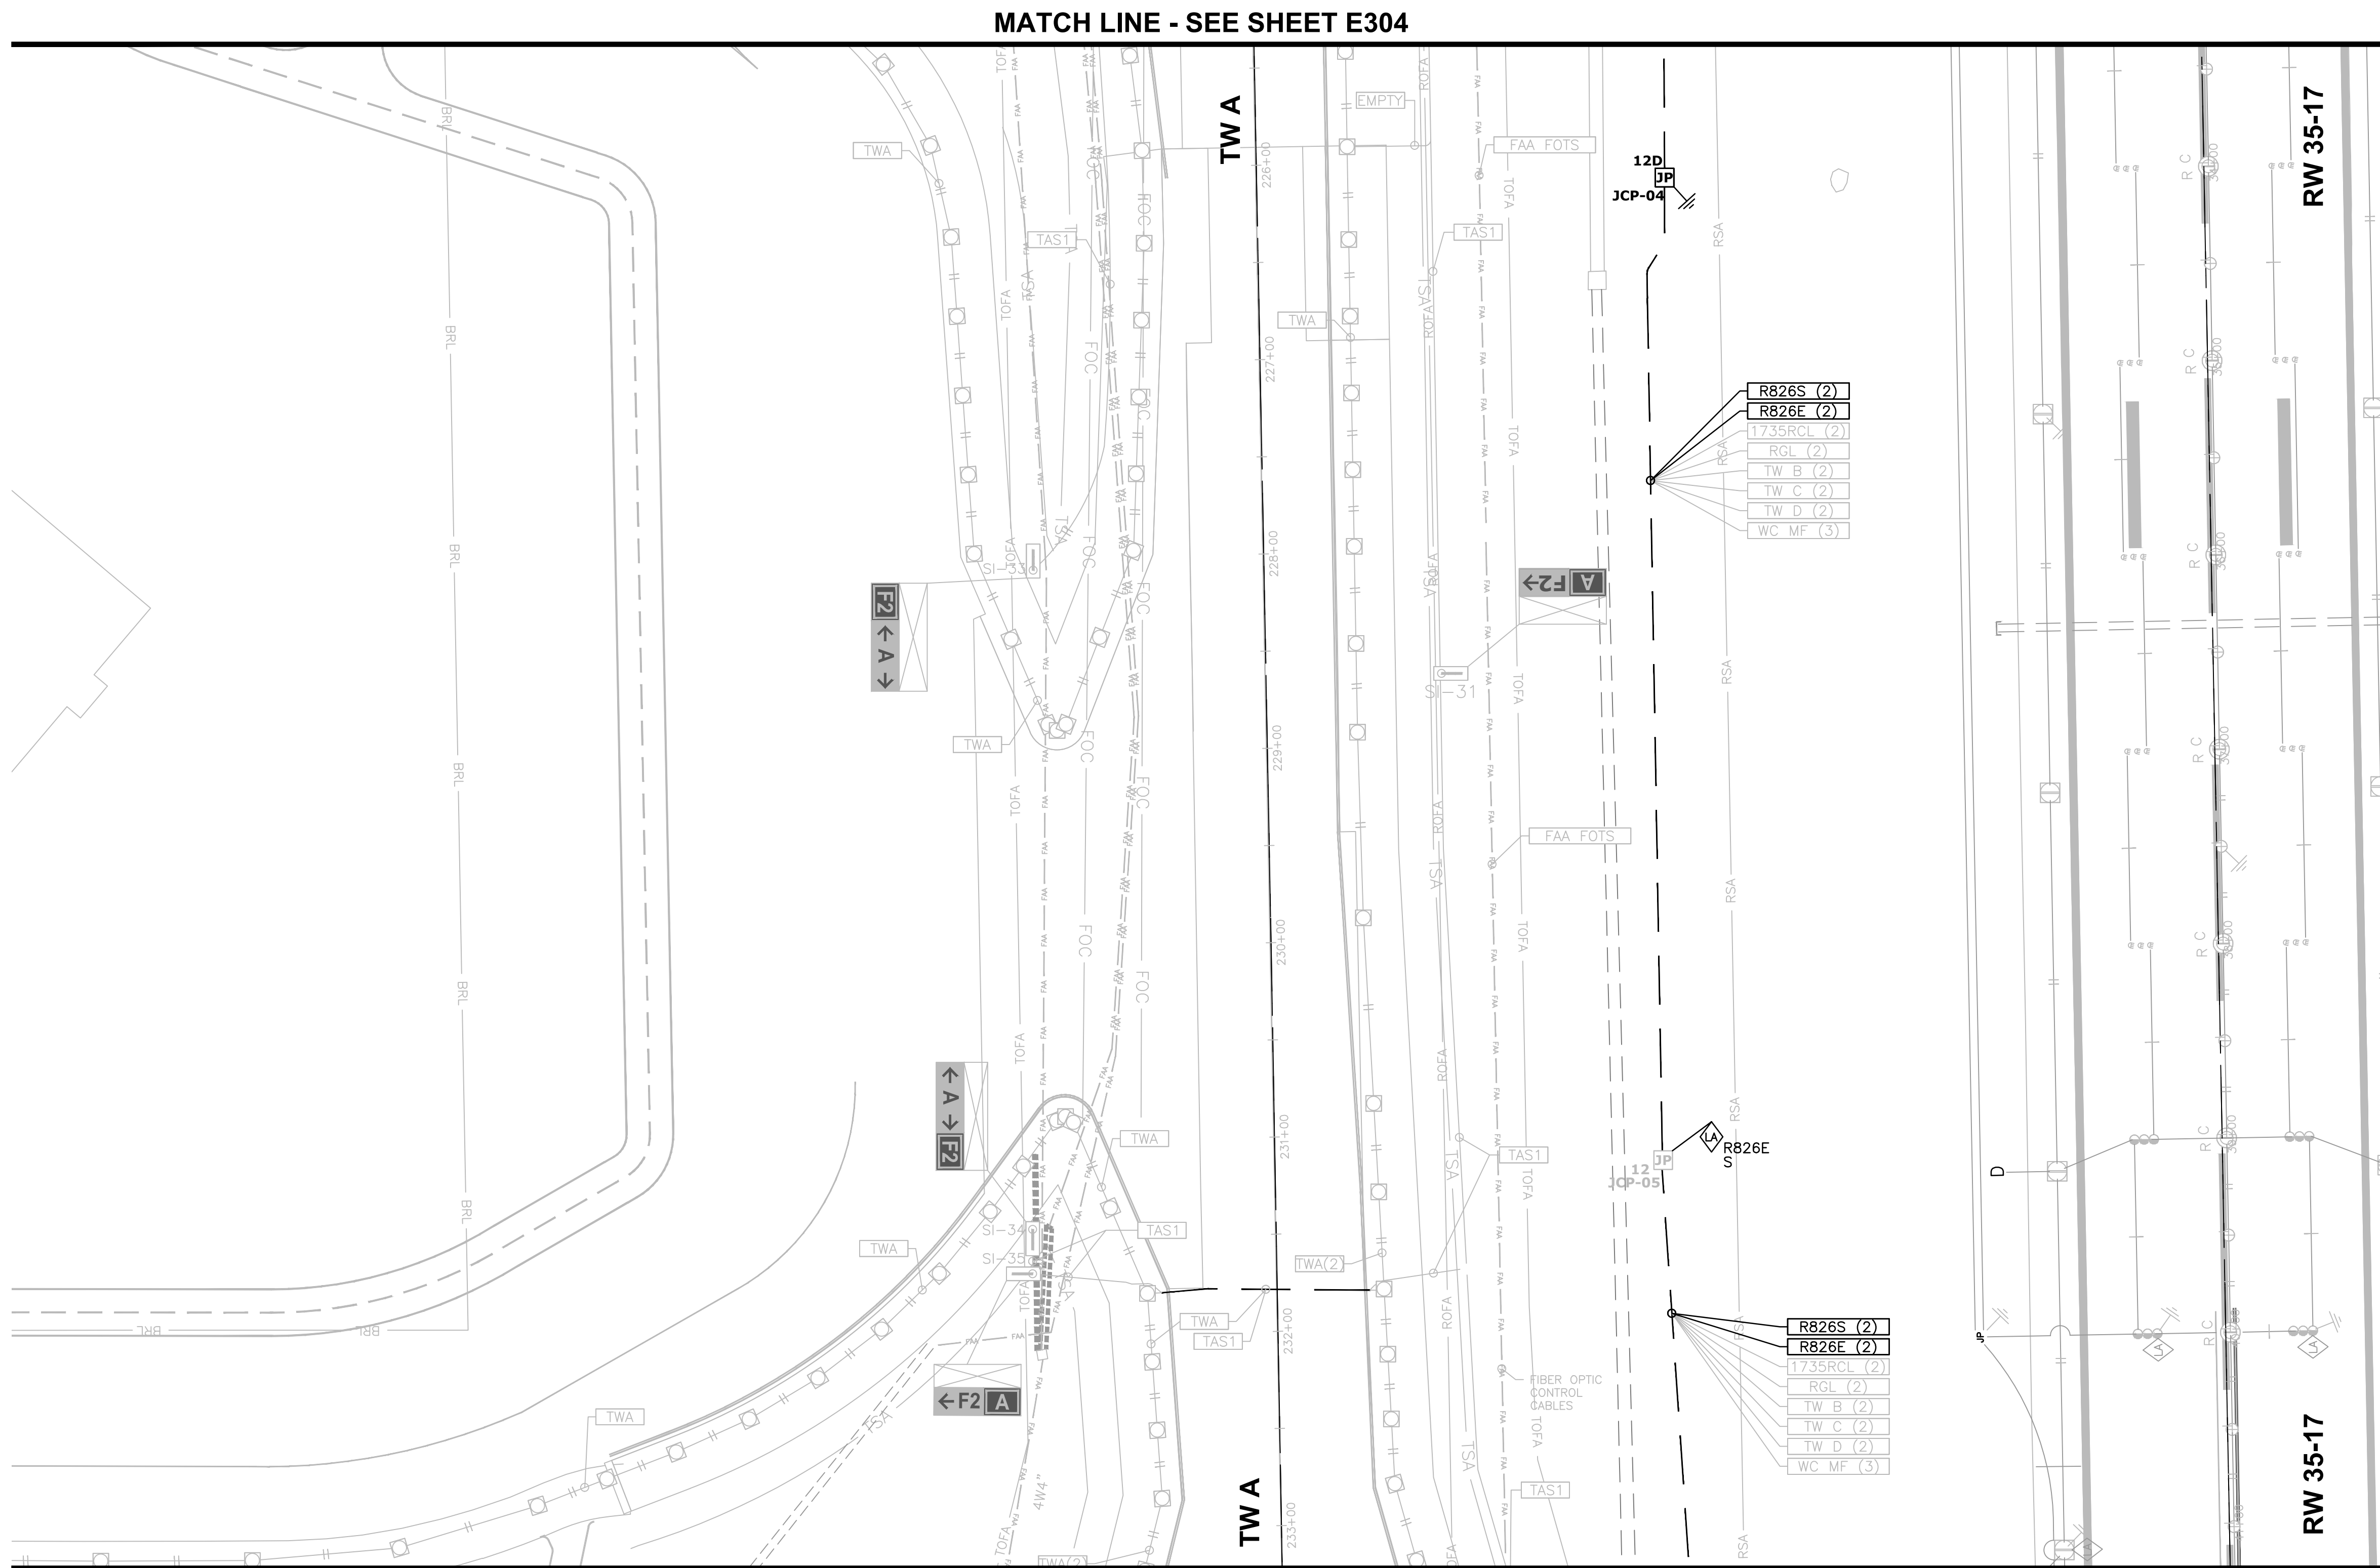

NOTES:

1. SEE SHEET E301 FOR GENERAL CIRCUITING NOTES.

MATCH LINE - SEE SHEET E304

MATCH LINE - SEE SHEET E304

TW A

TW A

12D
JCP-04



12
CP-05

R826S (2)
R826E (2)
1735RCL (2)
RGL (2)
TW B (2)
TW C (2)
TW D (2)
WC MF (3)

R826S (2)
R826E (2)
1735RCL (2)
RGL (2)
TW B (2)
TW C (2)
TW D (2)
WC MF (3)

RW 35-17

RW 35-17

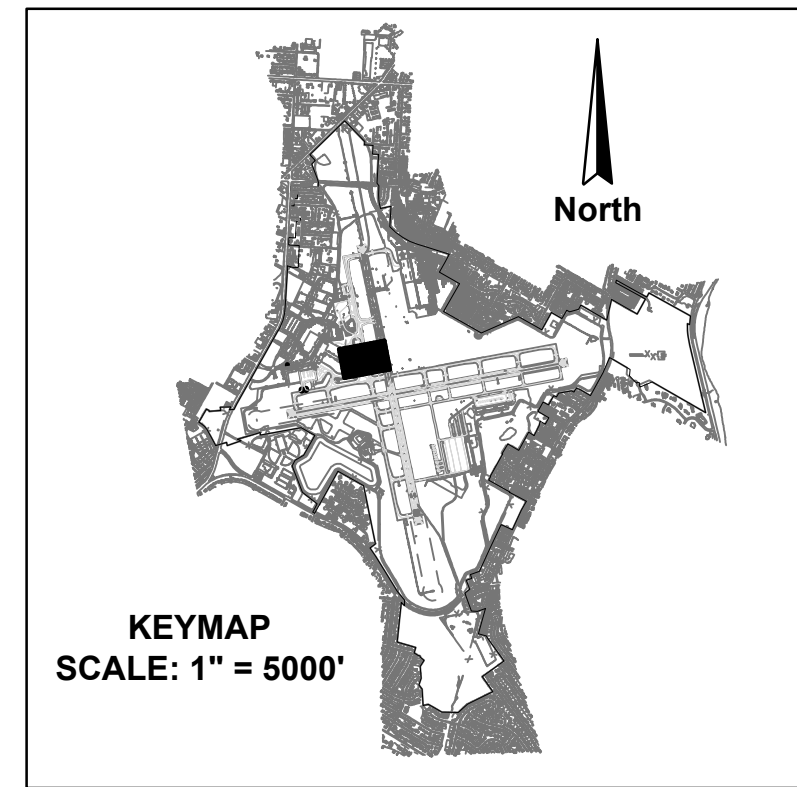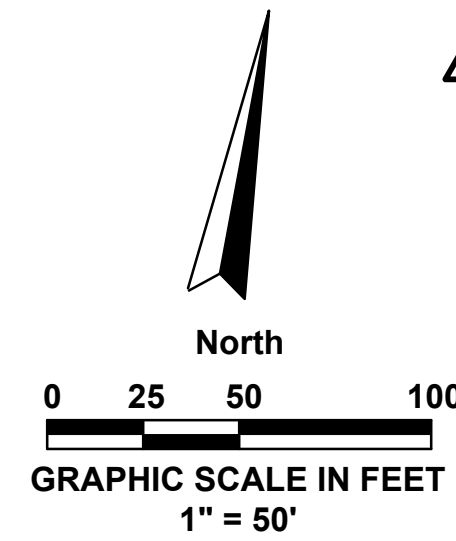

AVCON, INC.
ENGINEERS & PLANNERS

3298 SUMMIT BLVD., SUITE 26
PENSACOLA, FL 32503
OFFICE: (850) 698-3526
CORPORATE CERTIFICATE OF
AUTHORIZATION NUMBER: 5057
www.avconinc.com

**TRANSFORMING TODAY'S IDEAS
INTO TOMORROW'S REALITY**

1.	4/25	ADDENDUM 3	SAH
△			
△			
△			
△			
△			
△			
△			
△			
NO.	DATE	REVISION	BY

**AIRFIELD
LIGHTING
CIRCUITING PLAN
(SHEET 10 OF 11)**

**RUNWAY 8-26
REHABILITATION**

**PREPARED FOR
PENSACOLA INTERNATIONAL AIRPORT**

DESIGNED BY:	SAH
DRAWN BY:	KJF
CHECKED BY:	MAG
APPROVED BY:	VCL
PROJECT NO:	24.0359.01
DATE:	MARCH 28, 2025

SHEET NUMBER
E310

THIS DOCUMENT CONTAINS PRIVILEGED AND PROPRIETARY INFORMATION, ALL OF WHICH IS EXPRESSLY PROVIDED BY AVCON, INC. FOR USE BY THE INTENDED RECIPIENT, AND FOR A SPECIFIC PURPOSE. WITHOUT THE EXPRESS WRITTEN CONSENT OF AVCON, INC. ANY DISTRIBUTION, REPRODUCTION OR OTHER USE OF THIS DOCUMENT, IN WHOLE OR IN PART, IS STRICTLY PROHIBITED.