


N:\359 CITY OF PENSACOLA-AIRPORT\2024.0359.01-PNS RUNWAY 8-26\000 CAD\24035901_E101-111.DWG 4/11/2025 11:17 AM

MATCH LINE - SEE SHEET E108

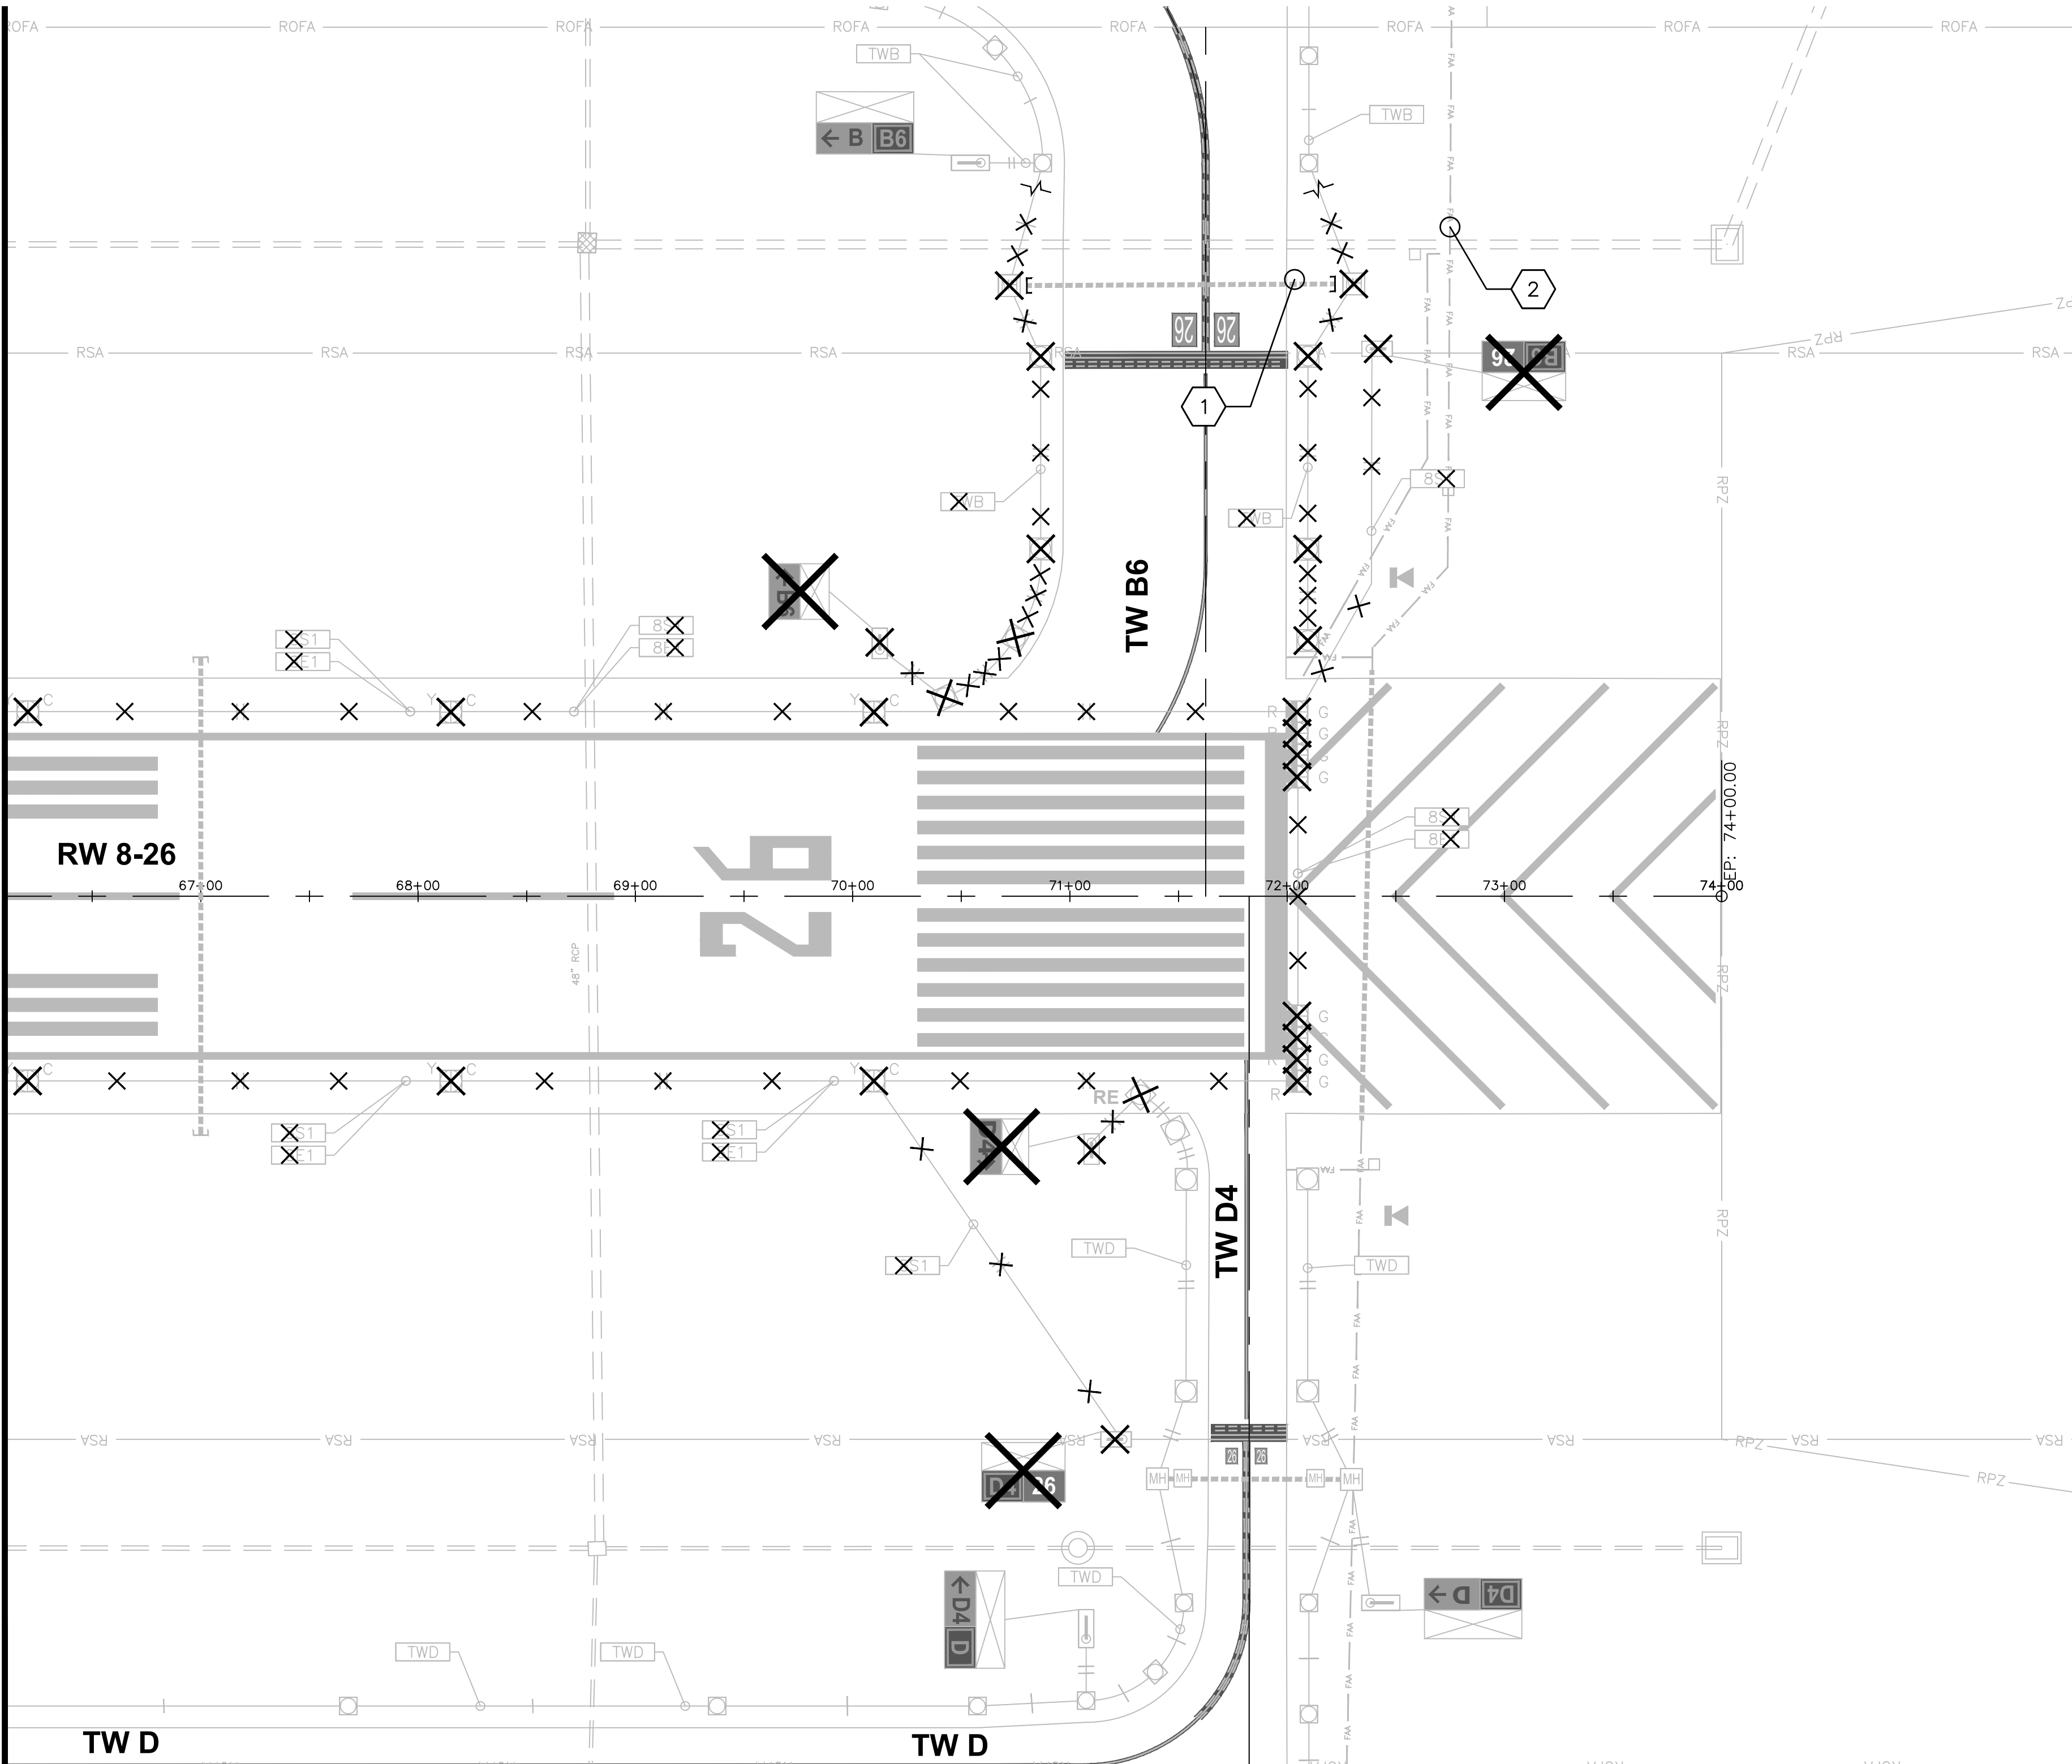

NOTES:


1. SEE SHEET E101 FOR GENERAL DEMOLITION NOTES.
2. SEE SHEETS E001 THRU E003 FOR ELECTRICAL NOTES, LEGEND AND ABBREVIATIONS.

KEYNOTES:



- 1 PRESERVE AND PROTECT ALL FAA CABLES AND CONDUITS IN AREA. (TYP.)
- 2 PRESERVE AND PROTECT ALL FAA CABLES AND CONDUITS IN AREA. (TYP.)



EXISTING RUNWAY
EXIT SIGN

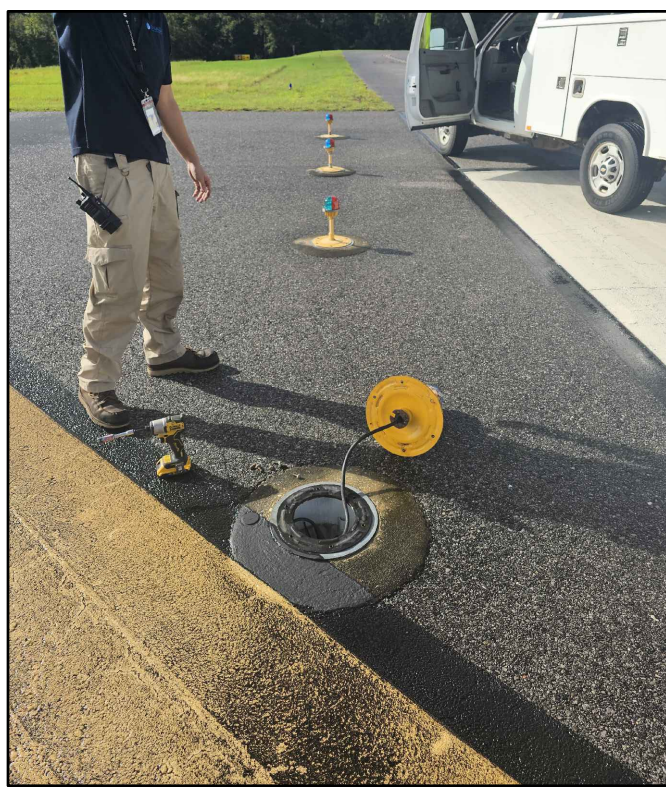

EXISTING RUNWAY 26
THRESHOLD

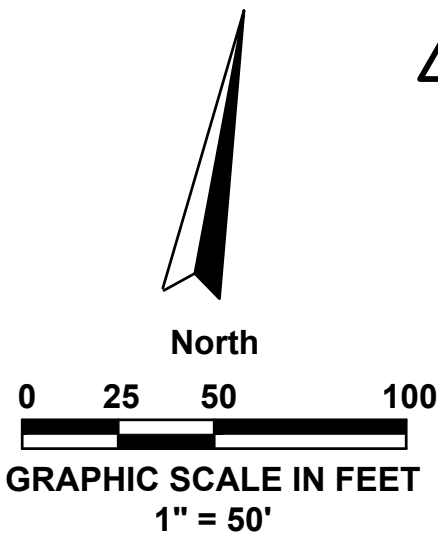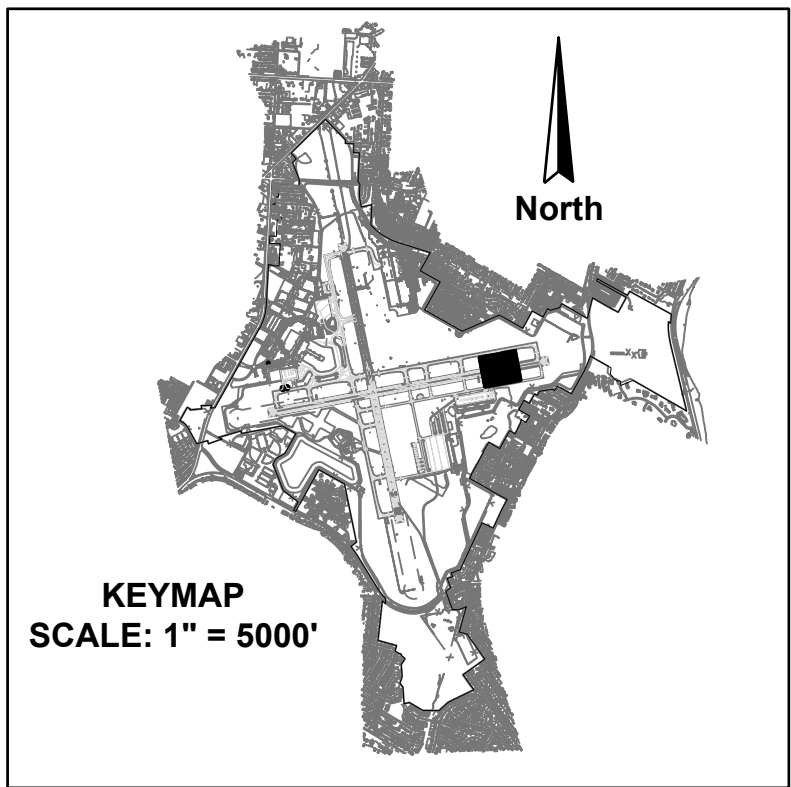

EXISTING
CONDITIONS AND
DEMOLITION PLAN
(SHEET 9 OF 11)
ISSUED FOR BID DRAWINGS

RUNWAY 8-26
REHABILITATION
PREPARED FOR
PENSACOLA INTERNATIONAL AIRPORT

DESIGNED BY: SAH
DRAWN BY: KJF
CHECKED BY: MAG
APPROVED BY: VCL
PROJECT NO: 24.0359.01
DATE: MARCH 28, 2025


SHEET NUMBER
E109

AVCON, INC.
ENGINEERS & PLANNERS
3298 SUMMIT BLVD., SUITE 26
PENSACOLA, FL 32503
OFFICE: (850) 688-3326
CORPORATE CERTIFICATE OF
AUTHORIZATION NUMBER: 5057
WWW.AVCONINC.COM

NO.	DATE	REVISION	BY
1	4/25	ADDENDUM 3	SAH
2			
3			
4			
5			
6			
7			
8			
9			
10			

TRANSFORMING TODAY'S IDEAS
INTO TOMORROW'S REALITY
THIS DOCUMENT CONTAINS PRIVILEGED AND PROPRIETARY INFORMATION. ALL OF WHICH IS EXPRESSLY PROVIDED BY AVCON, INC., FOR USE BY THE INTENDED RECIPIENT, AND FOR A SPECIFIC PURPOSE. WITHOUT THE EXPRESS WRITTEN CONSENT OF AVCON, INC., ANY DISTRIBUTION, REPRODUCTION, OR OTHER USE OF THIS DOCUMENT, IN WHOLE OR IN PART, IS STRICTLY PROHIBITED.

N:\359 CITY OF PENSACOLA-AIRPORT\2024-0359.01-PNS RUNWAY 8-26\000 CAD\24035901_E101-111.DWG 4/11/2025 11:17 AM


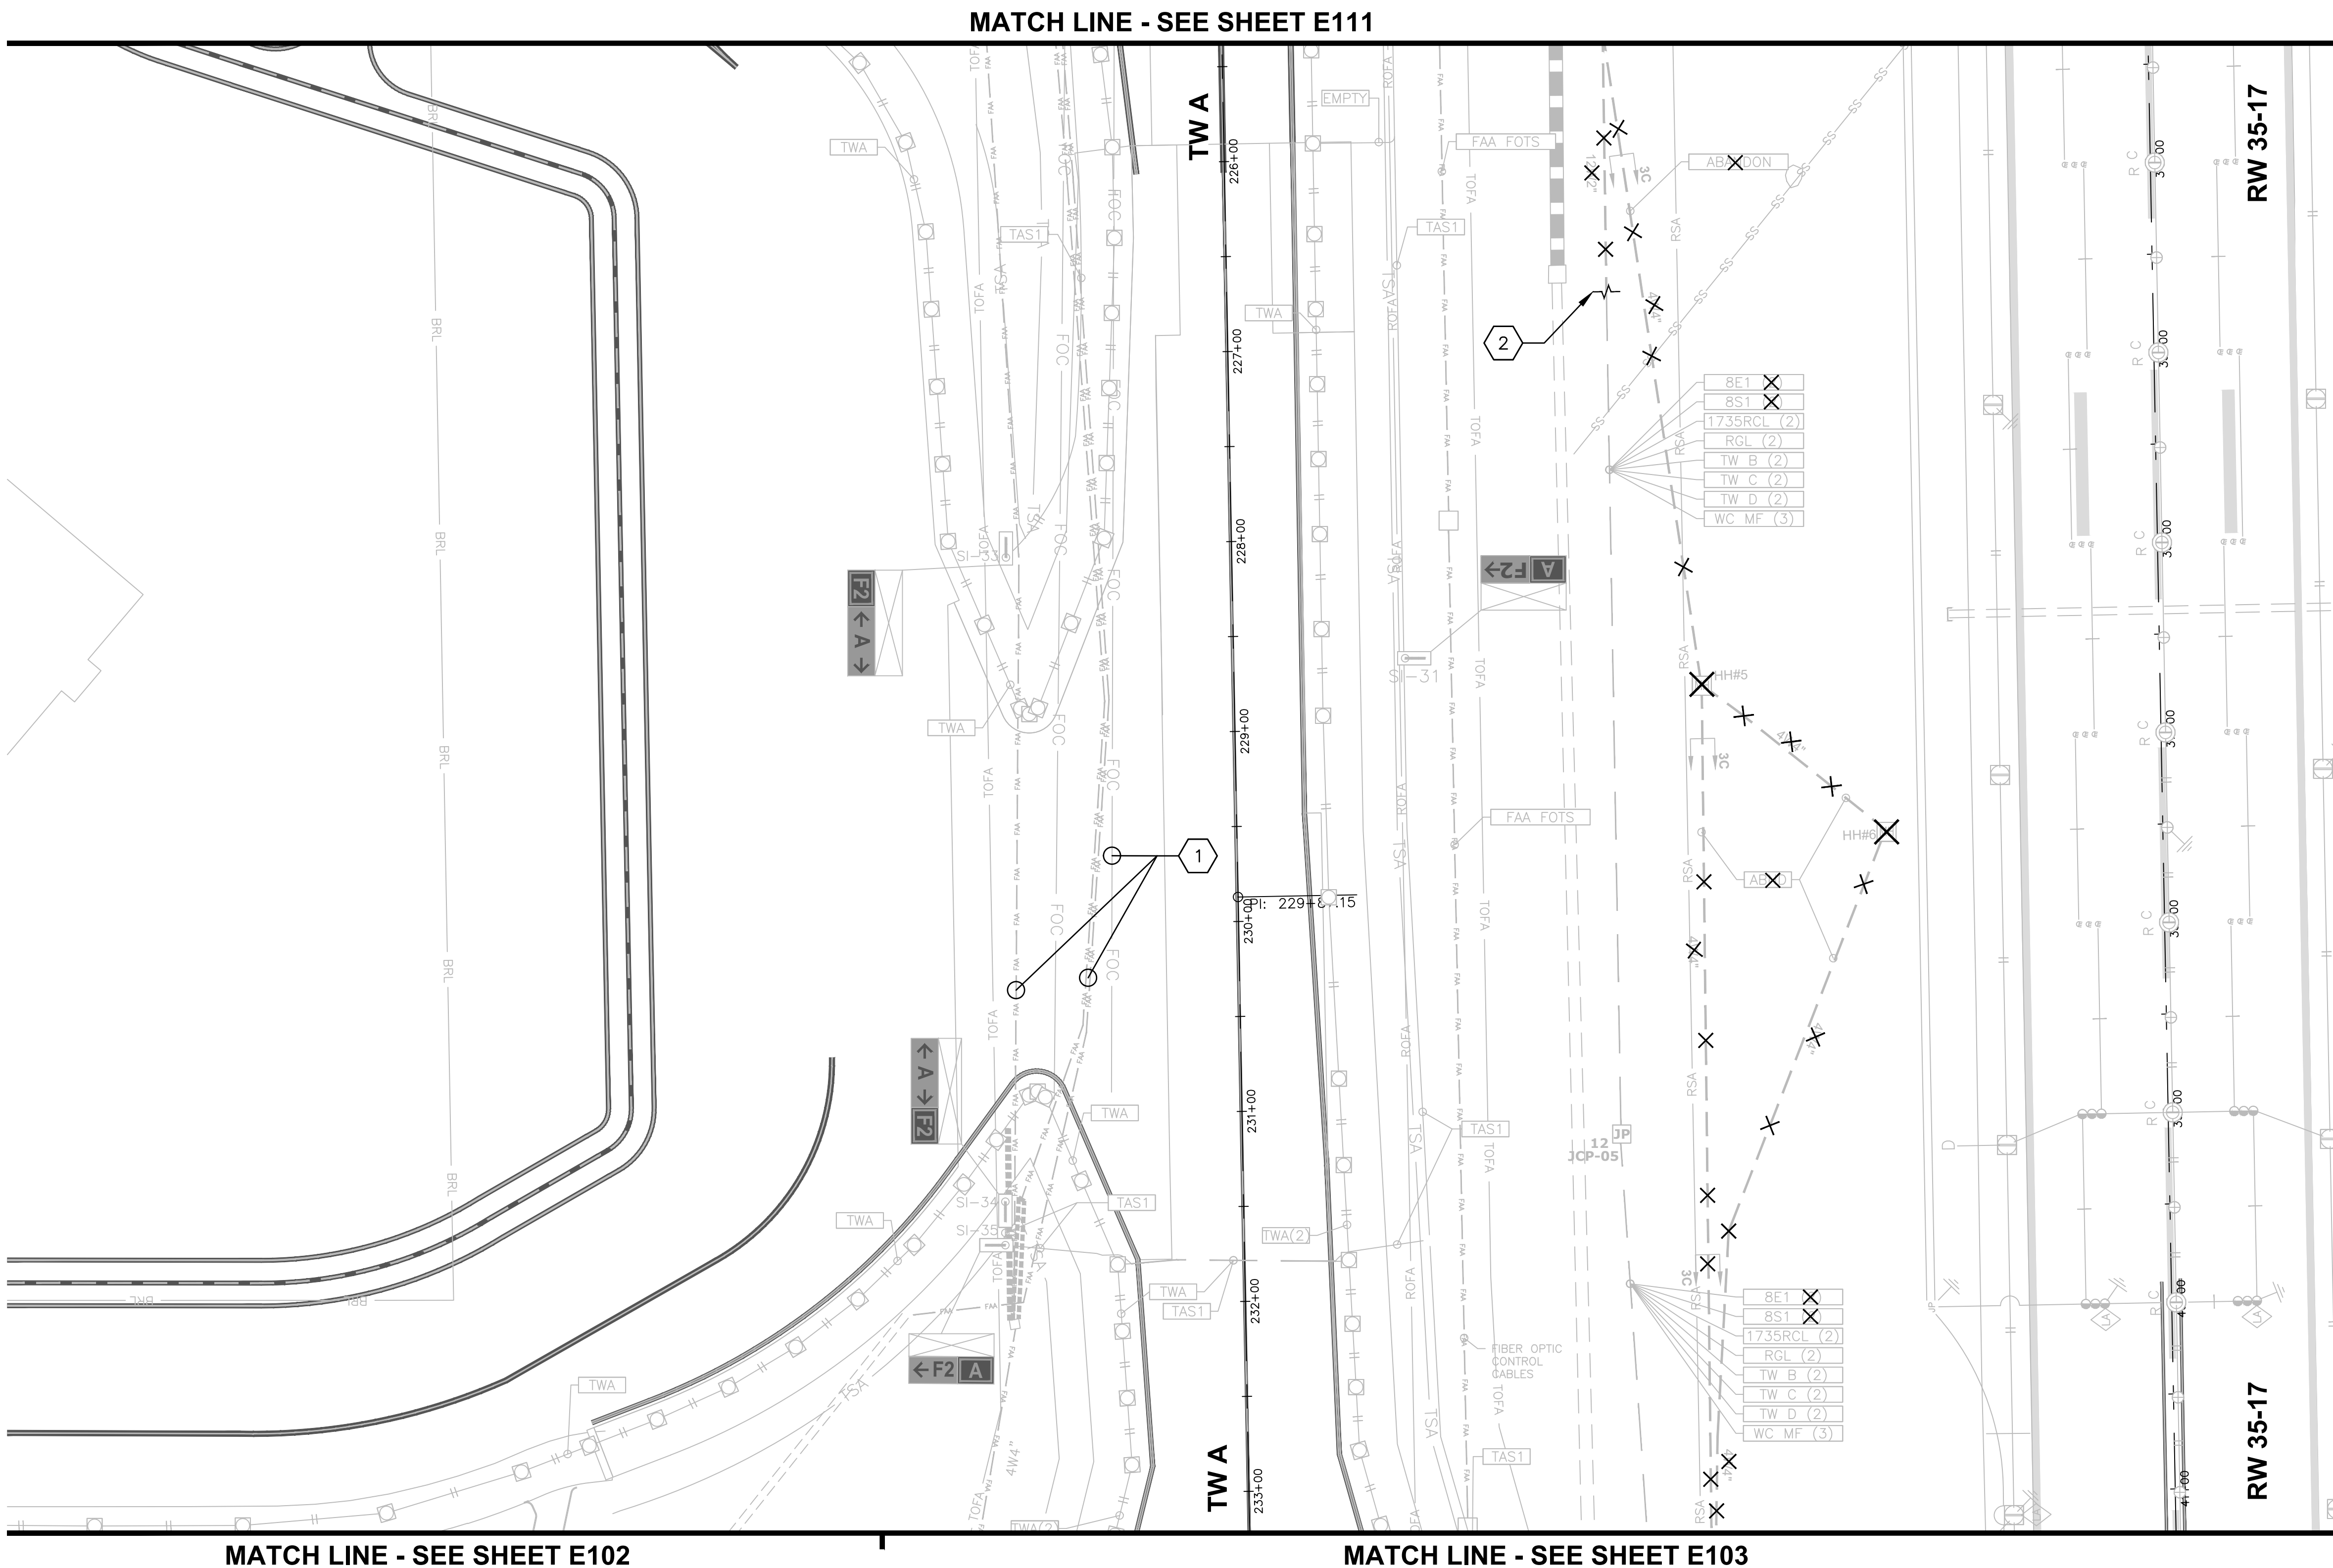


NOTES:

- SEE SHEET E101 FOR GENERAL DEMOLITION NOTES.
- SEE SHEETS E001 THRU E003 FOR ELECTRICAL NOTES, LEGEND AND ABBREVIATIONS.

KEYNOTES:

- PRESERVE AND PROTECT ALL FAA AND FIBER OPTIC CABLES AND CONDUITS IN AREA. (TYP.)
- SYMBOL INDICATES A CUT-SECTION IN CONDUIT. DEMOLISH ALL CONDUCTORS WITHIN CONDUIT AS SHOWN. CUT CONDUIT AND PRESERVE AND PROTECT EXISTING CONDUIT TO REMAIN AND BE REUSED IN THIS PROJECT.

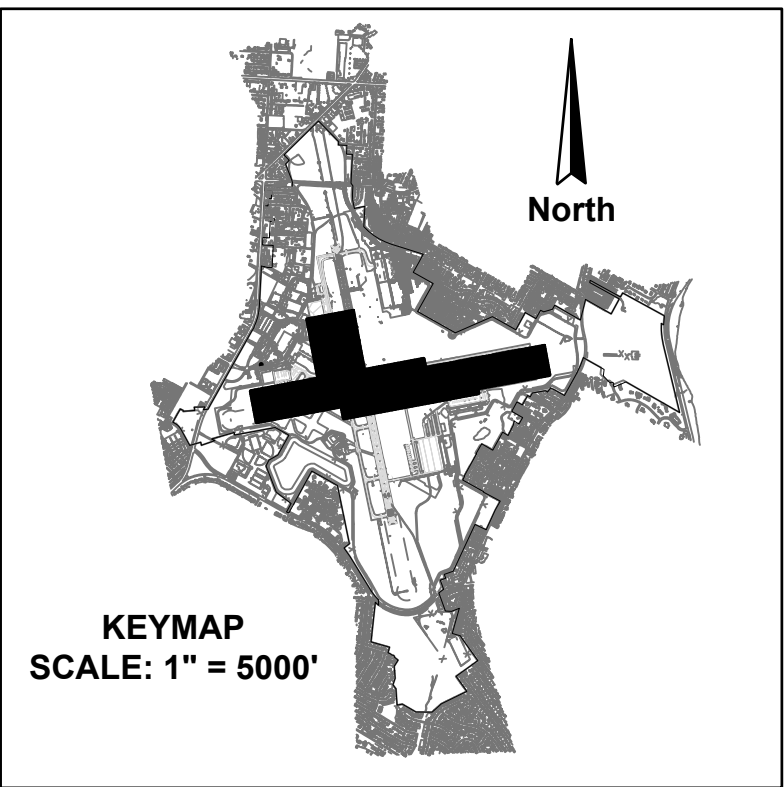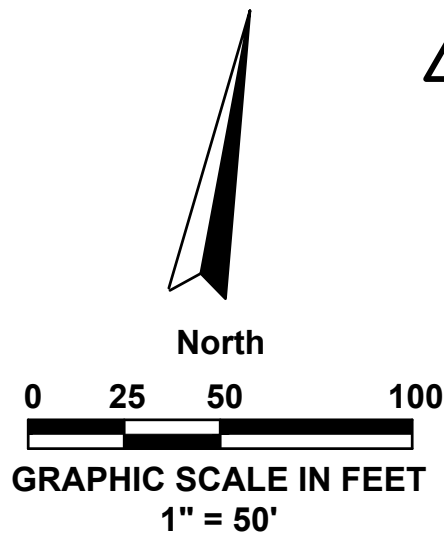

EXISTING
CONDITIONS AND
DEMOLITION PLAN
(SHEET 10 OF 11)
ISSUED FOR BID DRAWINGS

RUNWAY 8-26
REHABILITATION
PREPARED FOR
PENSACOLA INTERNATIONAL AIRPORT


DESIGNED BY: SAH
DRAWN BY: KJF
CHECKED BY: MAG
APPROVED BY: VCL
PROJECT NO: 24.0359.01
DATE: MARCH 28, 2025

SHEET NUMBER
E110

TRANSFORMING TODAY'S IDEAS
INTO TOMORROW'S REALITY

NO.	DATE	REVISION	BY
1	4/25	ADDENDUM 3	SAH
2			
3			
4			
5			
6			
7			
8			
9			
10			

AVCON, INC.
ENGINEERS & PLANNERS
3298 SUMMIT BLVD., SUITE 26
PENSACOLA, FL 32503
OFFICE: (850) 688-3326
CORPORATE CERTIFICATE OF
AUTHORIZATION NUMBER: 5057
WWW.AVCONINC.COM

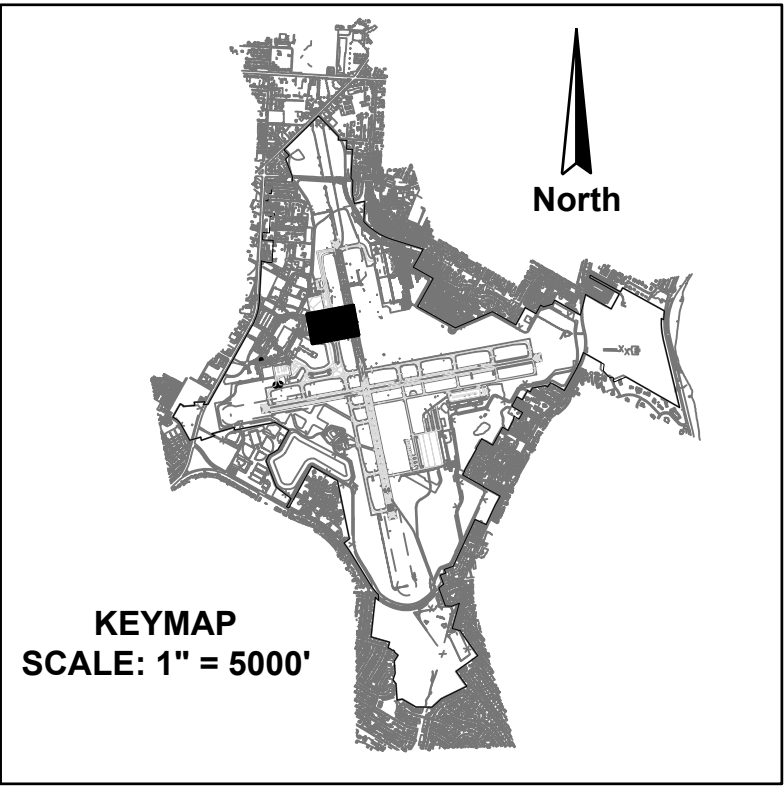

KEYMAP
SCALE: 1" = 5000'

North

0 25 50 100



GRAPHIC SCALE IN FEET
1" = 50'

1 PRESERVE AND PROTECT ALL FAA CABLES AND CONDUITS IN AREA. (TYP.)

2 SYMBOL INDICATES A CUT-SECTION IN CONDUIT. DEMOLISH ALL CONDUCTORS WITHIN CONDUIT AS SHOWN. CUT CONDUIT AND PRESERVE AND PROTECT EXISTING CONDUIT TO REMAIN AND BE REUSED IN THIS PROJECT.

- 1 PRESERVE AND PROTECT ALL FAA CABLES AND CONDUITS IN AREA. (TYP.)
- 2 SYMBOL INDICATES A CUT-SECTION IN CONDUIT. DEMOLISH ALL CONDUCTORS WITHIN CONDUIT AS SHOWN. CUT CONDUIT AND PRESERVE AND PROTECT EXISTING CONDUIT TO REMAIN AND BE REUSED IN THIS PROJECT.

N: \NICEVILLE-CAD\002_LOGOS\WPC\Avecon LOGO psmm.jpg

**TRANSFORMING TODAY'S IDEAS
INTO TOMORROW'S REALITY**

SA#	4/25	ADDENDUM 3	BY
1			
2			
**EXISTING
CONDITIONS AND
DEMOLITION PLAN
(SHEET 11 OF 11)
ISSUED FOR BID DRAWINGS**

RUNWAY 8-26 REHABILITATION

PREPARED FOR
PENSACOLA INTERNATIONAL AIRPORT


DESIGNED BY: SAH
DRAWN BY: KJF
CHECKED BY: MAG
APPROVED BY: VCL
PROJECT NO: 24.0359.01
DATE: MARCH 28, 2025

SHEET NUMBER
E111

THIS DOCUMENT CONTAINS PRIVILEGED AND PROPRIETARY INFORMATION, ALL OF WHICH IS EXPRESSLY PROVIDED BY AVCON, INC. FOR USE BY THE INTENDED RECIPIENT, AND FOR A SPECIFIC PURPOSE. WITHOUT THE EXPRESS WRITTEN CONSENT OF AVCON, INC. ANY DISTRIBUTION, REPRODUCTION, OR OTHER USE OF THIS DOCUMENT, IN WHOLE OR IN PART, IS STRICTLY PROHIBITED.

RW 17/35

RW 8/26

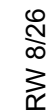

TRANSFORMING TODAY'S IDEAS
INTO TOMORROW'S REALITY

AVCON, INC.
ENGINEERS & PLANNERS

3298 SUMMIT BLVD., SUITE 26
PENSACOLA, FL 32503
OFFICE: (850) 696-3526
CORPORATE CERTIFICATE OF
AUTHORIZATION NUMBER: 5057
WWW.AVCONINC.COM

NONEXHAUSTIVE LISTING OF FIRM PROJECTS
NINETEENTH CENTURY LOGO: UPGRADES/LOGO: JPM 8/98

REPRODUCTION OR OTHER USE OF THIS DOCUMENT WITHOUT FIRM'S PERMISSION IS STRICTLY PROHIBITED

[illegible]

**EXISTING JCP
SCHEMATIC DIAGRAM
(SHEET 1 OF 4)**

ISSUED FOR BID DRAWINGS

RUNWAY 8-26 REHABILITATION

PREPARED FOR
PENSACOLA INTERNATIONAL AIRPORT

DESIGNED BY: SAH
DRAWN BY: KJR
CHECKED BY: MAG
APPROVED BY: VCL
PROJECT NO: 24.0359.01
DATE: MARCH 28, 2025

SHEET NUMBER
E112

A triangle with the number 1 inside.

SHEET NUMBER
E113

PREPARED FOR
PENSACOLA INTERNATIONAL AIRPORT

ISSUED FOR BID DRAWINGS

NO.	DATE	REVISION	BY
1	4/25	ADDENDUM 3	
2			
3			
4			
5			
6			
7			

AVCON, INC.
ENGINEERS & PLANNERS

**TRANSFORMING TODAY'S IDEAS
INTO TOMORROW'S REALITY**

THIS DOCUMENT CONTAINS PRIVILEGED AND PROPRIETARY INFORMATION, ALL OF WHICH IS EXPRESSLY PROVIDED BY AVCON, INC. FOR USE BY THE INTENDED RECIPIENT, AND FOR A SPECIFIC PURPOSE. WITHOUT THE EXPRESS WRITTEN CONSENT OF AVCON, INC. ANY DISTRIBUTION, REPRODUCTION, OR OTHER USE OF THIS DOCUMENT, IN WHOLE OR IN PART, IS STRICTLY PROHIBITED.



**RUNWAY 8-26
REHABILITATION**

PREPARED FOR
PENSACOLA INTERNATIONAL AIRPORT

**EXISTING JCP
SCHEMATIC DIAGRAM
(SHEET 3 OF 4)**

NO.	DATE	REVISION	BY
1	4/25	ADDENDUM 3	
2			
3			
4			
5			
6			
7			
8			
9			
10			

AVCON, INC.
ENGINEERS & PLANNERS
3298 SUMMIT BLVD., SUITE 26
PENSACOLA, FL. 32503
CORPORATE CERTIFICATE OF
AUTHORIZATION NUMBER: 5057
www.avconinc.com

TRANSFORMING TODAY'S IDEAS
INTO TOMORROW'S REALITY

N:\MCDIVILLE\CA2\W62_L0005\FPE\CA2\w62n1.L002.pptm.jpg



NO.	DATE	REVISION	BY
1	4/25	ADDENDUM 3	
2			
3			
4			
5			
6			
7			
8			
9			
10			

N:\359 CITY OF PENSACOLA-AIRPORT\2024-0359.01-PNS RUNWAY 8-26\000 CAD\24035901_E201-211.DWG 4/11/2025 11:19 AM


GENERAL LAYOUT NOTES:

- SEE SHEET E001 FOR GENERAL NOTES AND E002-E003 FOR SYMBOL LEGEND.
- SEE CONTRACT DETAILS AND CONTRACT SPECIFICATIONS SECTION L-125 AND L-110 FOR ADDITIONAL INFORMATION REGARDING INSTALLATION OF LIGHT FIXTURES, SIGNS AND ASSOCIATED CONDUIT.
- POSITION ALL BASE CANS WITH SURVEY INSTRUMENTS AS INDICATED IN THE CONTRACT DOCUMENTS. STAKE LOCATION OF ALL BASE CANS PRIOR TO INSTALLATION TO DEMONSTRATE ACCURACY OF LAYOUT, SPACING INTERVALS, AND COORDINATION WITH PAVING JOINTS AND SITE FEATURES. BRING CONFLICTS TO THE ATTENTION OF THE ENGINEER. ALLOW 5 CALENDAR DAYS FOR A RESOLUTION.


- ALL FIXTURES, SIGNS, BASE CANS, ETC., SHALL BE INSTALLED AS SHOWN ON THE CONTRACT DOCUMENTS OR ACCEPTED SHOP DRAWINGS AND IN ACCORDANCE WITH THE APPLICABLE FAA ADVISORY CIRCULARS AND MANUFACTURERS' RECOMMENDATIONS. SURVEY INSTRUMENTS SHALL BE USED TO POSITION ALL ITEMS TO INSURE PRECISE ORIENTATION. TOLERANCES GIVEN IN THE FAA ADVISORY CIRCULARS AND THE CONTRACT DOCUMENTS SHALL NOT BE EXCEEDED. WHERE NO TOLERANCE IS GIVEN, NO DEVIATION IS PERMITTED. ITEMS NOT INSTALLED IN ACCORDANCE WITH THE FAA ADVISORY CIRCULARS AND THE CONTRACT DOCUMENTS SHALL BE REPLACED BY AND AT THE EXPENSE OF THE CONTRACTOR.

- POSITION ALL BASE CANS WITH SURVEY INSTRUMENTS AS INDICATED IN THE CONTRACT DOCUMENTS. STAKE LOCATION OF ALL BASE CANS PRIOR TO INSTALLATION TO DEMONSTRATE ACCURACY OF LAYOUT, SPACING INTERVALS, AND COORDINATION WITH PAVING JOINTS AND SITE FEATURES. BRING CONFLICTS TO THE ATTENTION OF THE ENGINEER. ALLOW 5 CALENDAR DAYS FOR A RESOLUTION.
- EDGE LIGHT UNITS SHALL BE 10 FEET OFF THE FULL STRENGTH EDGE OF PAVEMENT (UNLESS SPECIFICALLY INDICATED OTHERWISE). ON STRAIGHT SECTIONS, THEY SHALL BE OPTICALLY IN LINE WHEN SIGHTED FROM EITHER END OF A STRAIGHT SECTION. BASE CANS FOR EDGE LIGHT UNITS SHALL BE INSTALLED AT THE DESIGNATED LOCATIONS WITH TOP FLANGES AT THE REQUIRED ELEVATION AND WITHIN 2 DEGREES OF LEVEL. ALL ELEVATED EDGE LIGHTS SHALL BE INSTALLED AT AN EQUAL HEIGHT ABOVE GRADE NOT TO EXCEED 14 INCHES.


- SEMI-FLUSH LIGHT UNITS SHALL BE LOCATED AS SHOWN IN THE CONTRACT DOCUMENTS. ALL SEMI-FLUSH LIGHTS SHALL BE INSTALLED LEVEL WITH THE TOP EDGE BETWEEN PLUS 0-INCH AND MINUS 1/16 INCHES FROM THE PAVEMENT'S FINAL FINISH GRADE. LIGHT BASE CANS MUST BE ALIGNED PARALLEL TO THE CENTERLINE WITH A TOLERANCE OF PLUS OR MINUS 1/2 DEGREE. PROVIDE TIGHTER TOLERANCES IF REQUIRED BY FIXTURE MANUFACTURER TO MEET ADVISORY CIRCULAR PHOTOMETRIC PERFORMANCE CRITERIA.
- LOCATE MANDATORY SIGNS IN ACCORDANCE WITH DETAIL ON SHEET E512.

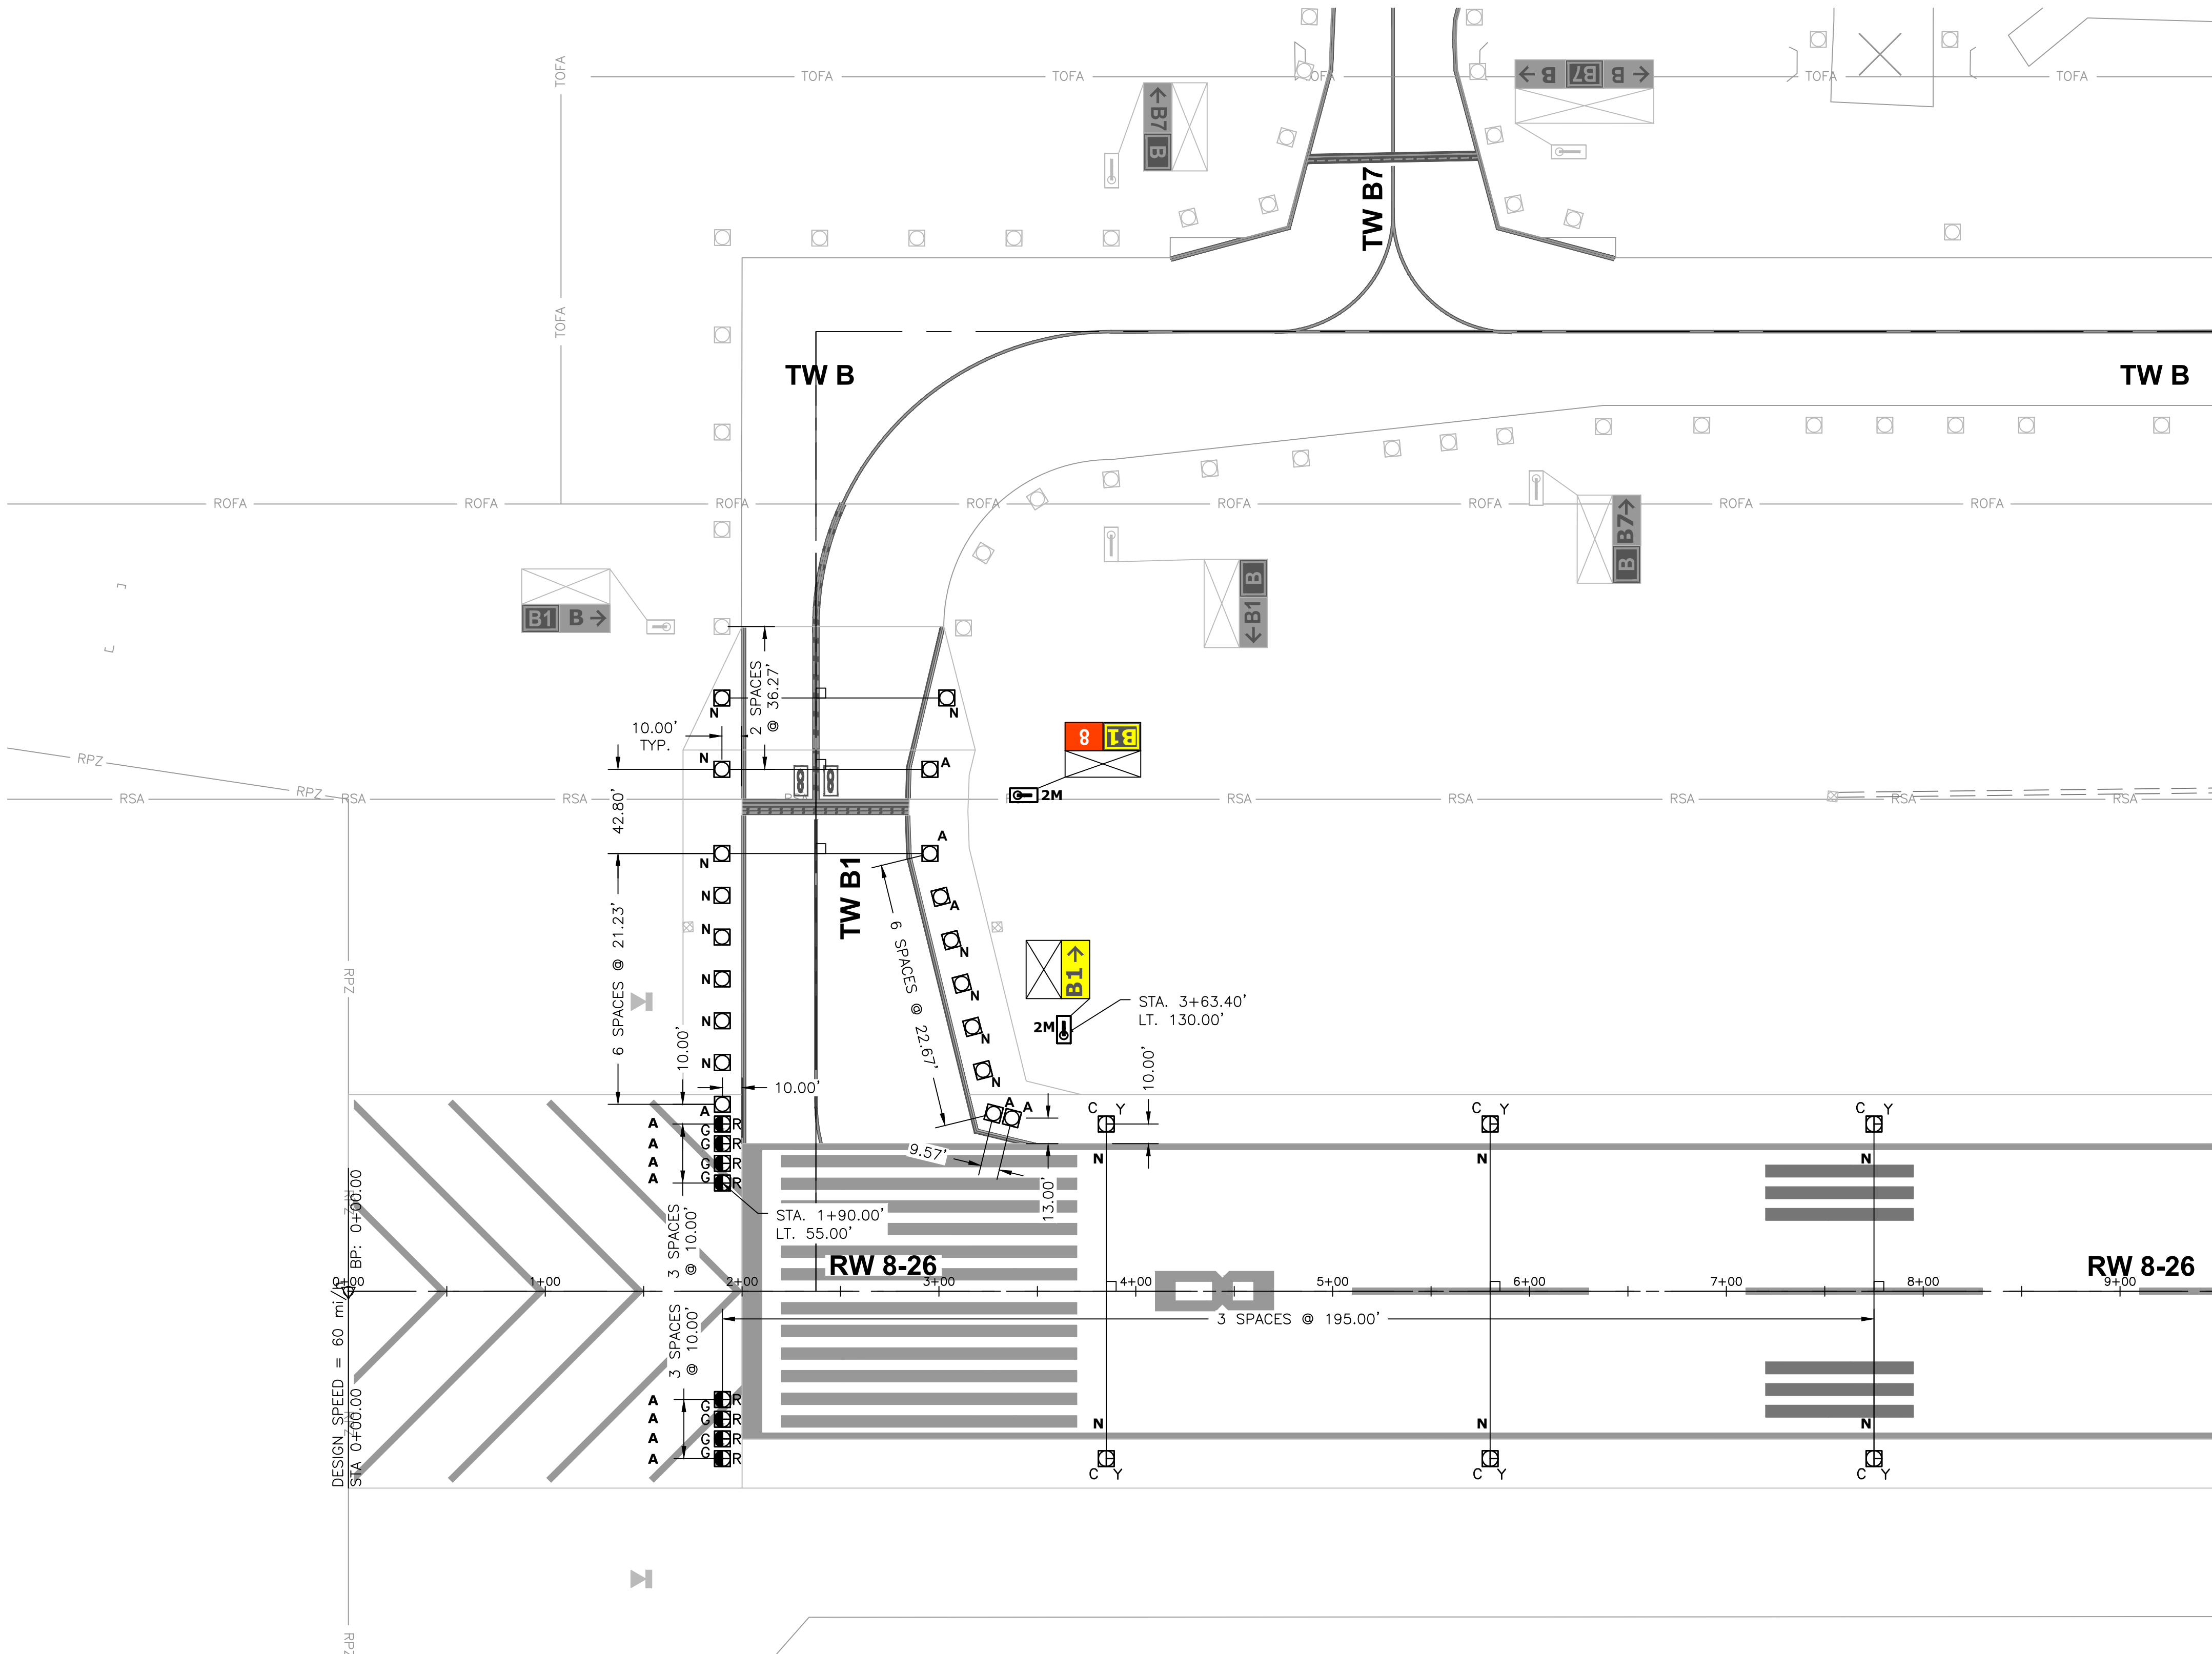

MATCH LINE - SEE SHEET E202

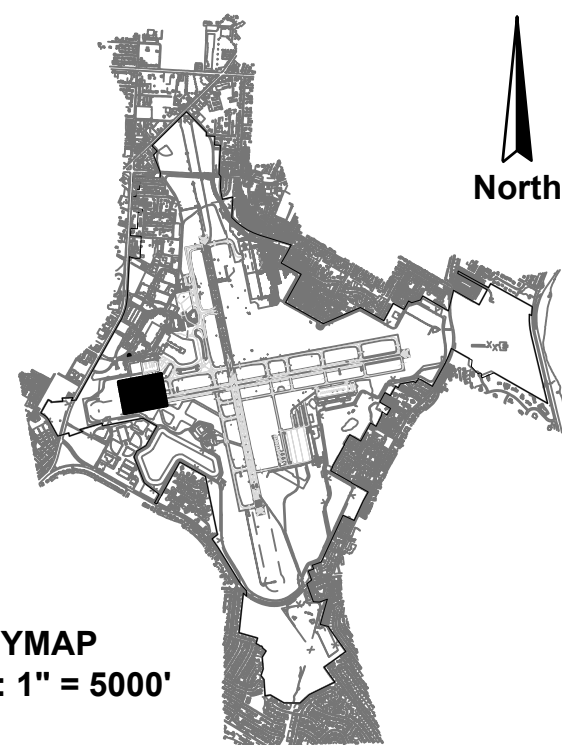

KEYMAP
SCALE: 1" = 5000'

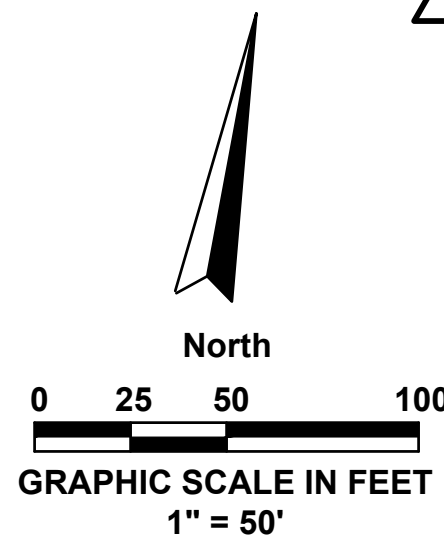

RUNWAY 8-26 REHABILITATION

PREPARED FOR
PENSACOLA INTERNATIONAL AIRPORT

DESIGNED BY: SAH
DRAWN BY: KJF
CHECKED BY: MAG
APPROVED BY: VCL
PROJECT NO: 24.0359.01
DATE: MARCH 28, 2025

SHEET NUMBER
E201

AIRFIELD LIGHTING LAYOUT PLAN (SHEET 1 OF 11)

ISSUED FOR BID DRAWINGS


NO.	DATE	REVISION	BY
1	4/25	ADDENDUM 3	SAH
2			
3			
4			
5			
6			
7			
8			
9			
10			

AVCON, INC.
ENGINEERS & PLANNERS
3298 SUMMIT BLVD., SUITE 26
PENSACOLA, FL 32503
OFFICE: (850) 688-3526
CORPORATE CERTIFICATE OF
AUTHORIZATION NUMBER: 5057
WWW.AVCONINC.COM

TRANSFORMING TODAY'S IDEAS
INTO TOMORROW'S REALITY

N:\359 CITY OF PENSACOLA-AIRPORT\2024.0359.01-PNS RUNWAY 8-26\000 CAD\24035901_E201-211.DWG 4/11/2025 11:20 AM

MATCH LINE - SEE SHEET E201

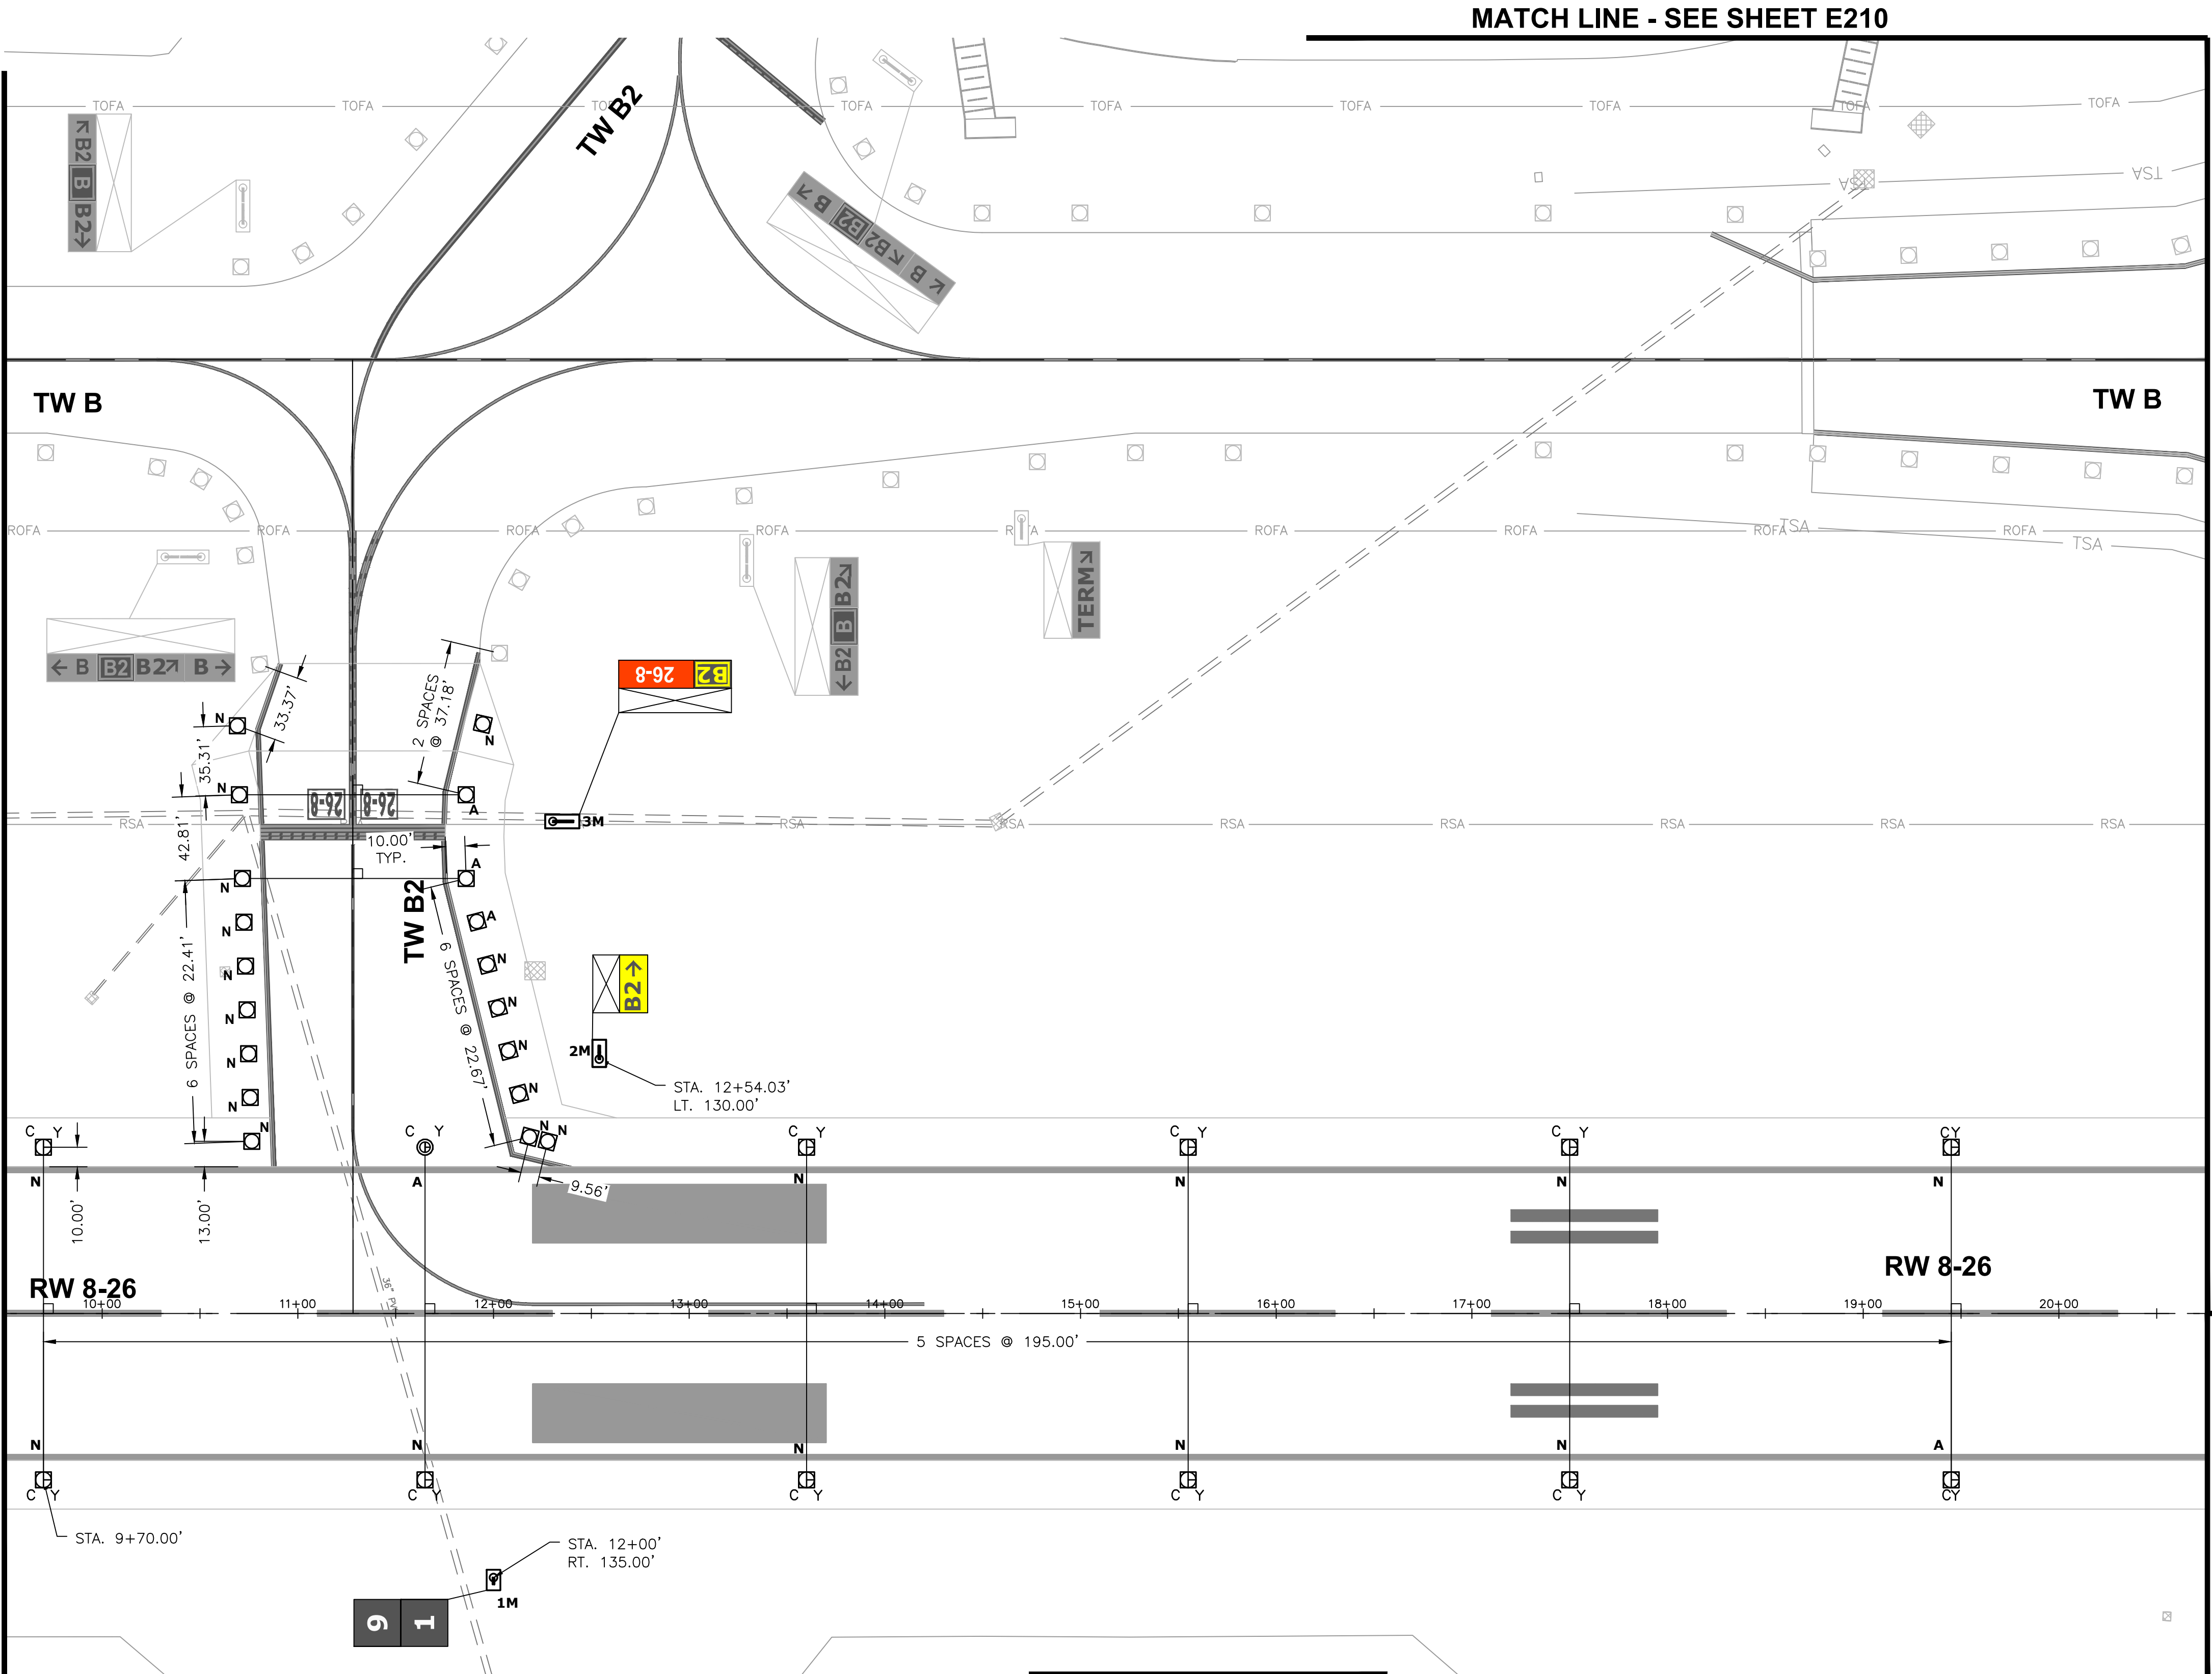


NOTES:



- SEE SHEET E201 FOR GENERAL LAYOUT NOTES.

MATCH LINE - THIS SHEET

MATCH LINE - SEE SHEET E204

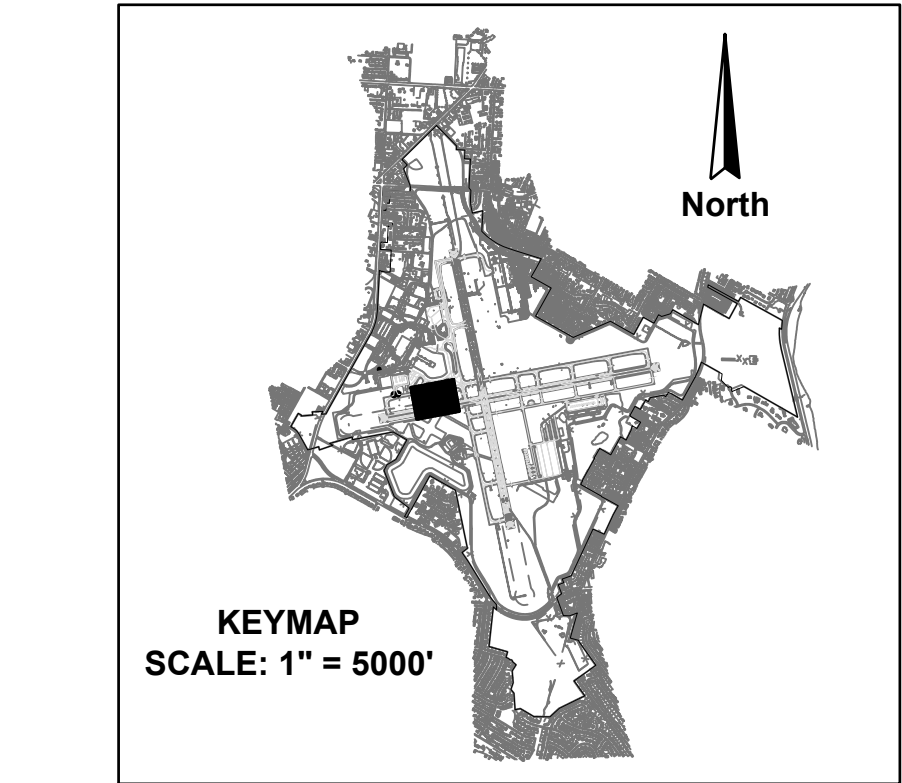

MATCH LINE - THIS SHEET

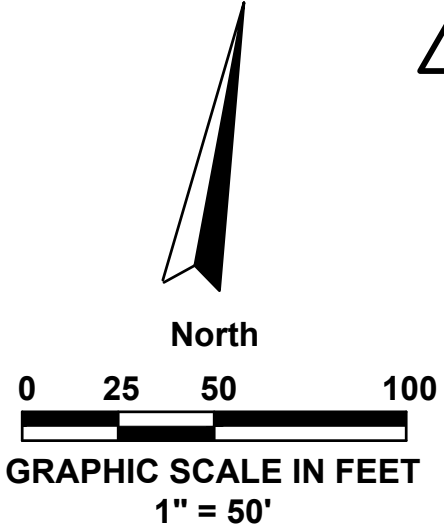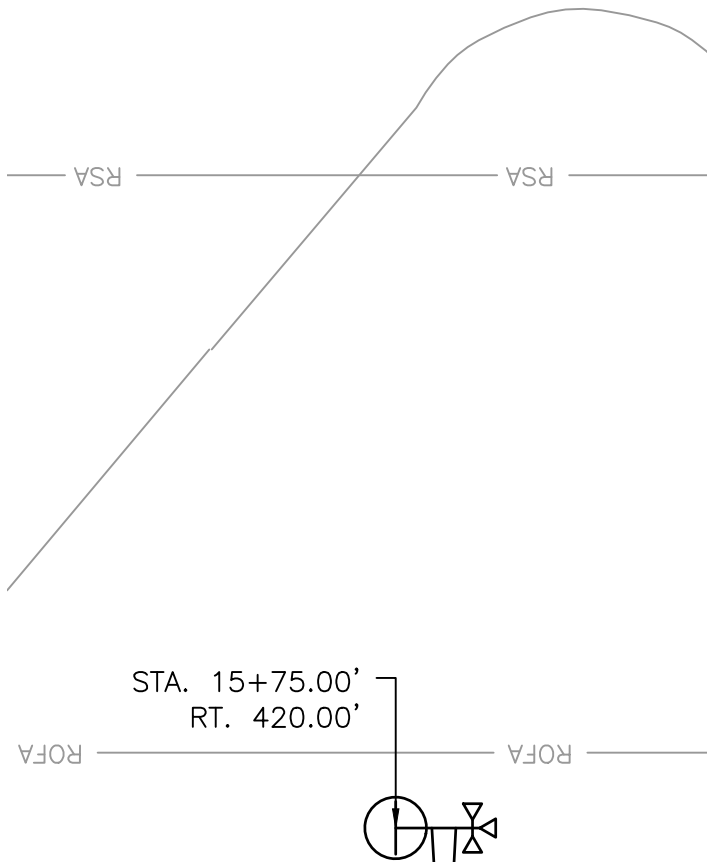

RUNWAY 8-26
REHABILITATION
PREPARED FOR
PENSACOLA INTERNATIONAL AIRPORT

AIRFIELD LIGHTING
LAYOUT PLAN
(SHEET 2 OF 11)
ISSUED FOR BID DRAWINGS

NO.	DATE	REVISION	BY
1	4/25	ADDENDUM 3	SAH
2			
3			
4			
5			
6			
7			
8			
9			
10			

AVCON, INC.
ENGINEERS & PLANNERS
3298 SUMMIT BLVD., SUITE 26
PENSACOLA, FL 32503
OFFICE: (850) 688-3326
CORPORATE CERTIFICATE OF
AUTHORIZATION NUMBER: 5057
WWW.AVCONINC.COM

TRANSFORMING TODAY'S IDEAS
INTO TOMORROW'S REALITY

DESIGNED BY: SAH
DRAWN BY: KJF
CHECKED BY: MAG
APPROVED BY: VCL
PROJECT NO: 24.0359.01
DATE: MARCH 28, 2025


SHEET NUMBER
E202

N:\359 CITY OF PENSACOLA-AIRPORT\2024.0359.01-PNS RUNWAY 8-26\000 CAD\24035901_E201-211.DWG 4/11/2025 11:20 AM

NOTES:



1. SEE SHEET E201 FOR GENERAL LAYOUT NOTES.

MATCH LINE - SEE SHEET E202

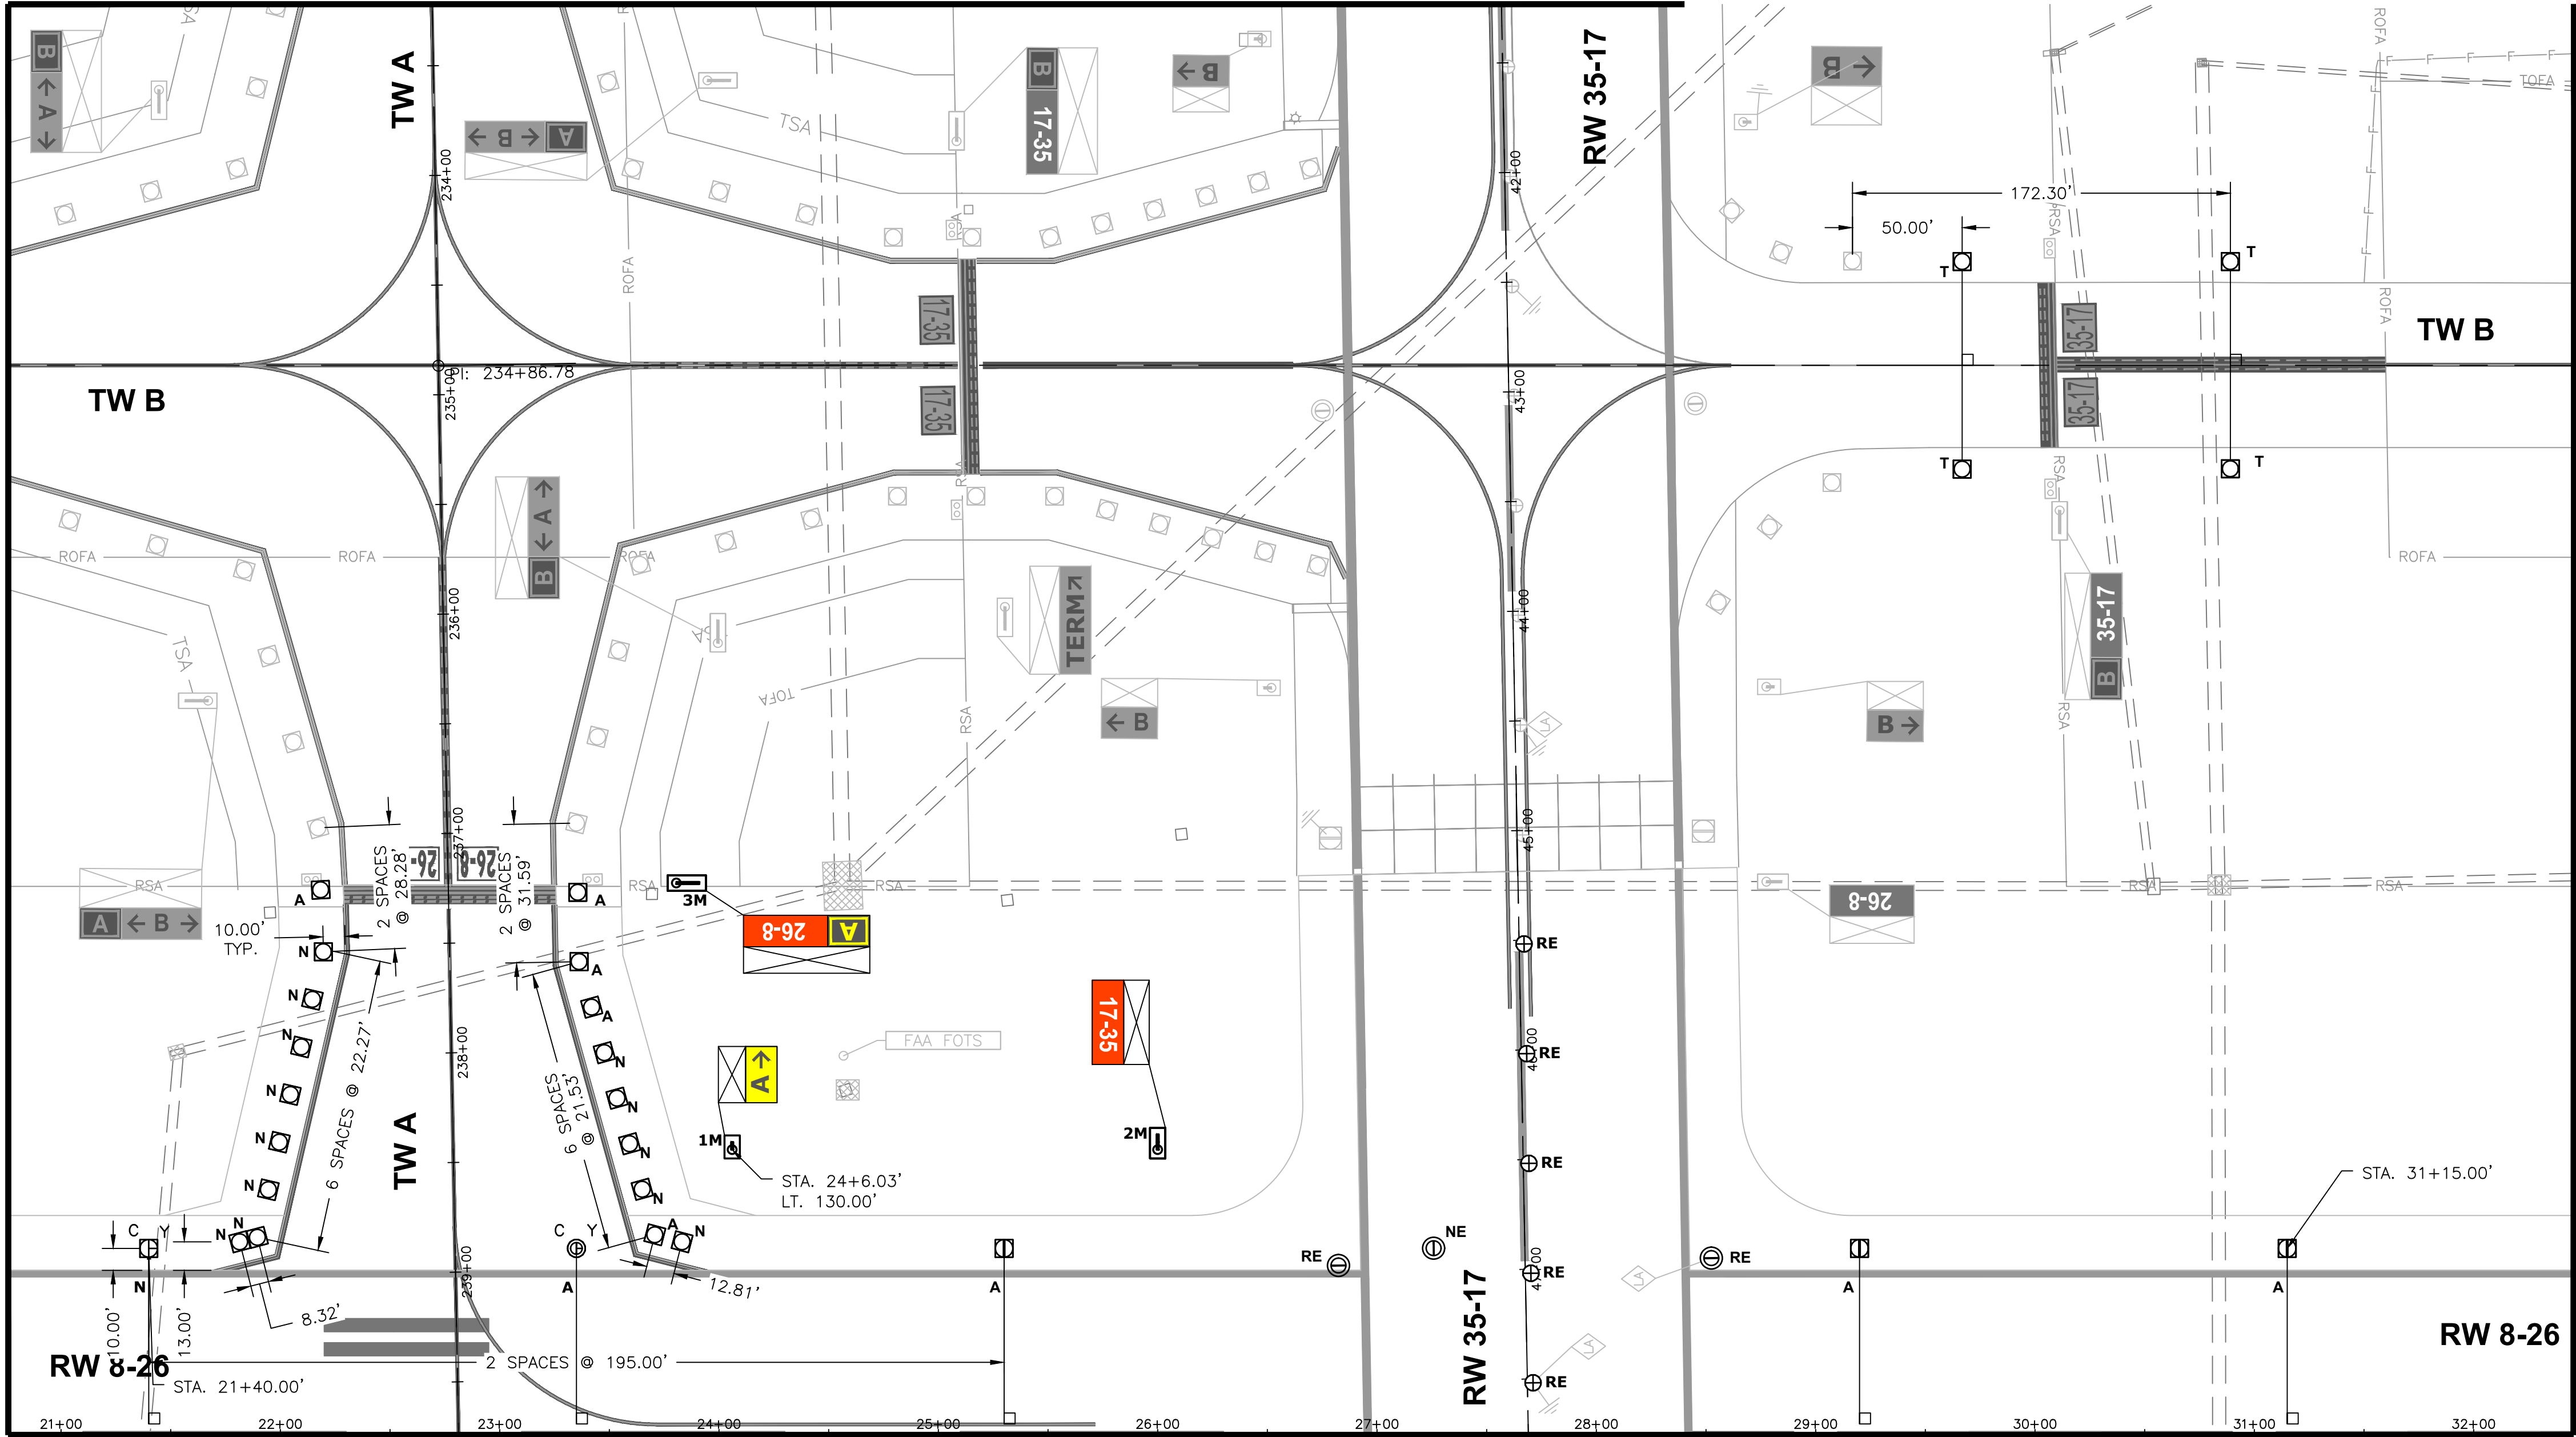

MATCH LINE - SEE SHEET E204

MATCH LINE - SEE SHEET E205

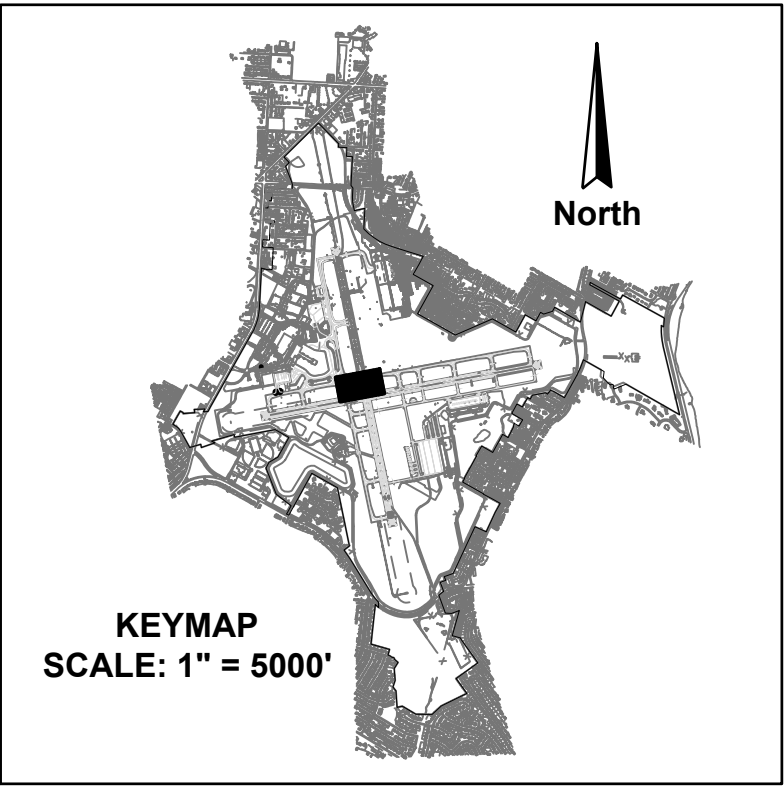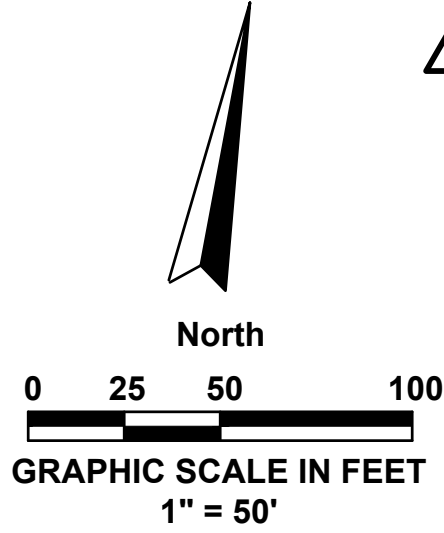

**RUNWAY 8-26
REHABILITATION**
PREPARED FOR
PENSACOLA INTERNATIONAL AIRPORT

DESIGNED BY: SAH
DRAWN BY: KJF
CHECKED BY: MAG
APPROVED BY: VCL
PROJECT NO: 24.0359.01
DATE: MARCH 28, 2025

**SHEET NUMBER
E203**

**AIRFIELD LIGHTING
LAYOUT PLAN
(SHEET 3 OF 11)**
ISSUED FOR BID DRAWINGS

NO.	DATE	REVISION	BY
1	4/25	ADDENDUM 3	SAH

AVCON, INC.
ENGINEERS & PLANNERS
3298 SUMMIT BLVD., SUITE 26
PENSACOLA, FL 32503
OFFICE: (850) 688-3526
CORPORATE CERTIFICATE OF
AUTHORIZATION NUMBER: 5057
WWW.AVCONINC.COM




TRANSFORMING TODAY'S IDEAS
INTO TOMORROW'S REALITY

THIS DOCUMENT CONTAINS PRIVILEGED AND PROPRIETARY INFORMATION, ALL OF WHICH IS EXPRESSLY PROVIDED BY AVCON, INC., FOR USE BY THE INTENDED RECIPIENT, AND FOR A SPECIFIC PURPOSE. WITHOUT THE EXPRESS WRITTEN CONSENT OF AVCON, INC., ANY DISTRIBUTION, REPRODUCTION, OR OTHER USE OF THIS DOCUMENT, IN WHOLE OR IN PART, IS STRICTLY PROHIBITED.

N:\359 CITY OF PENSACOLA-AIRPORT\2024.0359.01-PNS RUNWAY 8-26\000 CAD\24035901_E201-211.DWG 4/11/2025 11:20 AM

NOTES:

1. SEE SHEET E201 FOR GENERAL LAYOUT NOTES.

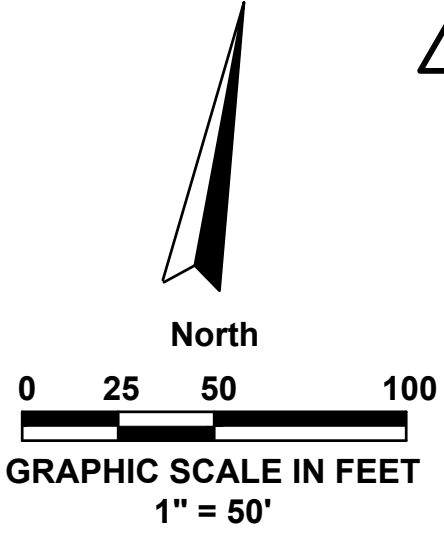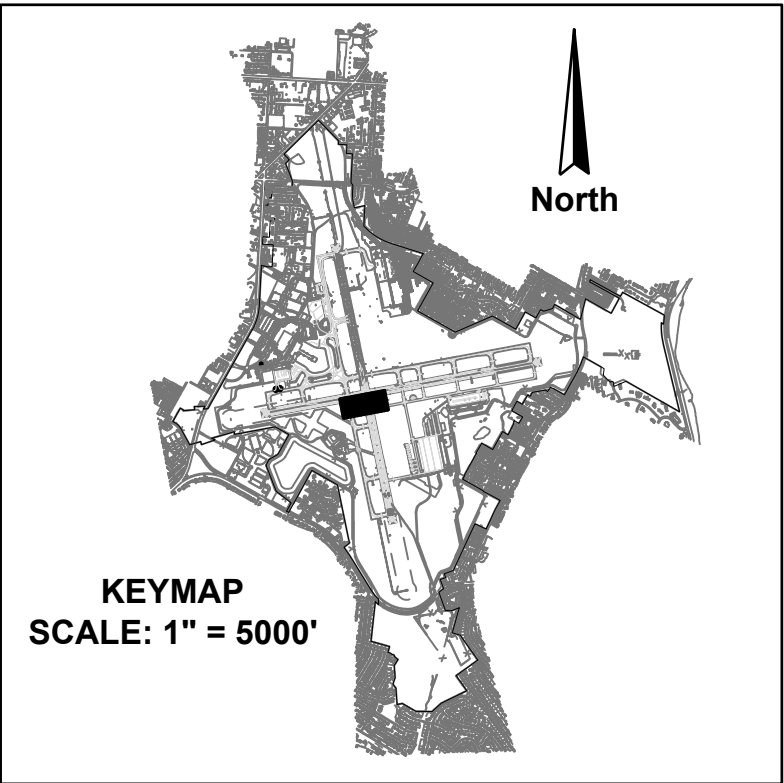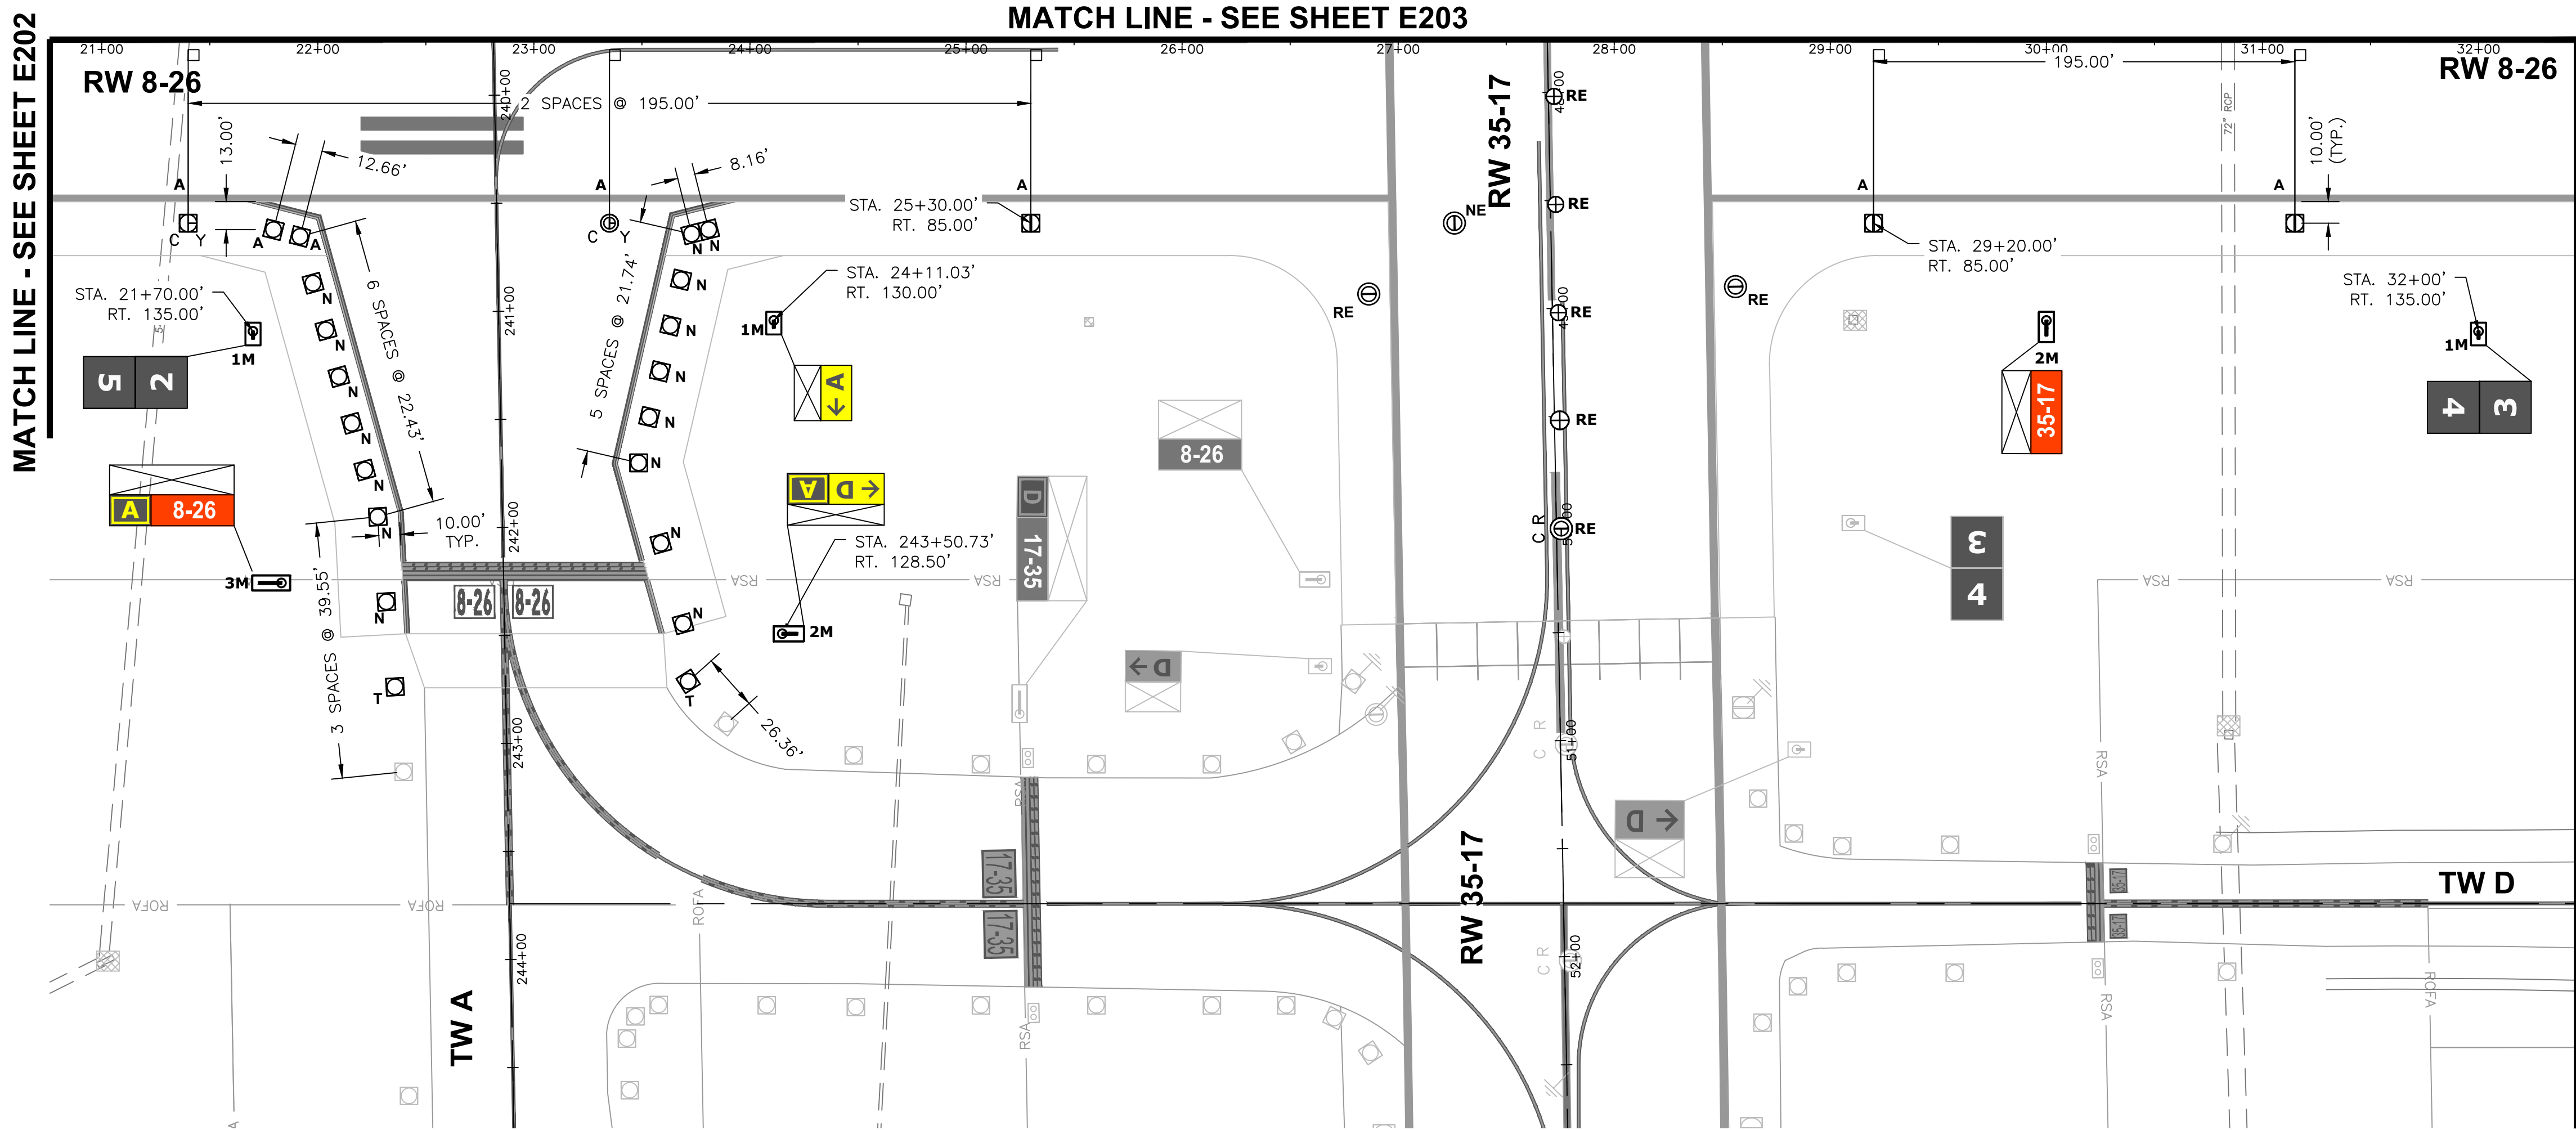

RUNWAY 8-26 REHABILITATION

PREPARED FOR
PENSACOLA INTERNATIONAL AIRPORT

DESIGNED BY: SAH
DRAWN BY: KJF
CHECKED BY: MAG
APPROVED BY: VCL
PROJECT NO: 24.0359.01
DATE: MARCH 28, 2025

SHEET NUMBER E204

AIRFIELD LIGHTING LAYOUT PLAN (SHEET 4 OF 11)

ISSUED FOR BID DRAWINGS

AVCON, INC.
ENGINEERS & PLANNERS
3298 SUMMIT BLVD., SUITE 26
PENSACOLA, FL 32503
OFFICE: (850) 688-3526
CORPORATE CERTIFICATE OF AUTHORIZATION NUMBER: 5057
WWW.AVCONINC.COM

TRANSFORMING TODAY'S IDEAS INTO TOMORROW'S REALITY

4/25 ADDENDUM 3 SAH




NO.	DATE	REVISION	BY
1			
2			
THIS DOCUMENT CONTAINS PRIVILEGED AND PROPRIETARY INFORMATION. ALL OF WHICH IS EXPRESSLY PROVIDED BY AVCON, INC., FOR USE BY THE INTENDED RECIPIENT, AND FOR A SPECIFIC PURPOSE. WITHOUT THE EXPRESS WRITTEN CONSENT OF AVCON, INC. ANY DISTRIBUTION, REPRODUCTION, OR OTHER USE OF THIS DOCUMENT, IN WHOLE OR IN PART, IS STRICTLY PROHIBITED.

N:\359 CITY OF PENSACOLA-AIRPORT\2024-0359.01-PNS RUNWAY 8-26\000 CAD\24035901_E201-211.DWG 4/11/2025 11:20 AM

NOTES:
1. SEE SHEET E201 FOR GENERAL LAYOUT NOTES.

MATCH LINE - SEE SHEET E204

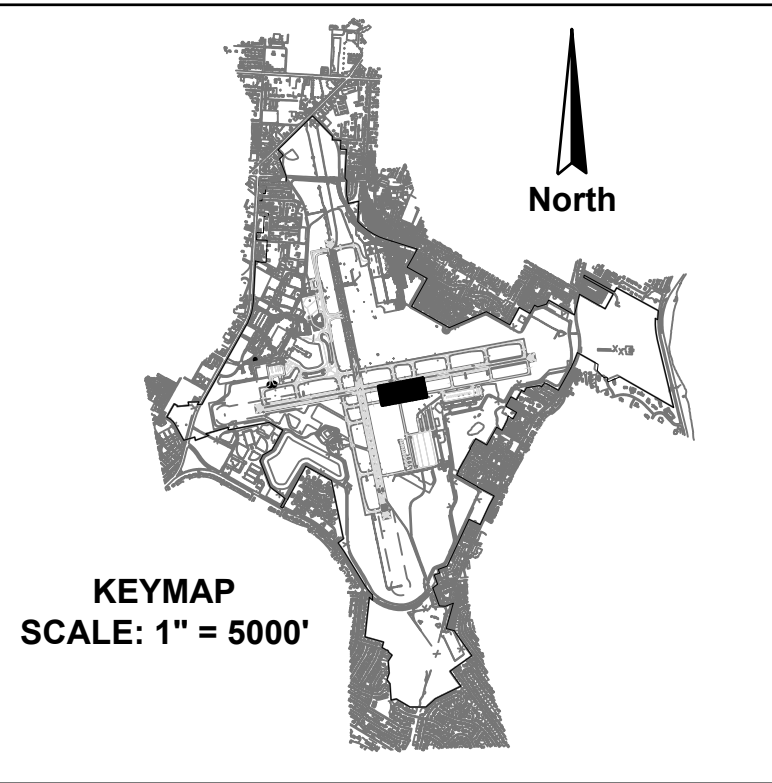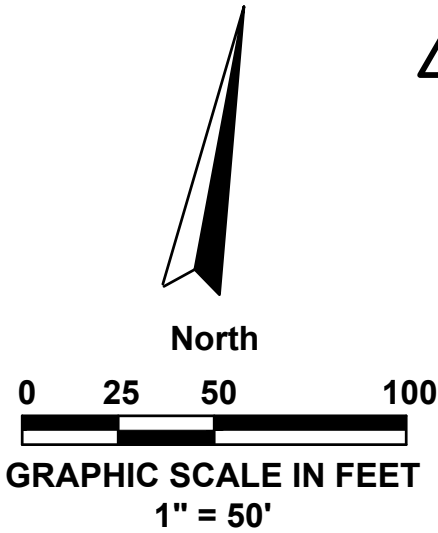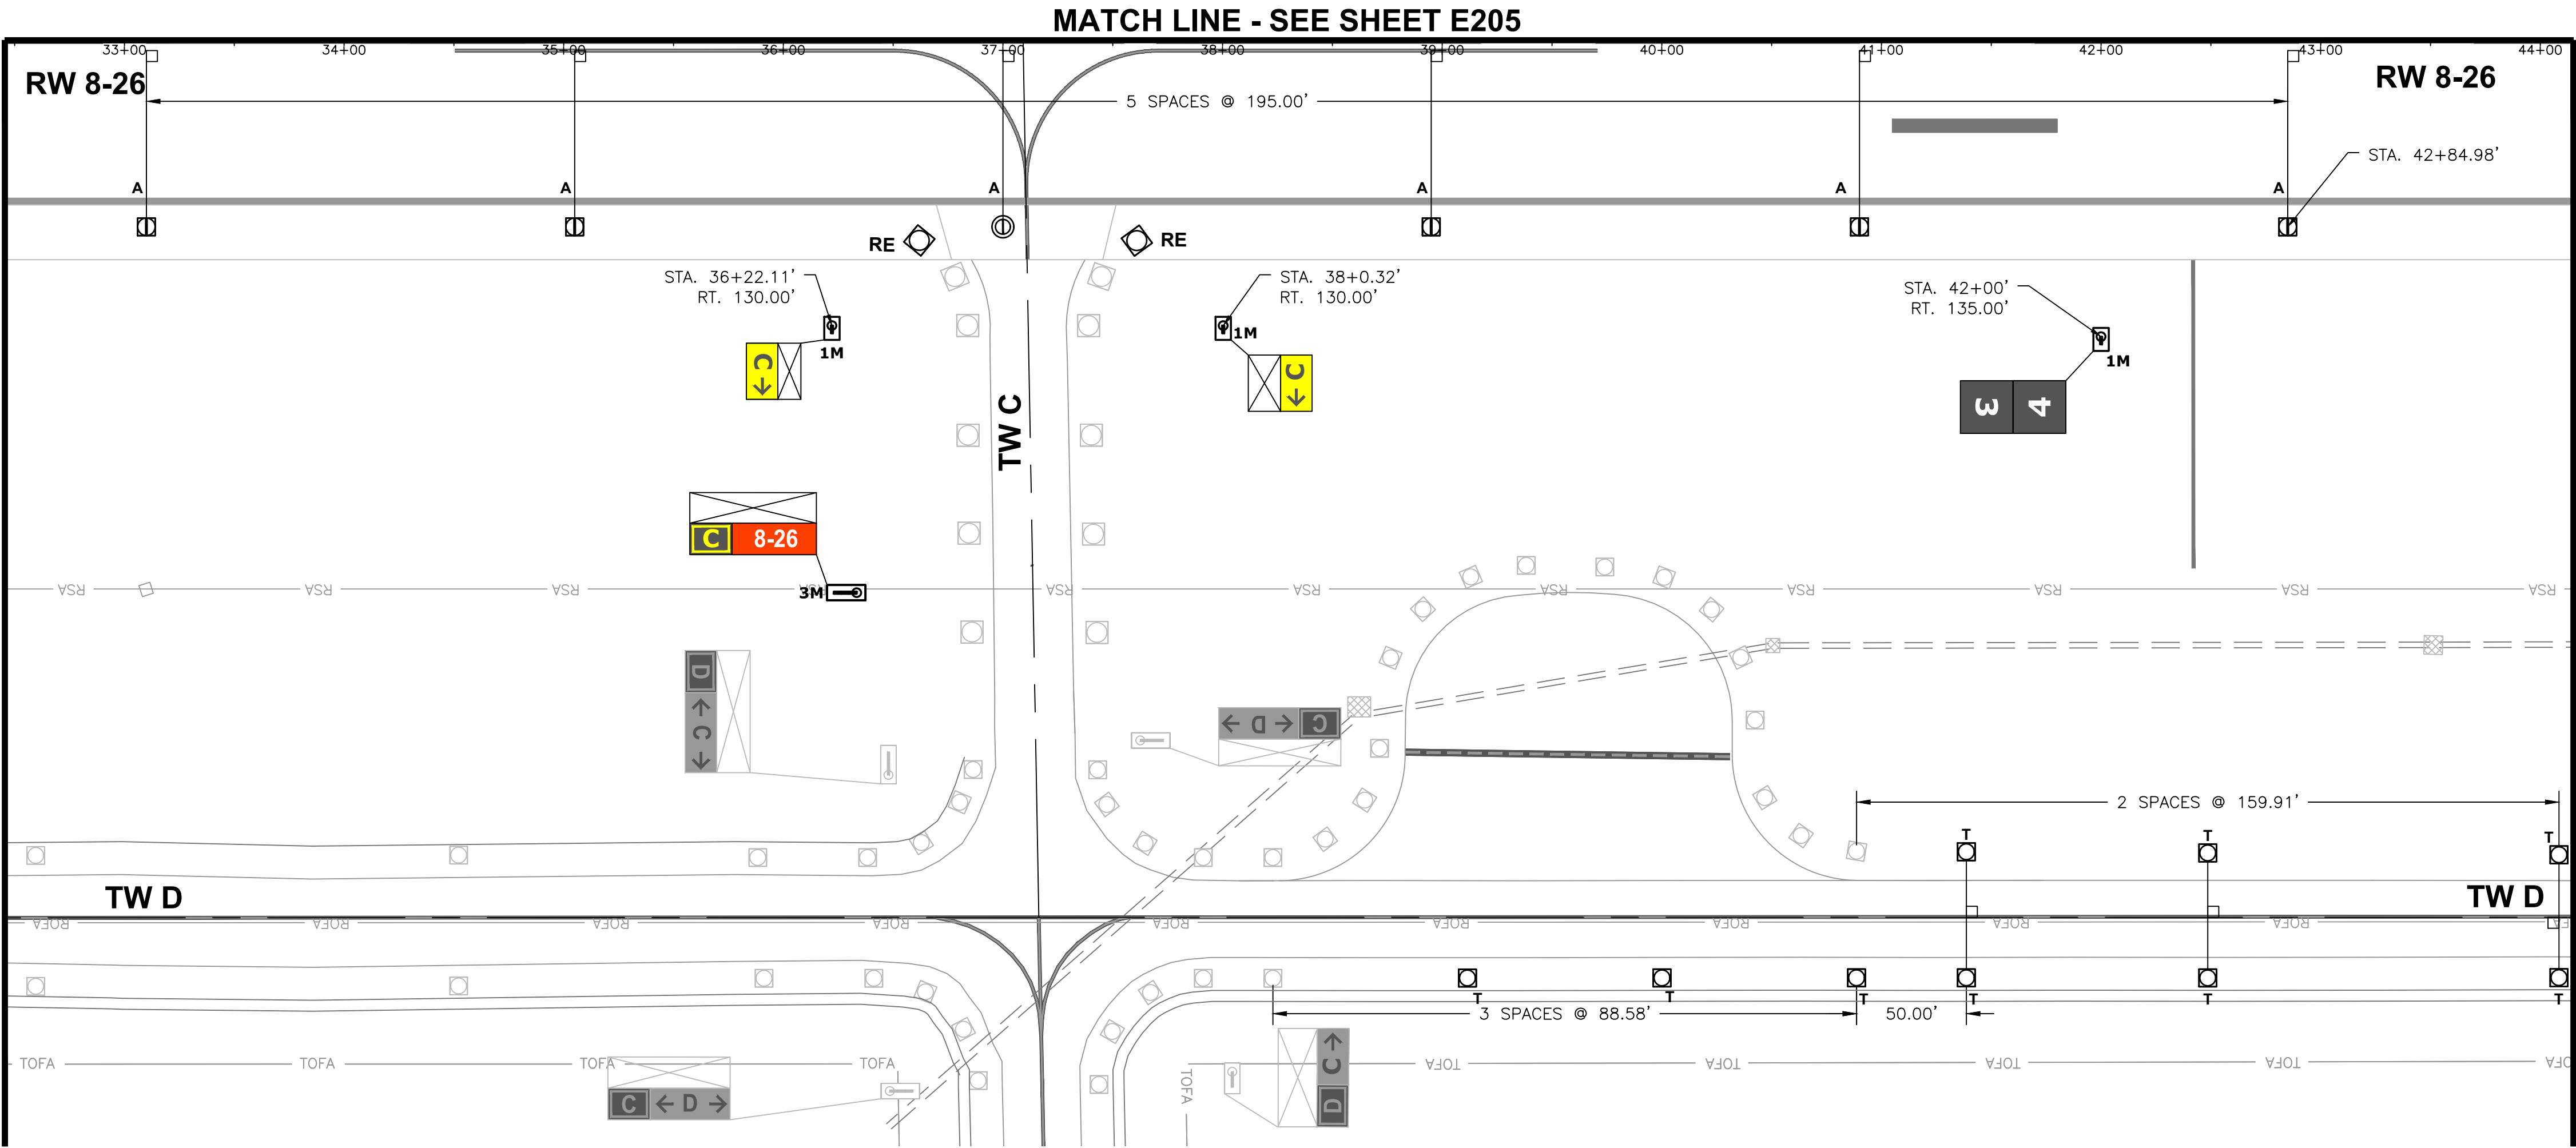

**RUNWAY 8-26
REHABILITATION**
PREPARED FOR
PENSACOLA INTERNATIONAL AIRPORT

**AIRFIELD LIGHTING
LAYOUT PLAN
(SHEET 6 OF 11)**
ISSUED FOR BID DRAWINGS

NO.	DATE	REVISION	BY
1	4/25	ADDENDUM 3	SAH

AVCON, INC.
ENGINEERS & PLANNERS
3298 SUMMIT BLVD., SUITE 26
PENSACOLA, FL 32503
OFFICE: (850) 688-3326
CORPORATE CERTIFICATE OF
AUTHORIZATION NUMBER: 5057
WWW.AVCONINC.COM

TRANSFORMING TODAY'S IDEAS
INTO TOMORROW'S REALITY

DESIGNED BY: SAH
DRAWN BY: KJF
CHECKED BY: MAG
APPROVED BY: VCL
PROJECT NO: 24.0359.01
DATE: MARCH 28, 2025


**SHEET NUMBER
E206**

THIS DOCUMENT CONTAINS PRIVILEGED AND PROPRIETARY INFORMATION, ALL OF WHICH IS EXPRESSLY PROVIDED BY AVCON, INC., FOR USE BY THE INTENDED RECIPIENT, AND FOR A SPECIFIC PURPOSE. WITHOUT THE EXPRESS WRITTEN CONSENT OF AVCON, INC. ANY DISTRIBUTION, REPRODUCTION, OR OTHER USE OF THIS DOCUMENT, IN WHOLE OR IN PART, IS STRICTLY PROHIBITED.



N:\359 CITY OF PENSACOLA-AIRPORT\2024.0359.01-PNS RUNWAY 8-26\000 CAD\24035901_E201-211.DWG 4/11/2025 11:21 AM

MATCH LINE - SEE SHEET E206

MATCH LINE - SEE SHEET E205

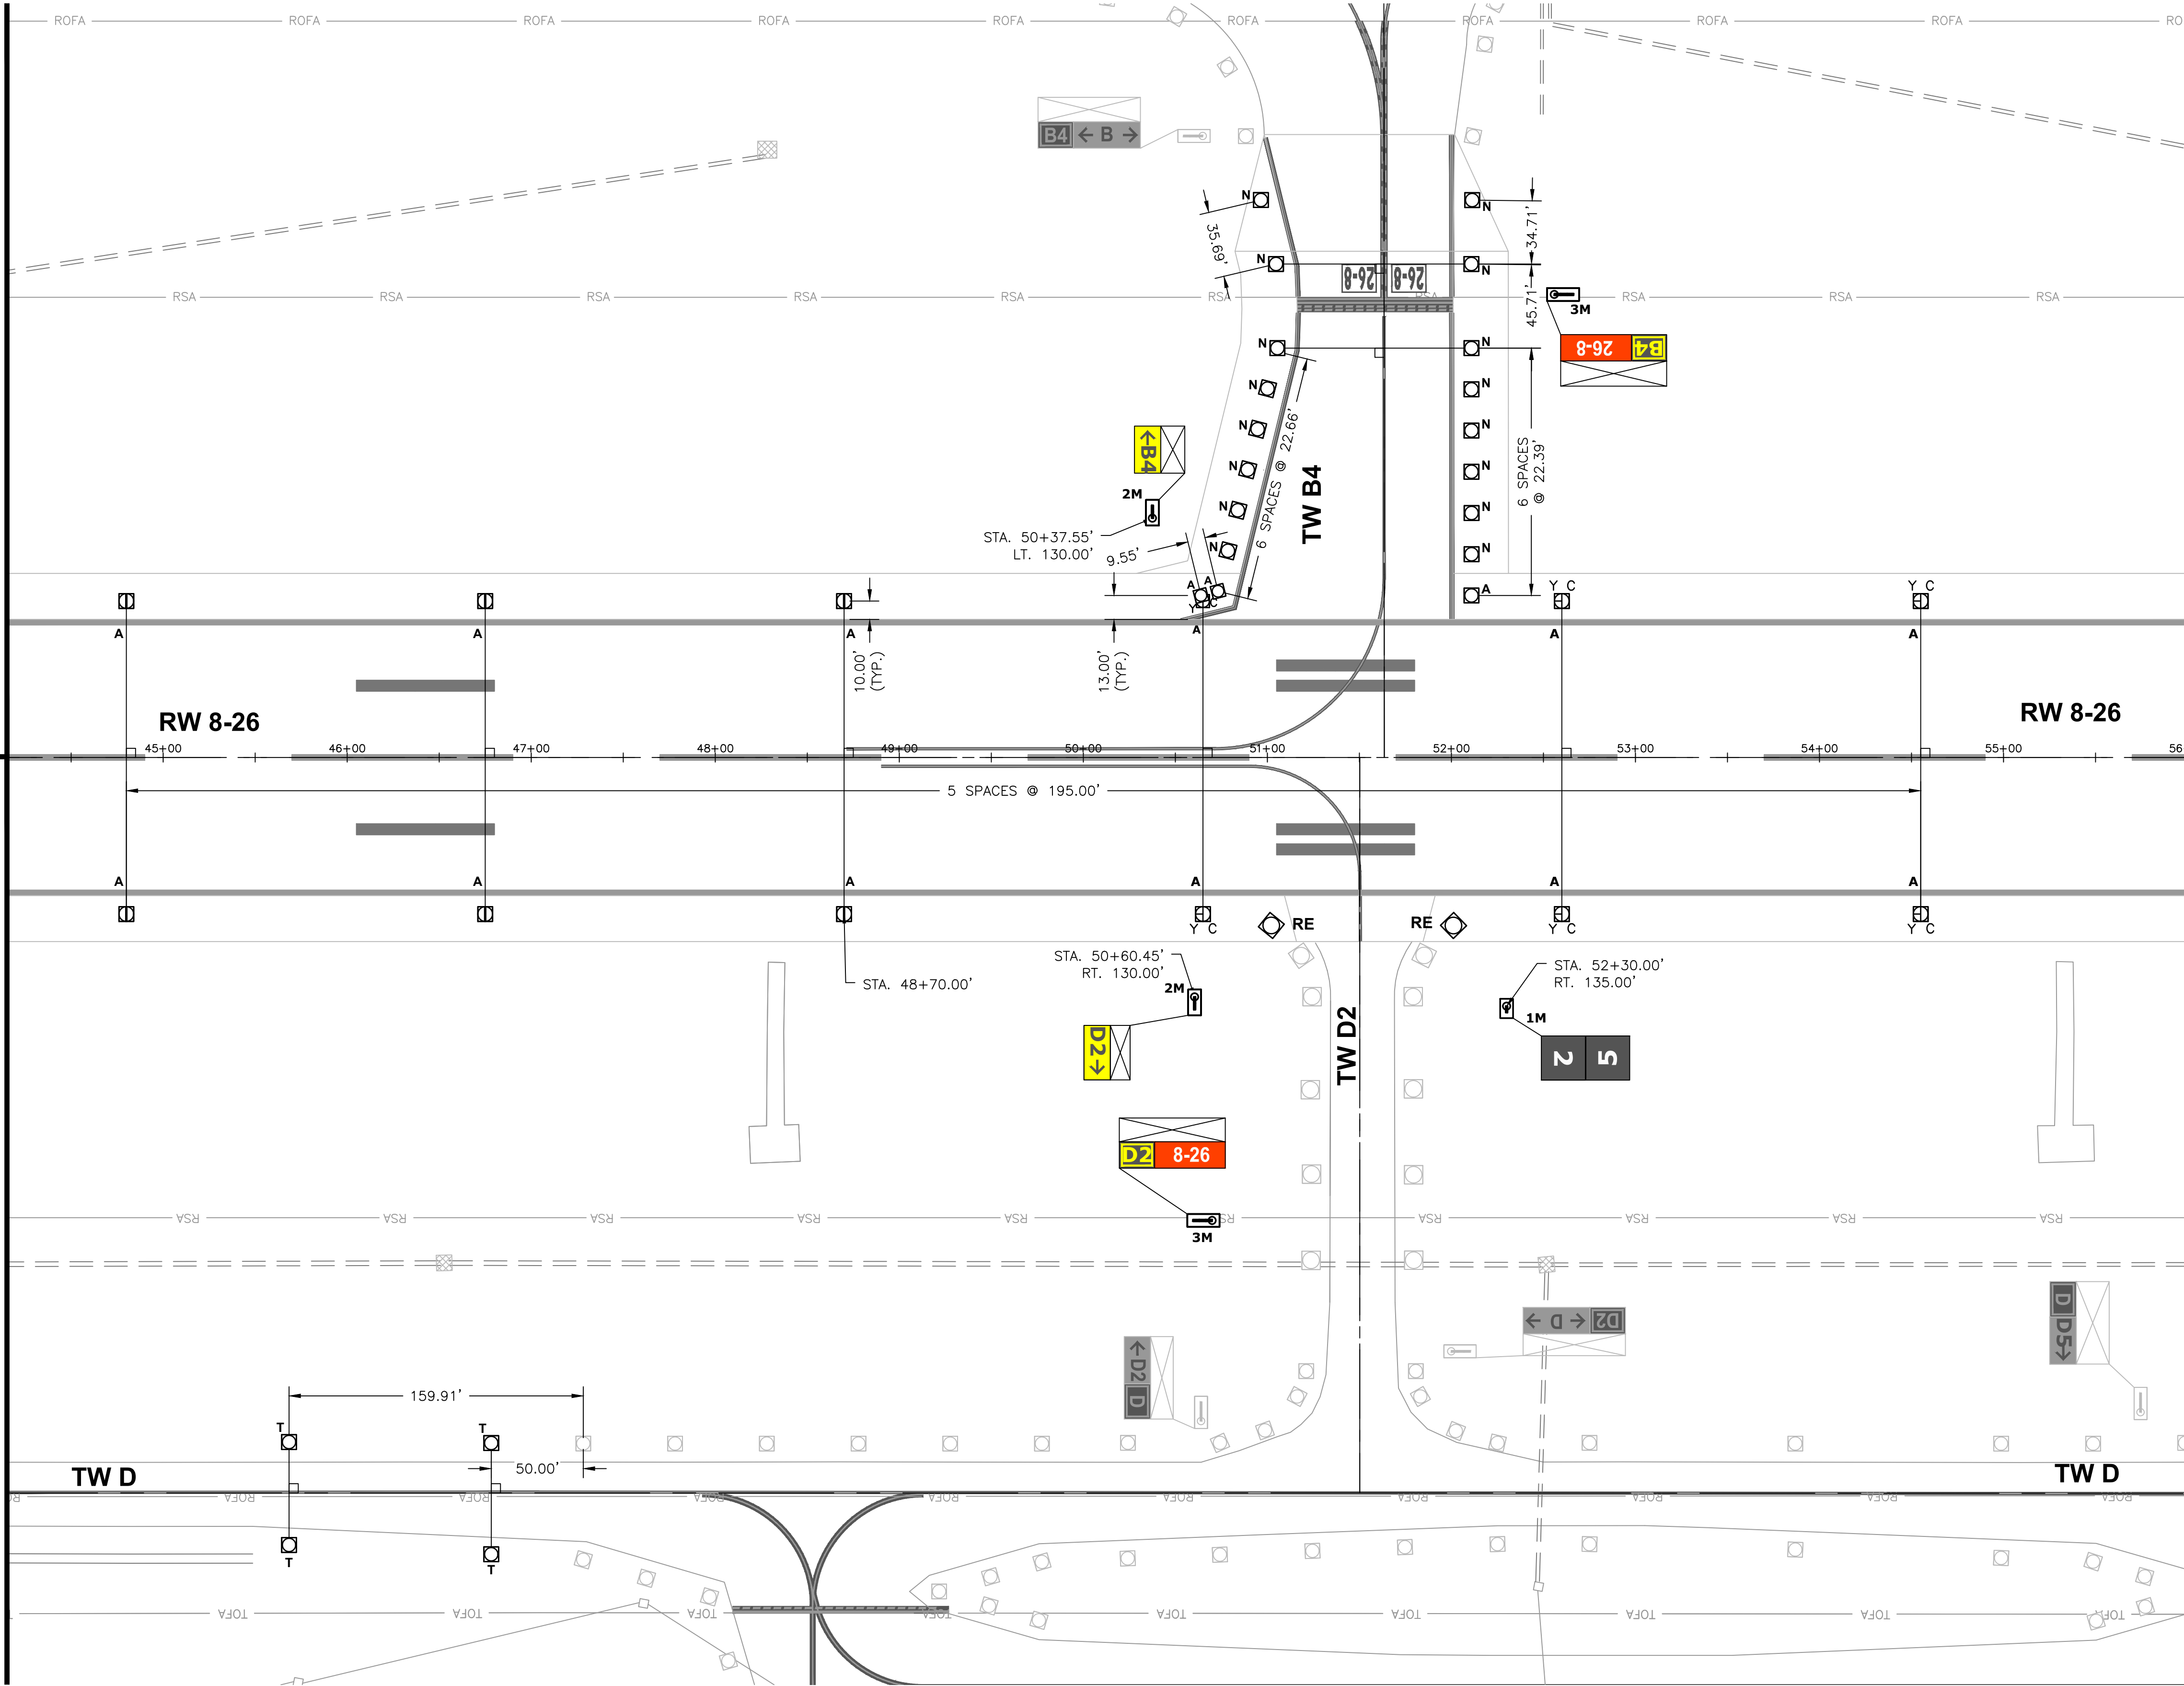

- NOTES:**
- SEE SHEET E201 FOR GENERAL LAYOUT NOTES.

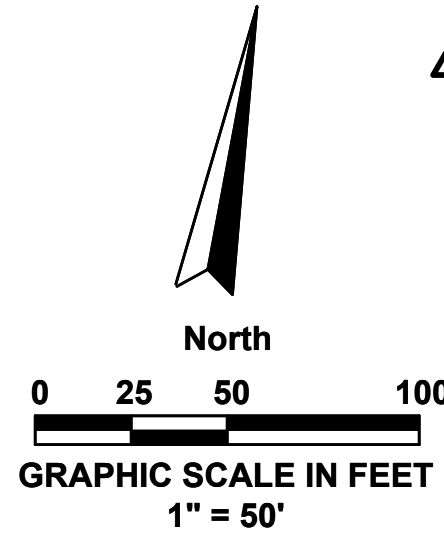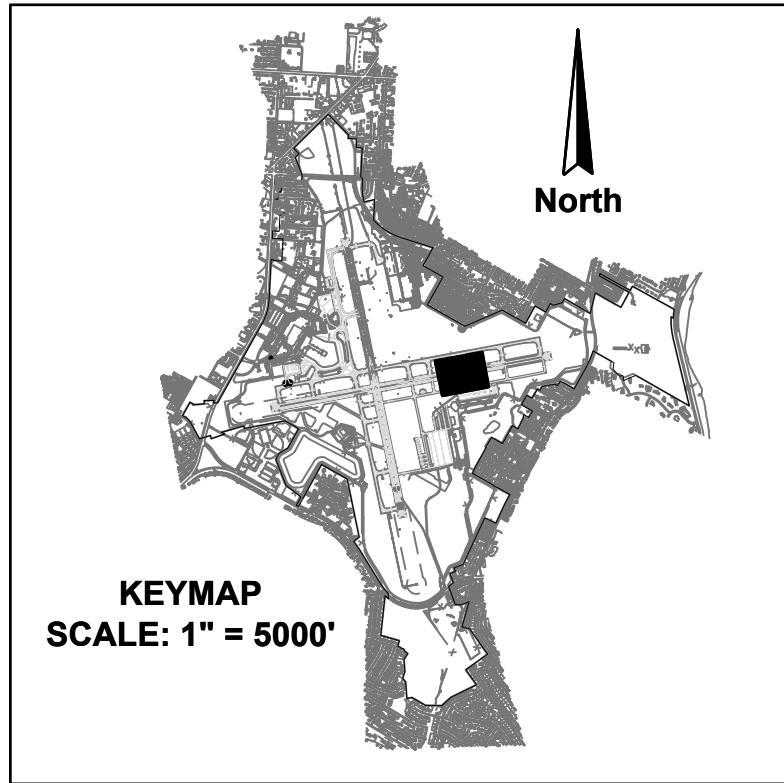

MATCH LINE - SEE SHEET E208

**RUNWAY 8-26
REHABILITATION**

PREPARED FOR
PENSACOLA INTERNATIONAL AIRPORT

**AIRFIELD LIGHTING
LAYOUT PLAN
(SHEET 7 OF 11)**

ISSUED FOR BID DRAWINGS


NO.	DATE	REVISION	BY
1	4/25	ADDENDUM 3	SAH
2			
3			
4			
5			
6			
7			
8			
9			
10			

AVCON, INC.
ENGINEERS & PLANNERS
3298 SUMMIT BLVD., SUITE 26
PENSACOLA, FL 32503
OFFICE: (850) 688-3326
CORPORATE CERTIFICATE OF
AUTHORIZATION NUMBER: 5057
WWW.AVCONINC.COM

TRANSFORMING TODAY'S IDEAS
INTO TOMORROW'S REALITY

DESIGNED BY: SAH
DRAWN BY: KJF
CHECKED BY: MAG
APPROVED BY: VCL
PROJECT NO: 24.0359.01
DATE: MARCH 28, 2025

**SHEET NUMBER
E207**

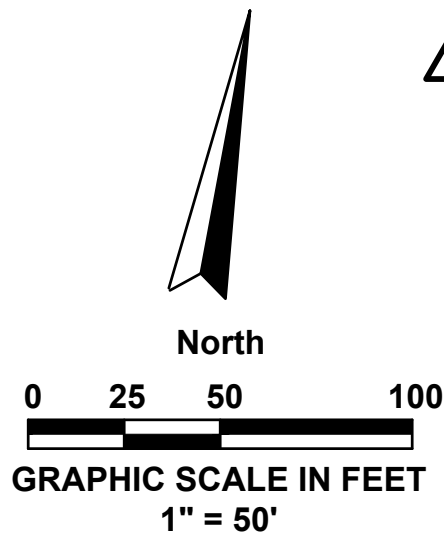

AVCON, INC.
ENGINEERS & PLANNERS
3298 SUMMIT BLVD., SUITE 26
PENSACOLA, FL 32503
OFFICE: (850) 698-3526
CORPORATE CERTIFICATE OF
AUTHORIZATION NUMBER: 5057
www.avconinc.com




DESIGNED BY: SAH
DRAWN BY: KJR
CHECKED BY: MAG
APPROVED BY: VCL
PROJECT NO: 24.0359.01
DATE: MARCH 28, 2025

SHEET NUMBER
E209

N:\359 CITY OF PENSACOLA-AIRPORT\2024.0359.01-PNS RUNWAY 8-26\000 CAD\24035901_E201-211.DWG 4/11/2025 11:21 AM

NOTES:

1. SEE SHEET E201 FOR GENERAL LAYOUT NOTES.

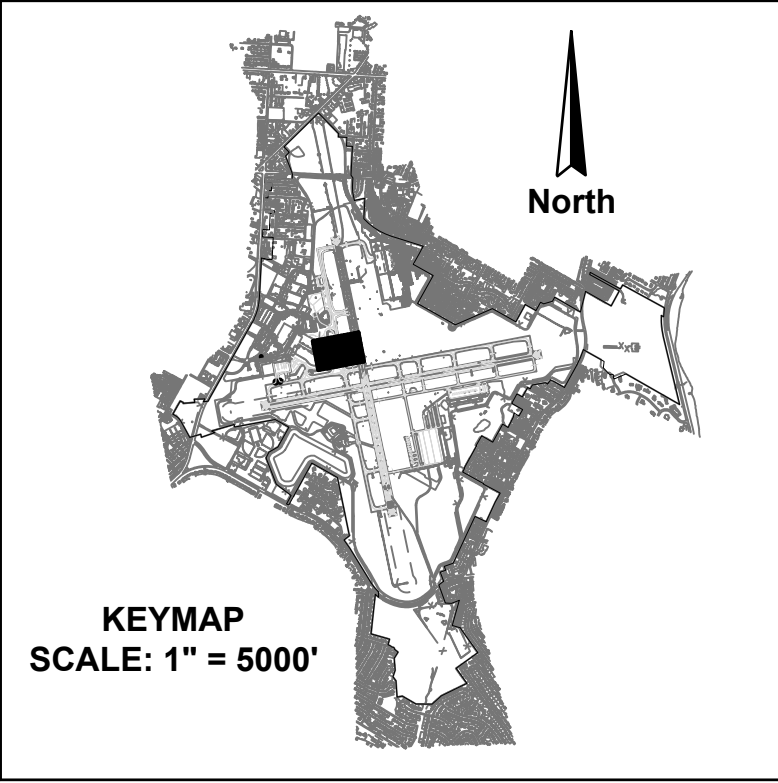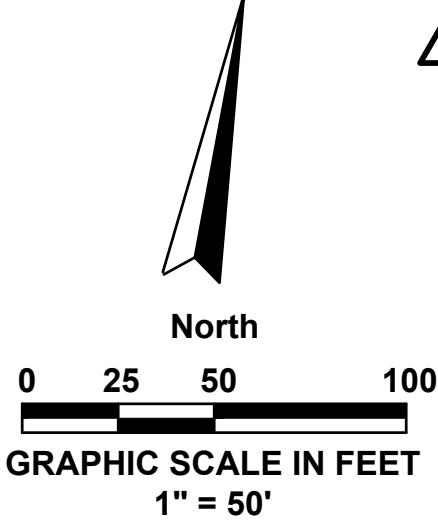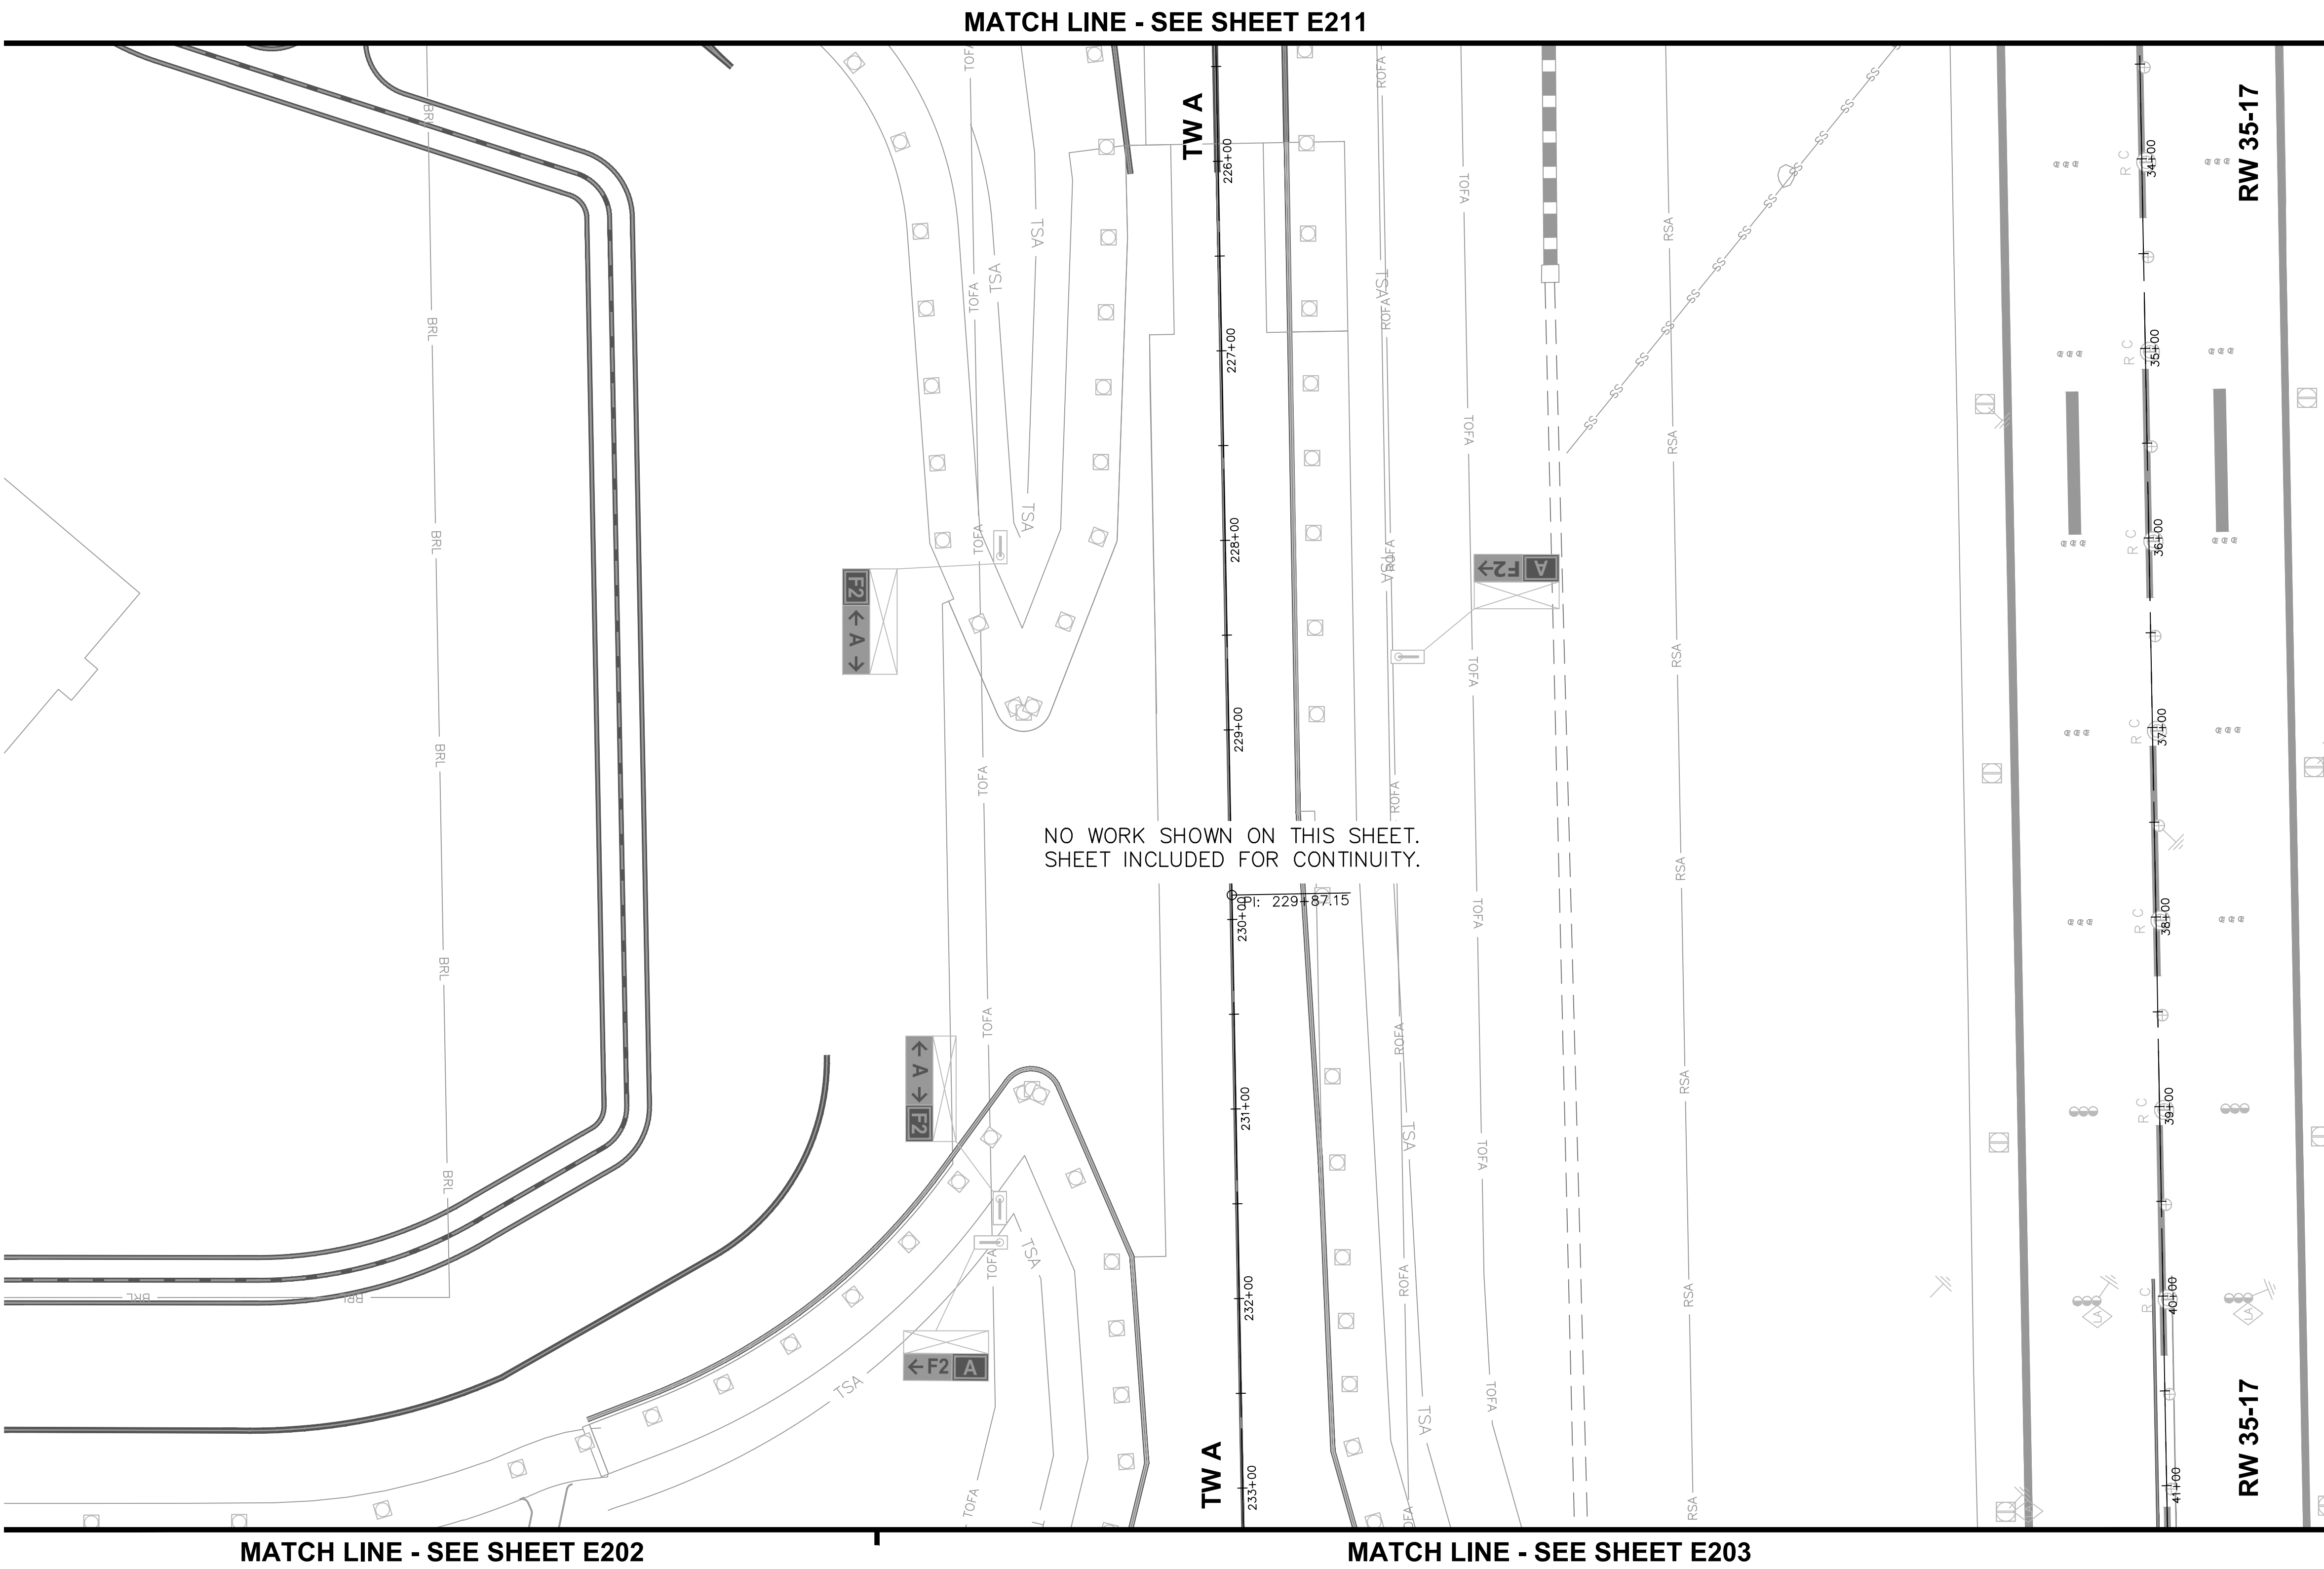

RUNWAY 8-26
REHABILITATION
PREPARED FOR
PENSACOLA INTERNATIONAL AIRPORT

AIRFIELD LIGHTING
LAYOUT PLAN
(SHEET 10 OF 11)
ISSUED FOR BID DRAWINGS

NO.	DATE	REVISION	BY
1	4/25	ADDENDUM 3	SAH
2			
3			
4			
5			
6			
7			
8			
9			
10			

AVCON, INC.
ENGINEERS & PLANNERS
3298 SUMMIT BLVD., SUITE 26
PENSACOLA, FL 32503
OFFICE: (850) 688-3326
CORPORATE CERTIFICATE OF
AUTHORIZATION NUMBER: 5057
WWW.AVCONINC.COM

TRANSFORMING TODAY'S IDEAS
INTO TOMORROW'S REALITY




DESIGNED BY: SAH
DRAWN BY: KJF
CHECKED BY: MAG
APPROVED BY: VCL
PROJECT NO: 24.0359.01
DATE: MARCH 28, 2025

SHEET NUMBER
E210

THIS DOCUMENT CONTAINS PRIVILEGED AND PROPRIETARY INFORMATION, ALL OF WHICH IS EXPRESSLY PROVIDED BY AVCON, INC., FOR USE BY THE INTENDED RECIPIENT, AND FOR A SPECIFIC PURPOSE. WITHOUT THE EXPRESS WRITTEN CONSENT OF AVCON, INC. ANY DISTRIBUTION, REPRODUCTION, OR OTHER USE OF THIS DOCUMENT, IN WHOLE OR IN PART, IS STRICTLY PROHIBITED.

N:\359 CITY OF PENSACOLA-AIRPORT\2024.0359.01-PNS RUNWAY 8-26\000 CAD\24035901_E201-211.DWG 4/11/2025 11:22 AM

NOTES:
1. SEE SHEET E201 FOR GENERAL LAYOUT NOTES.

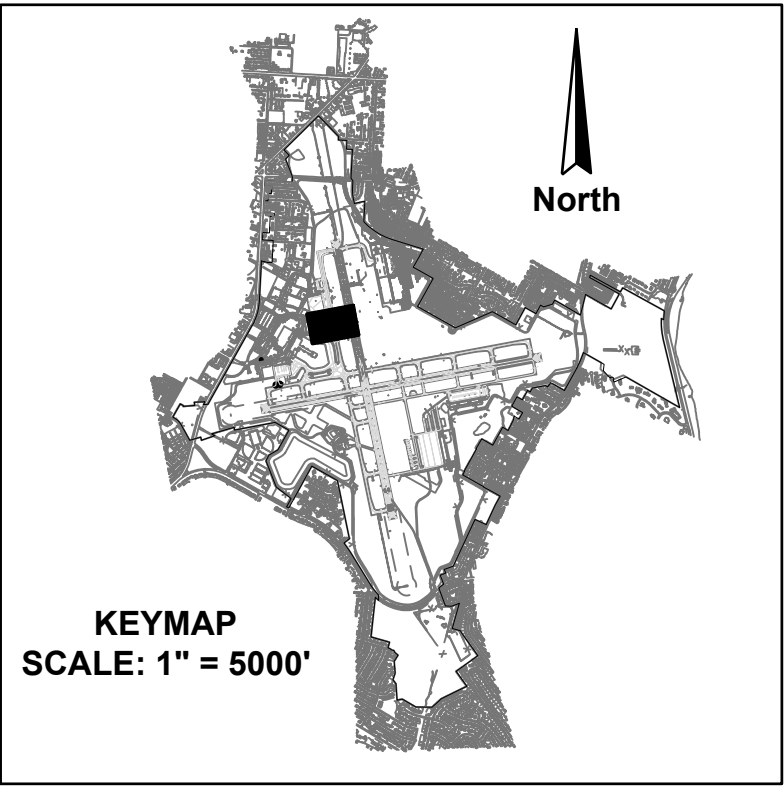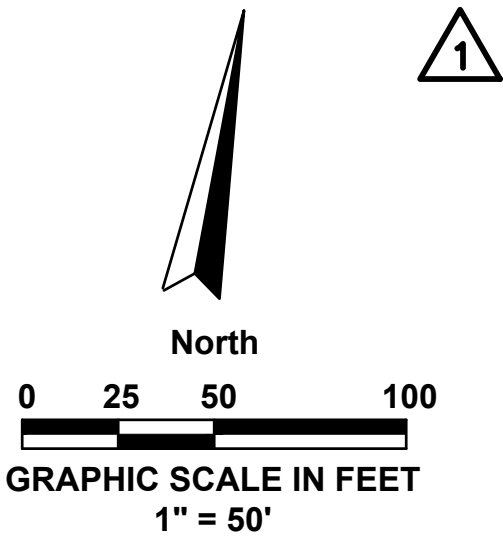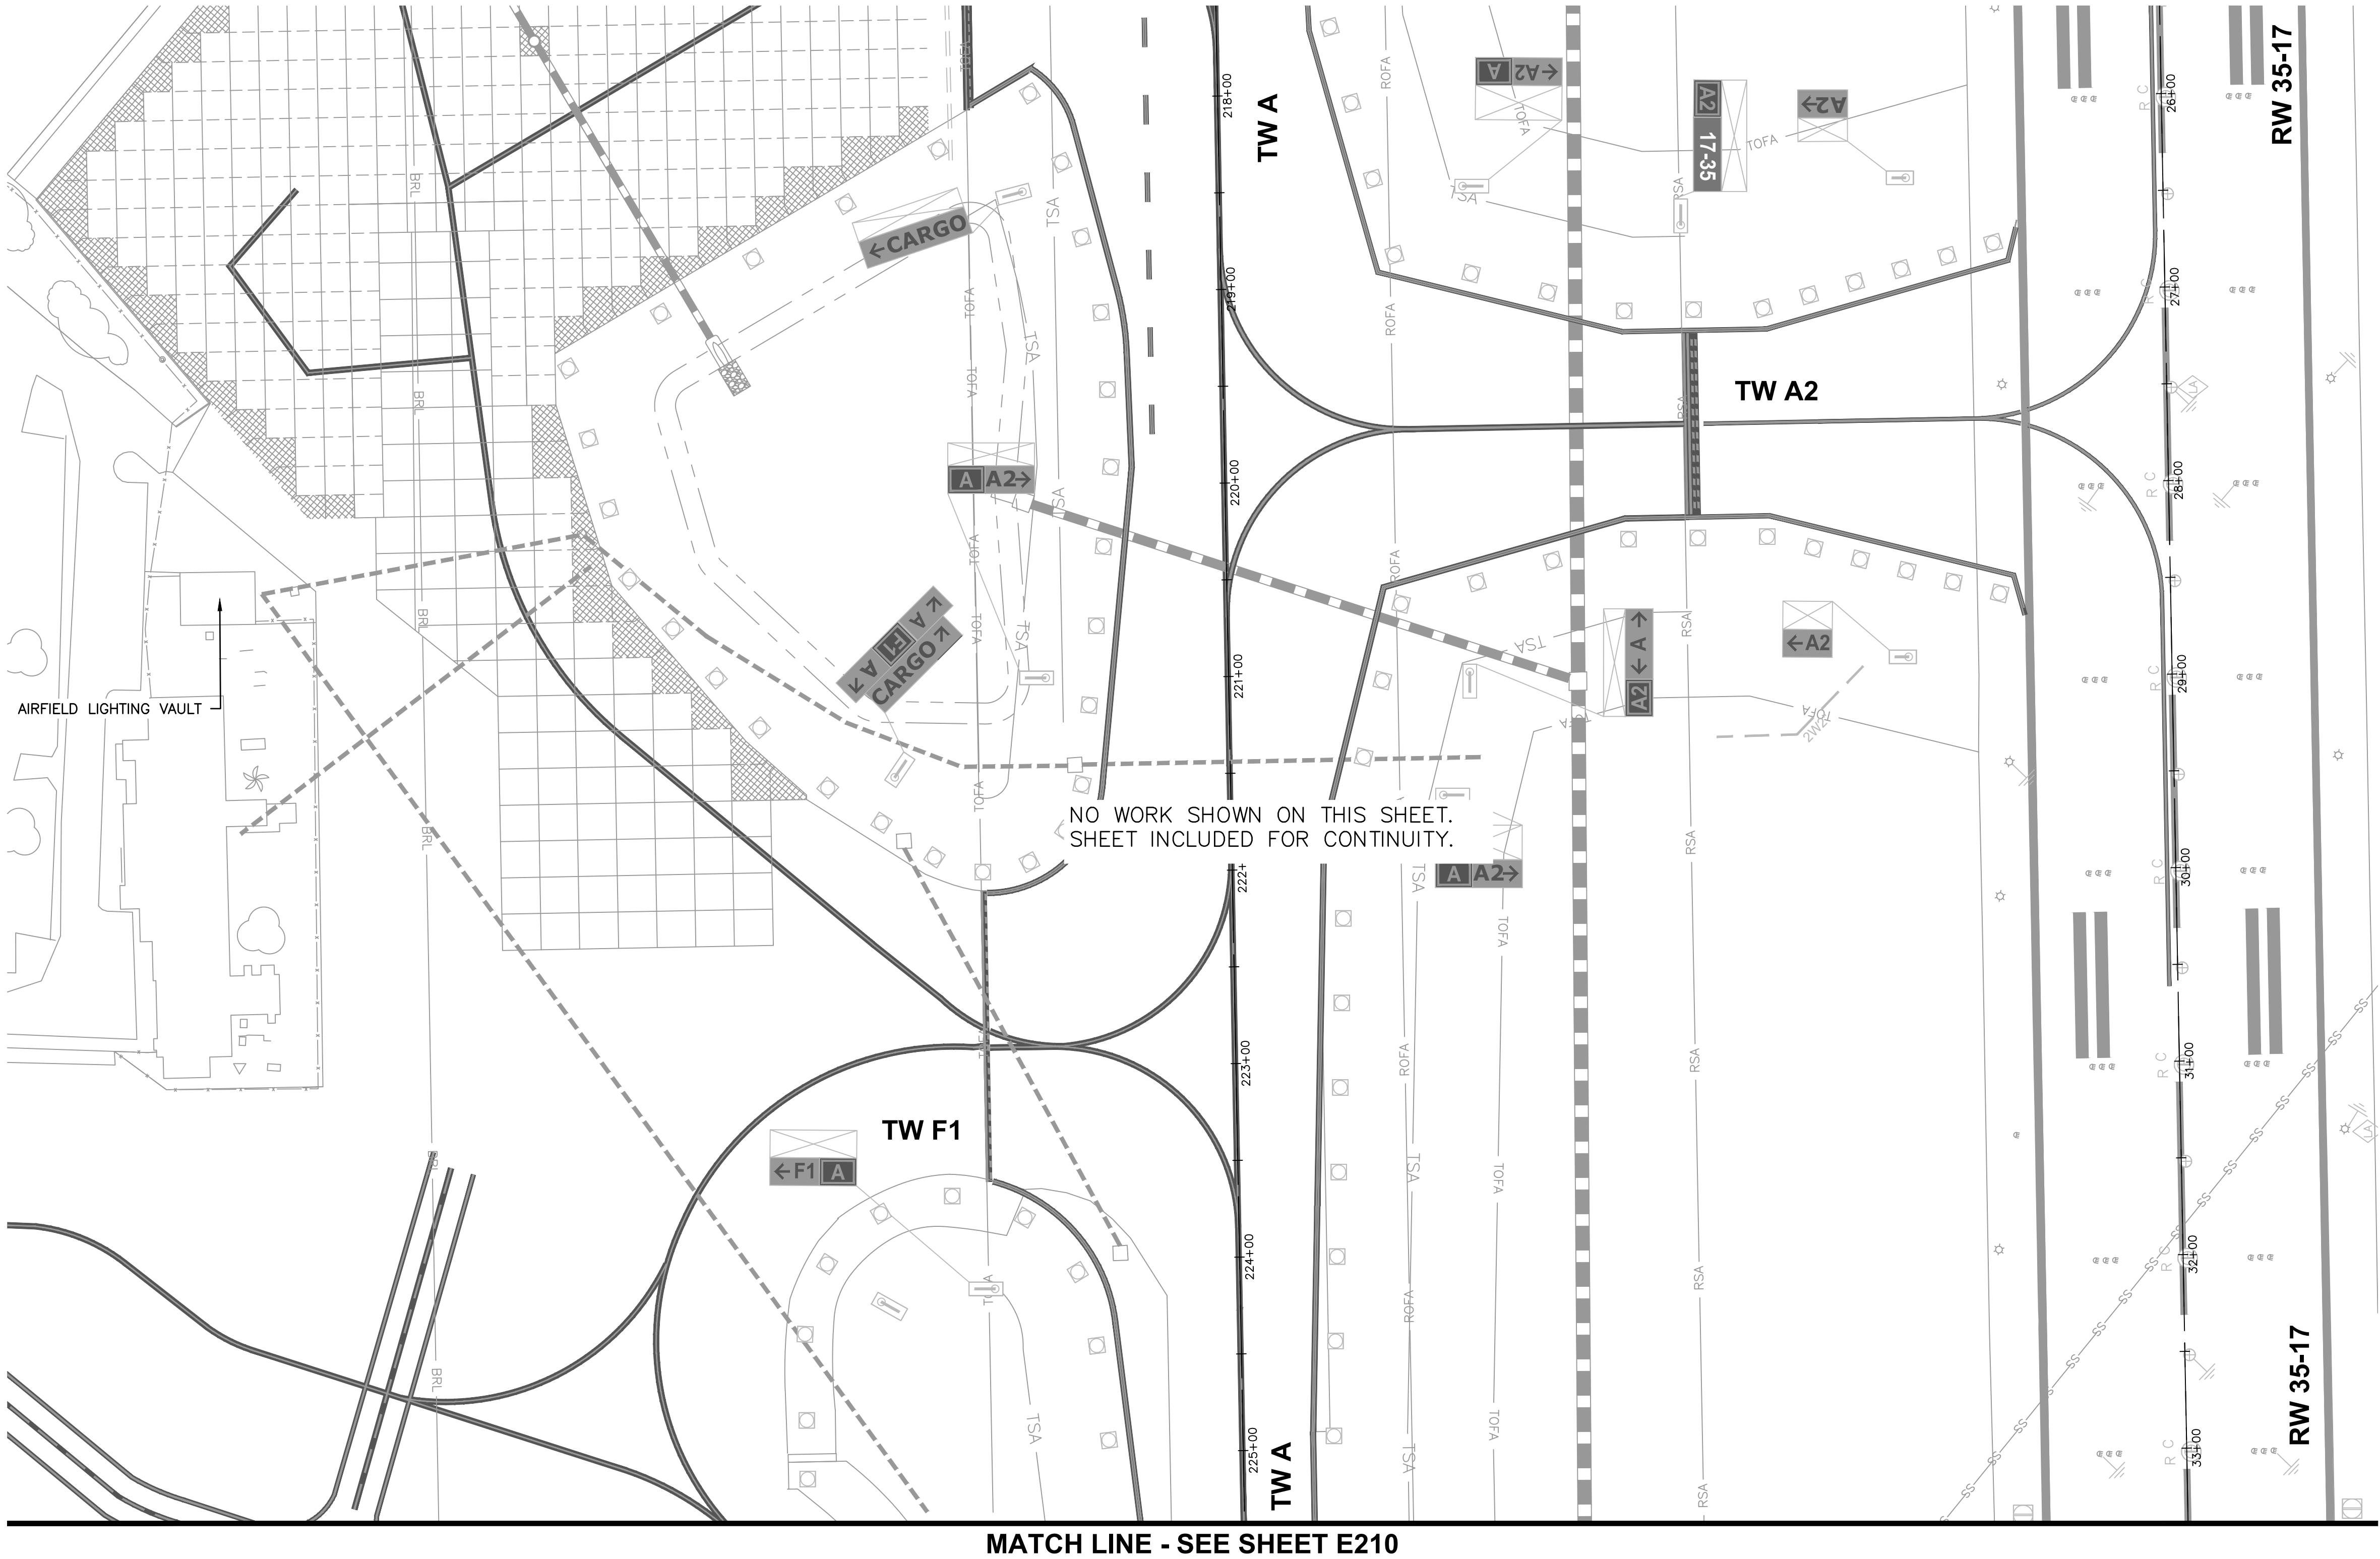

**RUNWAY 8-26
REHABILITATION**
PREPARED FOR
PENSACOLA INTERNATIONAL AIRPORT

**AIRFIELD LIGHTING
LAYOUT PLAN
(SHEET 11 OF 11)**
ISSUED FOR BID DRAWINGS

NO.	DATE	REVISION	BY
1	4/25	ADDENDUM 3	SAH

R:\NICKLE-CAD\02_LOADS\WPG\Avcon_1000.pwg
AVCON, INC.
ENGINEERS & PLANNERS
3298 SUMMIT BLVD., SUITE 26
PENSACOLA, FL 32503
OFFICE: (850) 688-3326
CORPORATE CERTIFICATE OF
AUTHORIZATION NUMBER: 5057
WWW.AVCONINC.COM

**TRANSFORMING TODAY'S IDEAS
INTO TOMORROW'S REALITY**

DESIGNED BY: SAH
DRAWN BY: KJF
CHECKED BY: MAG
APPROVED BY: VCL
PROJECT NO: 24.0359.01
DATE: MARCH 28, 2025

**SHEET NUMBER
E211**

THIS DOCUMENT CONTAINS PRIVILEGED AND PROPRIETARY INFORMATION, ALL OF WHICH IS EXPRESSLY PROVIDED BY AVCON, INC., FOR USE BY THE INTENDED RECIPIENT, AND FOR A SPECIFIC PURPOSE. WITHOUT THE EXPRESS WRITTEN CONSENT OF AVCON, INC., ANY DISTRIBUTION, REPRODUCTION, OR OTHER USE OF THIS DOCUMENT, IN WHOLE OR IN PART, IS STRICTLY PROHIBITED.